




Pipe Holder Holes Detail (1 : 10)

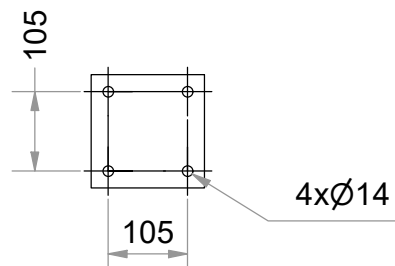


Transmitter Holes Detail (1 : 10)

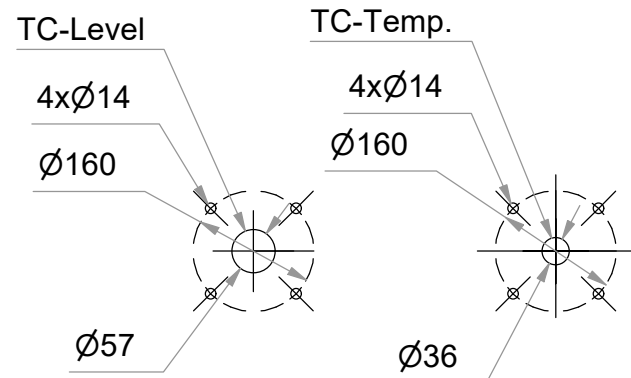


Past. Holes Detail (1 : 10)

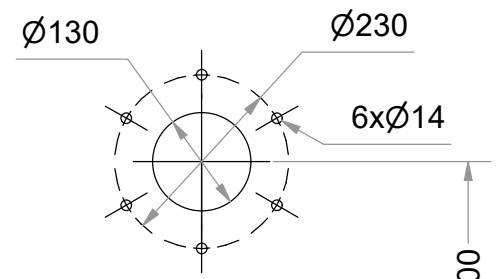

Biomass Holes Detail (1 : 10)

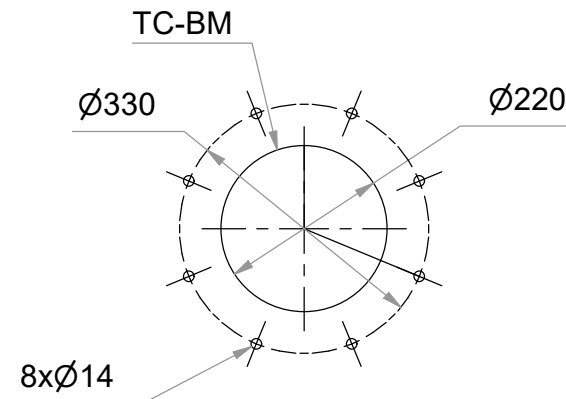


Anti Foam Holes Detail (1 : 10)

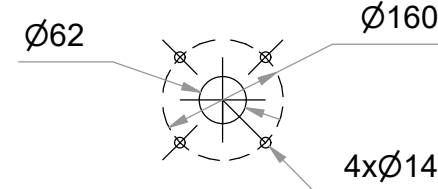

TC-Camera Sight Glass

TC-Light Sight Glass

A (1 : 20)

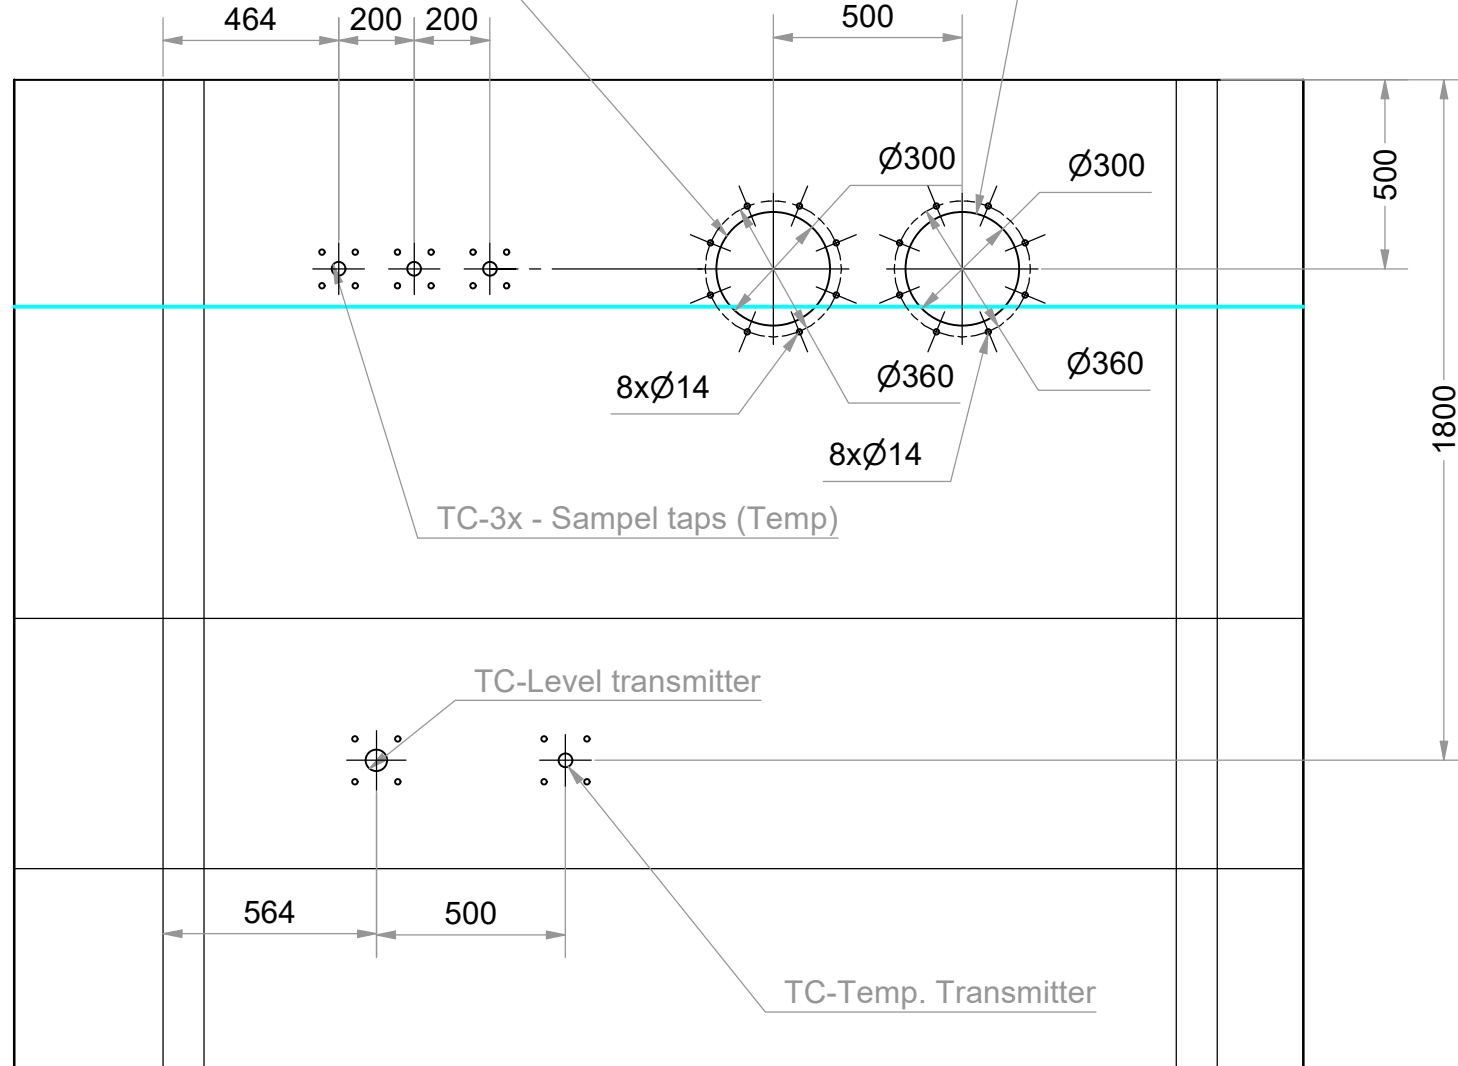

Centerline to Digester 2

Pipe Holder holes for BioGas Pipe





TC-GasMix 1

Freeboard

600

Pipe Holder holes for Past. Connection

TC-GasMix 2

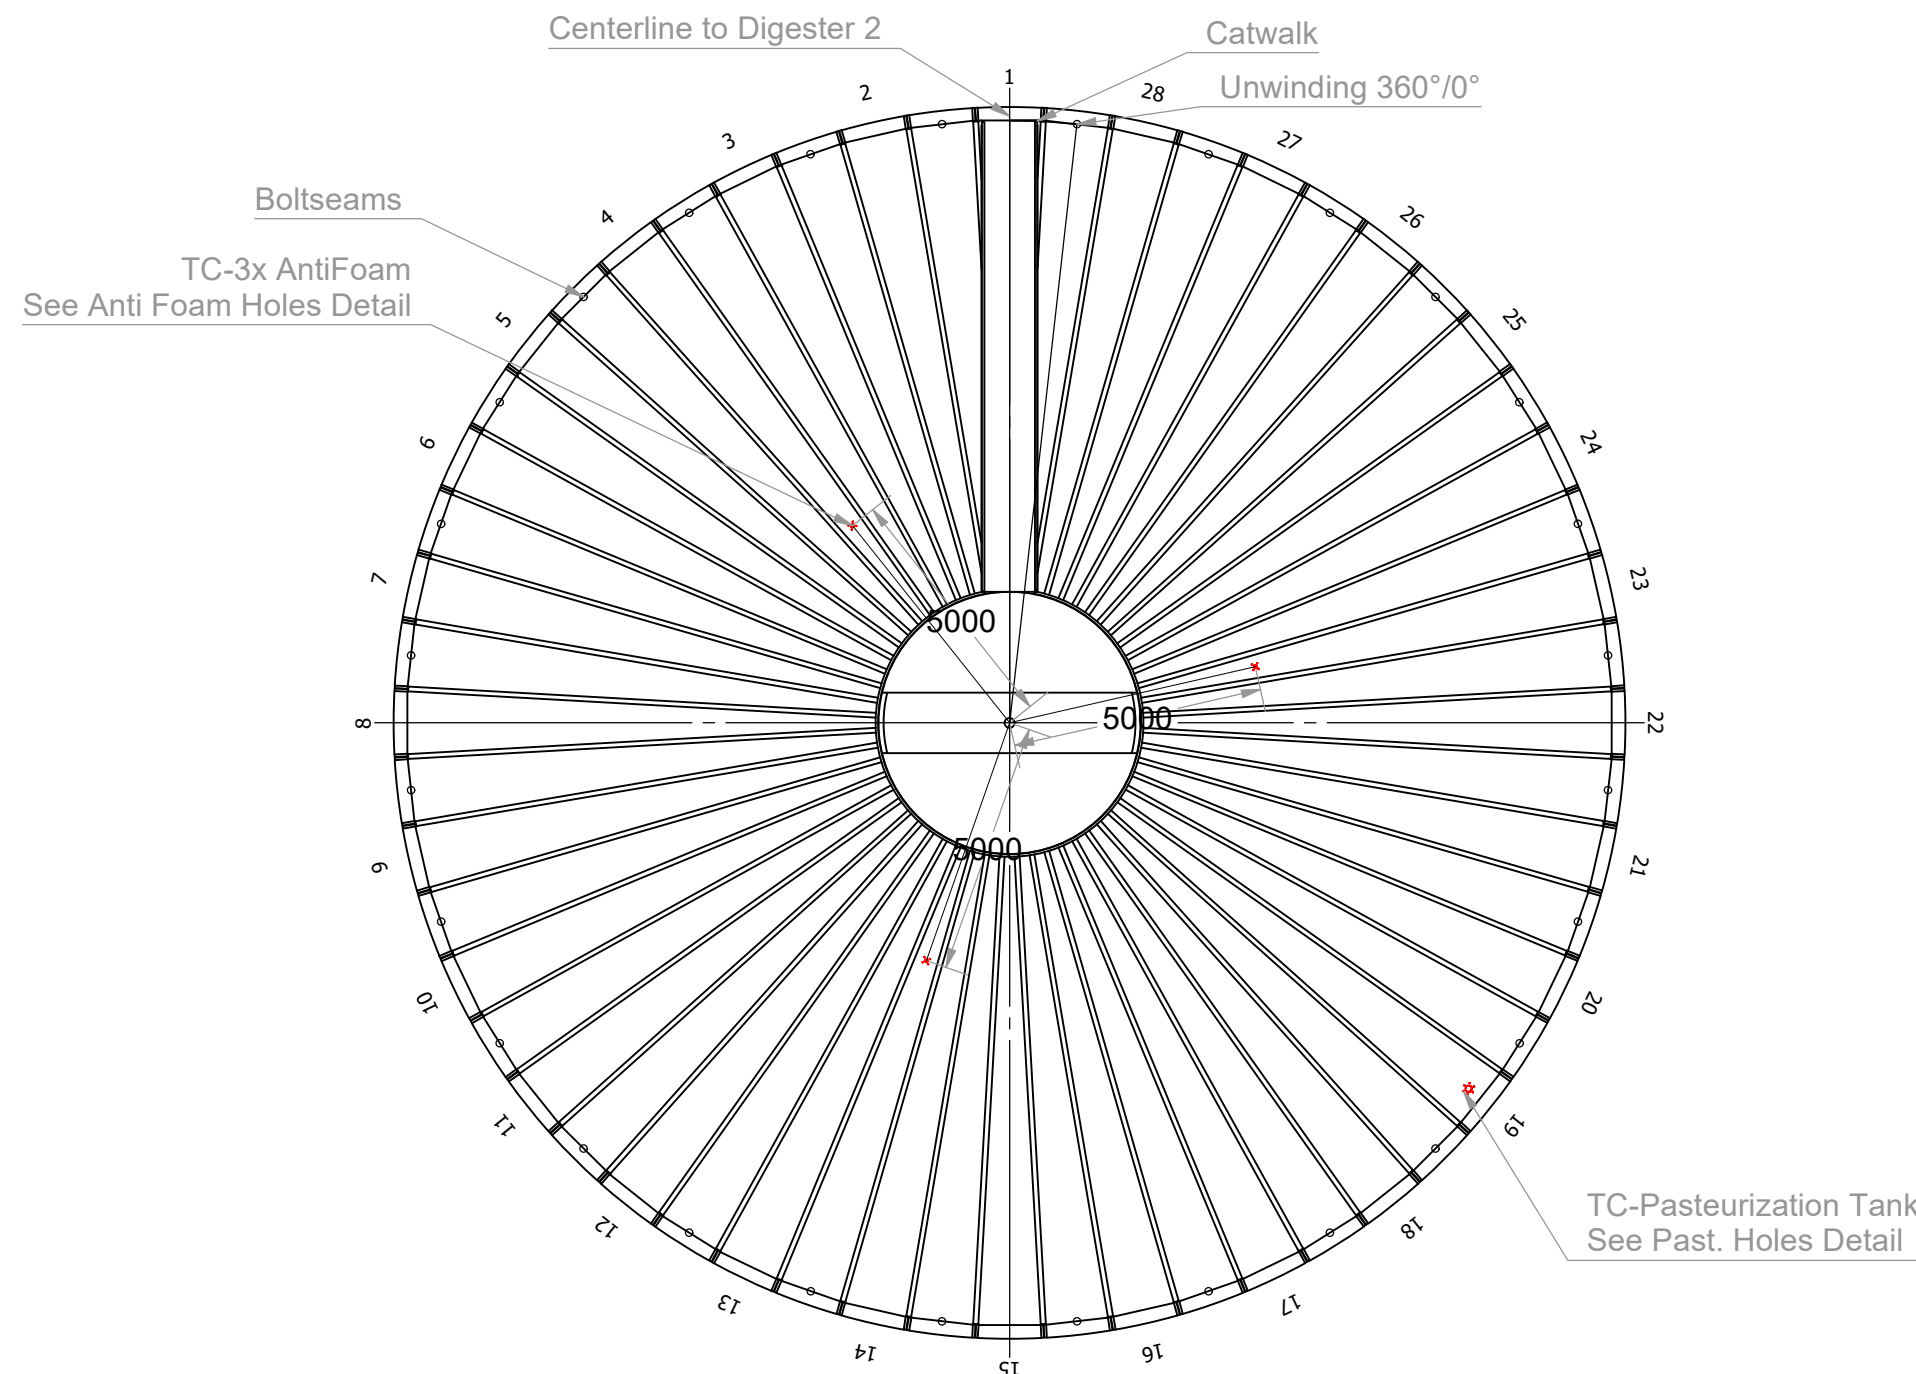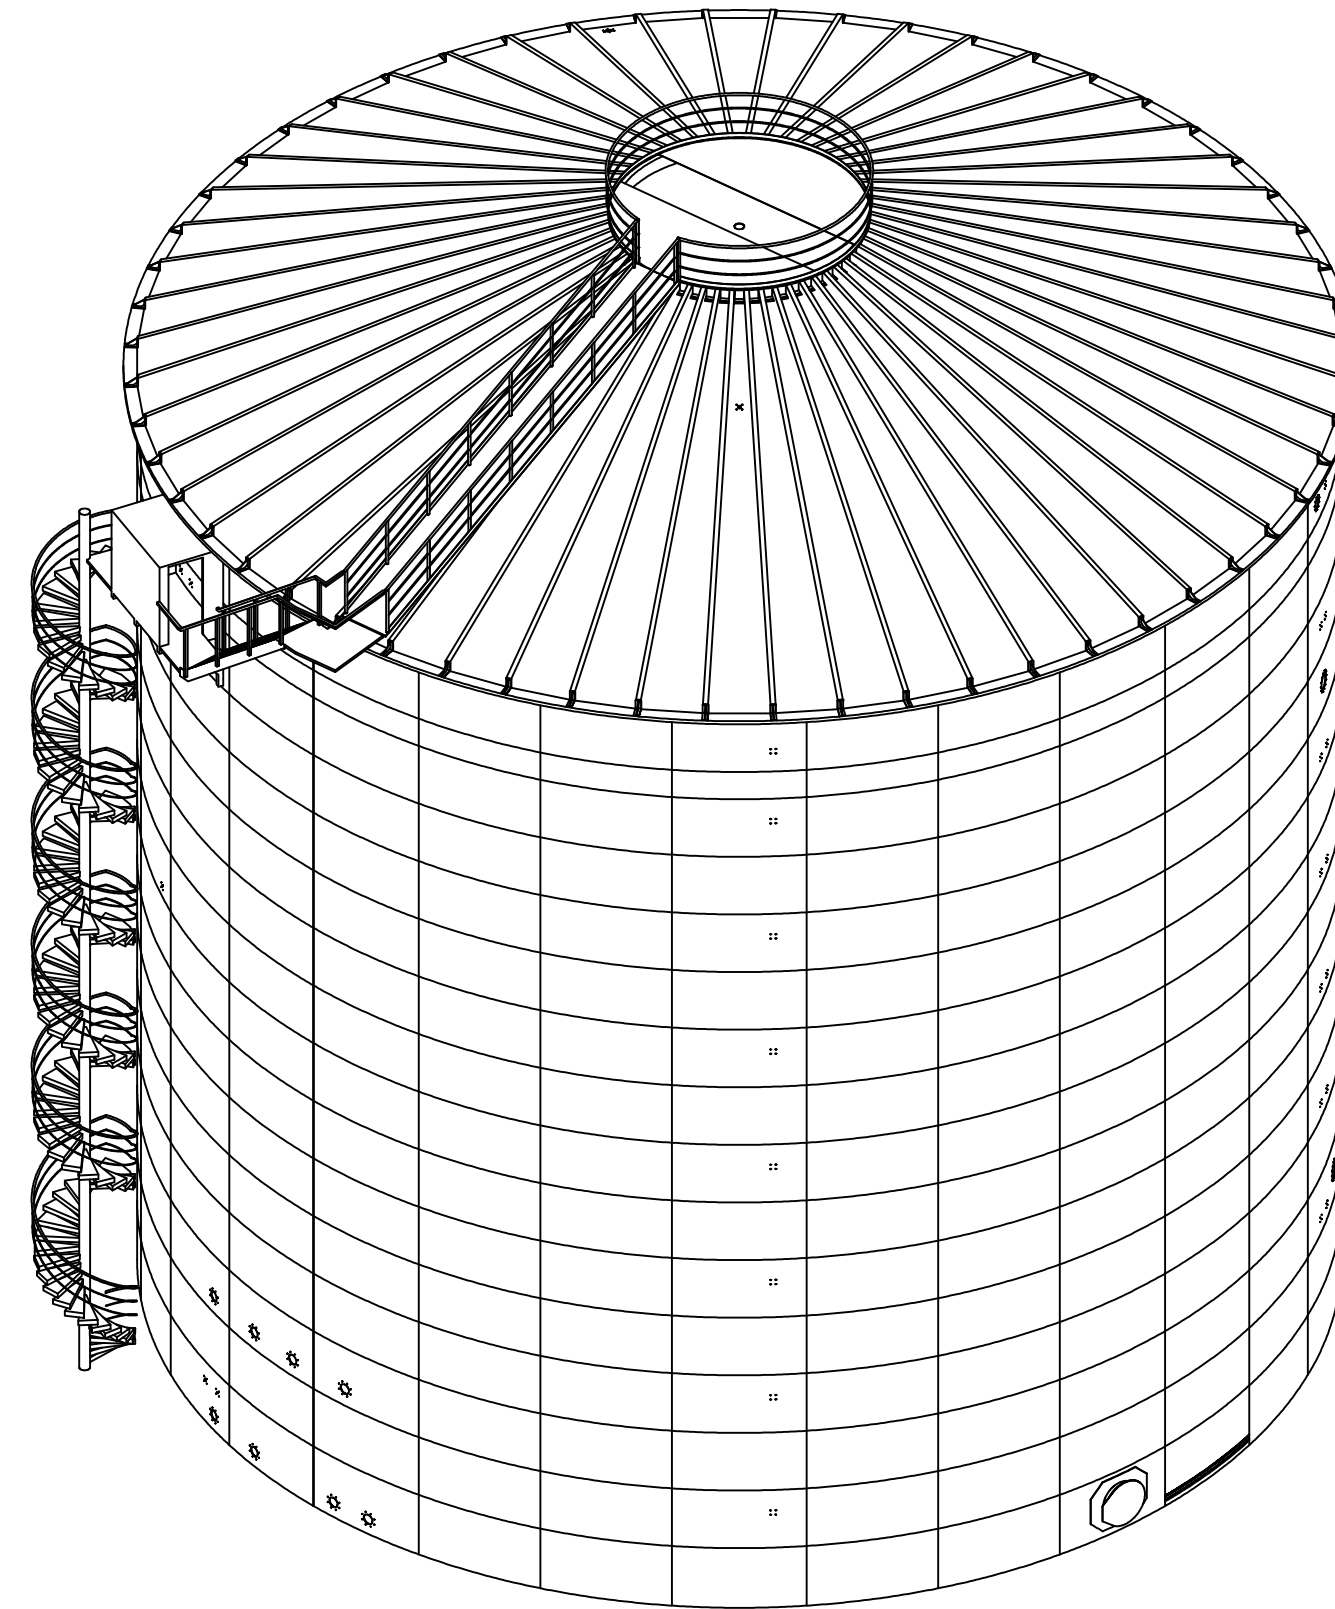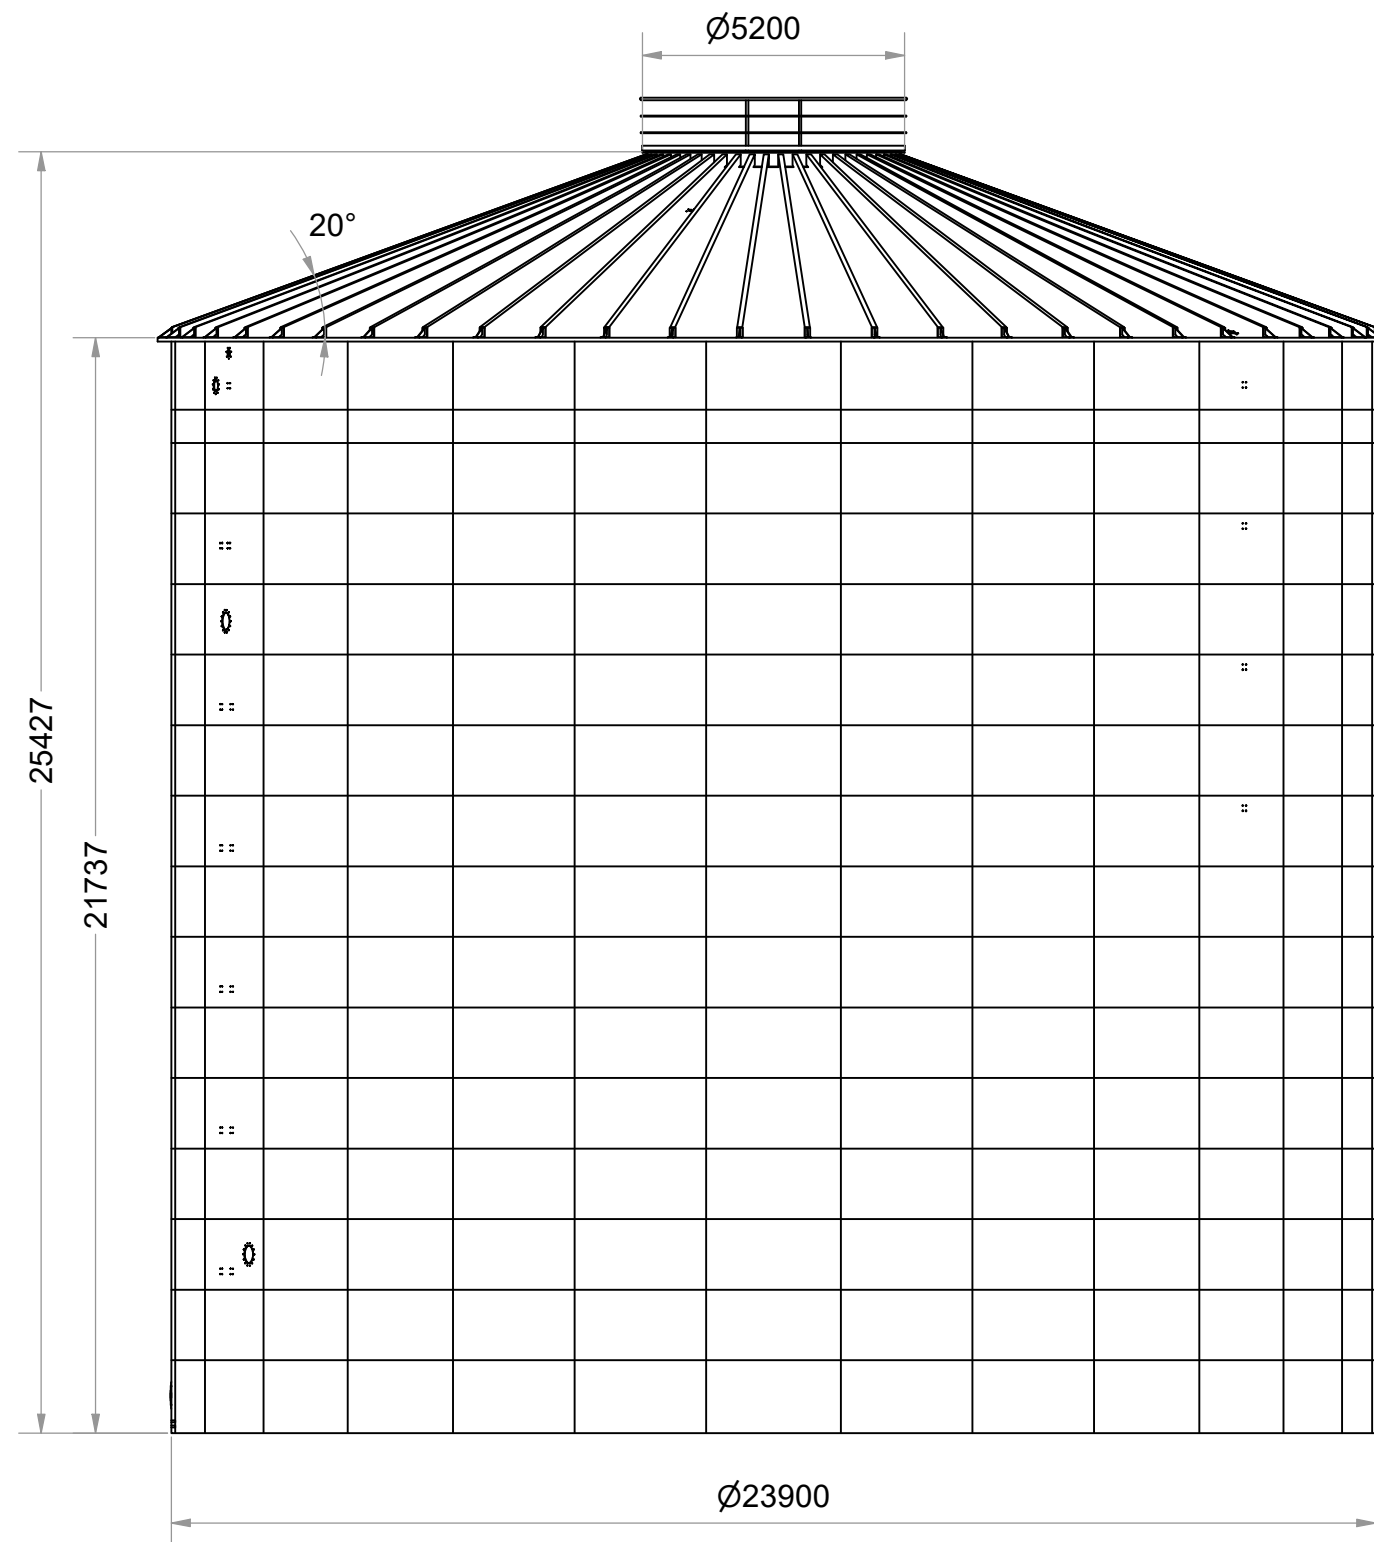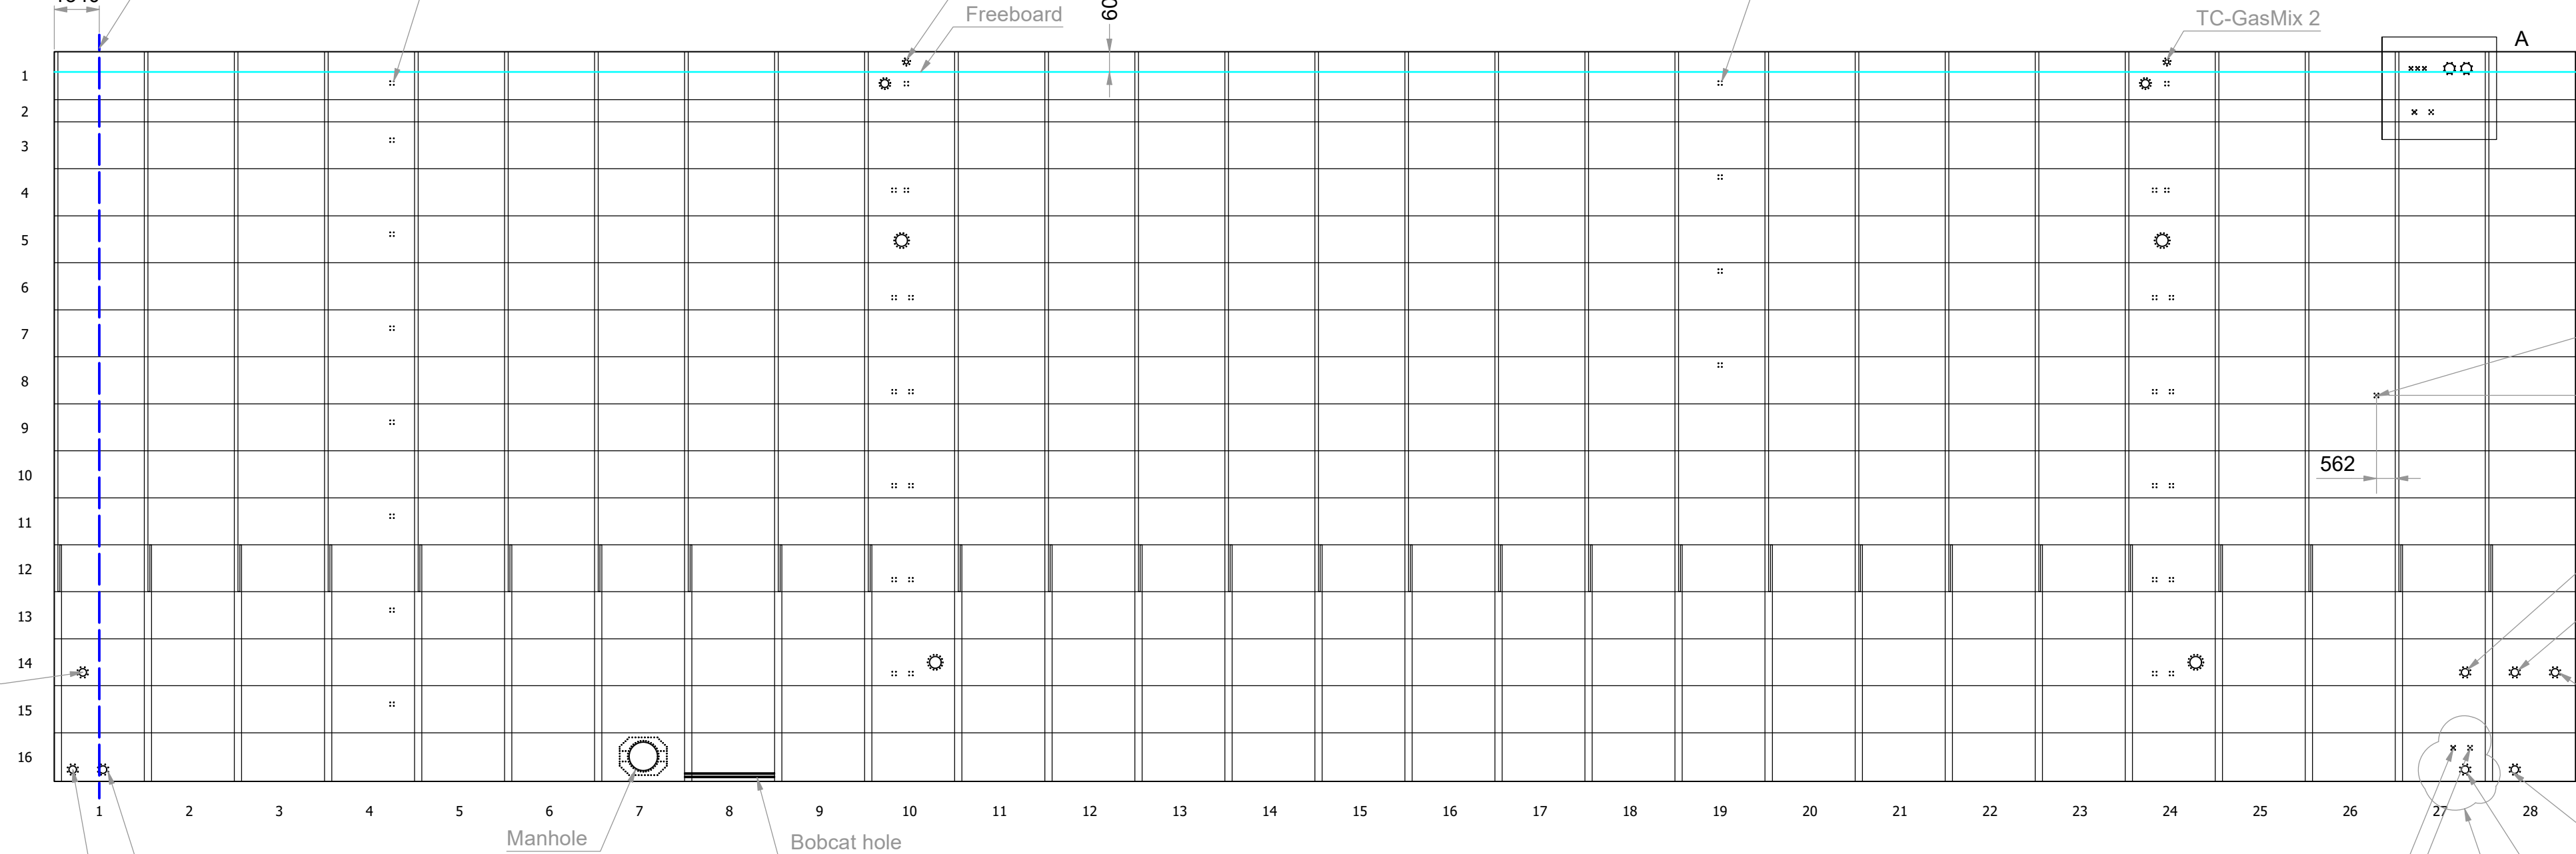

See DWG for hole size and placement on sheet

D	18-01-2025	JLH	added spare valve	JSc
C	25-09-2024	JLH	TT transmitter hole moved to ladder location	JLH
B	24-09-2024	JLH	Holes adapted from Schumann drawing	JLH
Rev	Date	Rev By	Description	Approved
Revision History				
Denne tegning må ikke overføres til, kopieres eller udrykkes af uvedkommende uden vor tilladelse.				
This drawing remains our property. Its use without due authority is forbidden, and will lead to legal action.				
Diese Zeichnung ist unser Eigentum. Unbefugte Benutzung ist verboten und wird gerichtlich verfolgt.				
Ce dessin est notre propriété. Toute utilisation indue est interdite sous peine de poursuites légales.				
Bigadan A/S Dronning Sophies Allé 7A DK - 8660 Skanderborg Tel. : +45 86 57 90 90 www.bigadan.com			Drawing State	
4003 - Nurmo Bioenergia Area 04.1 Digester 1 - 9500m³			Released	
Date : 19-09-2023			Sheet : 1 of 1	