

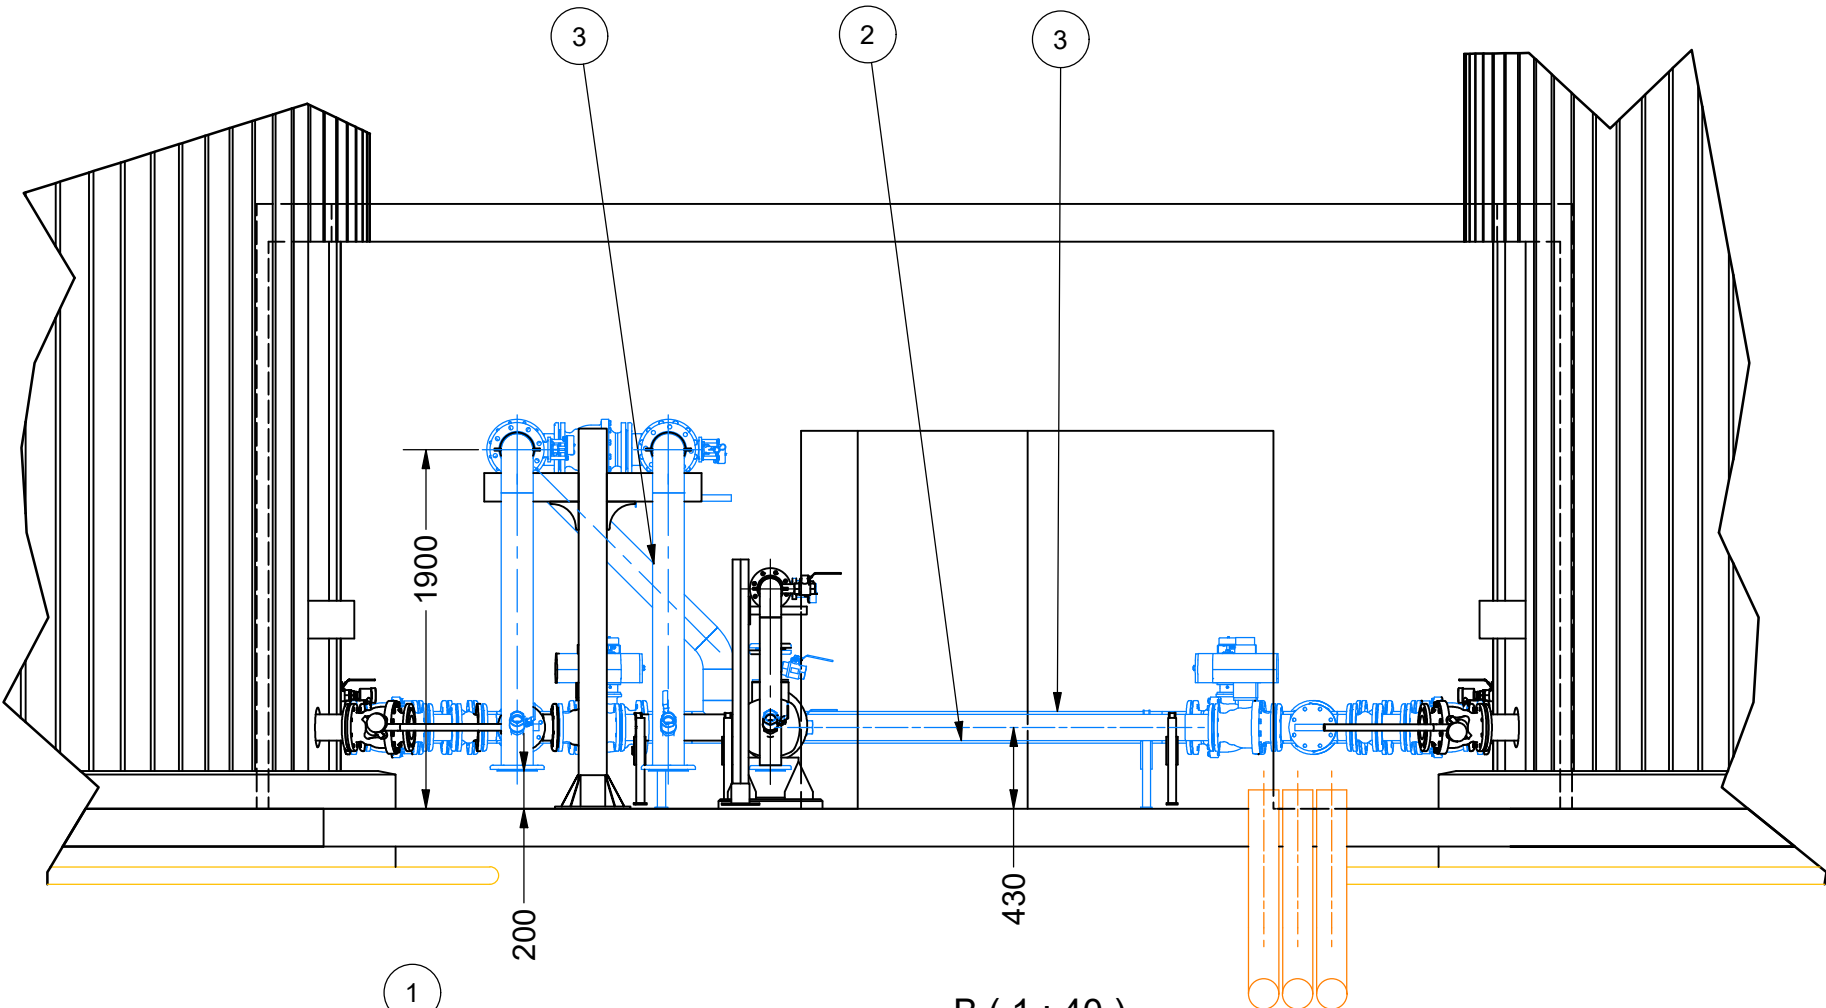
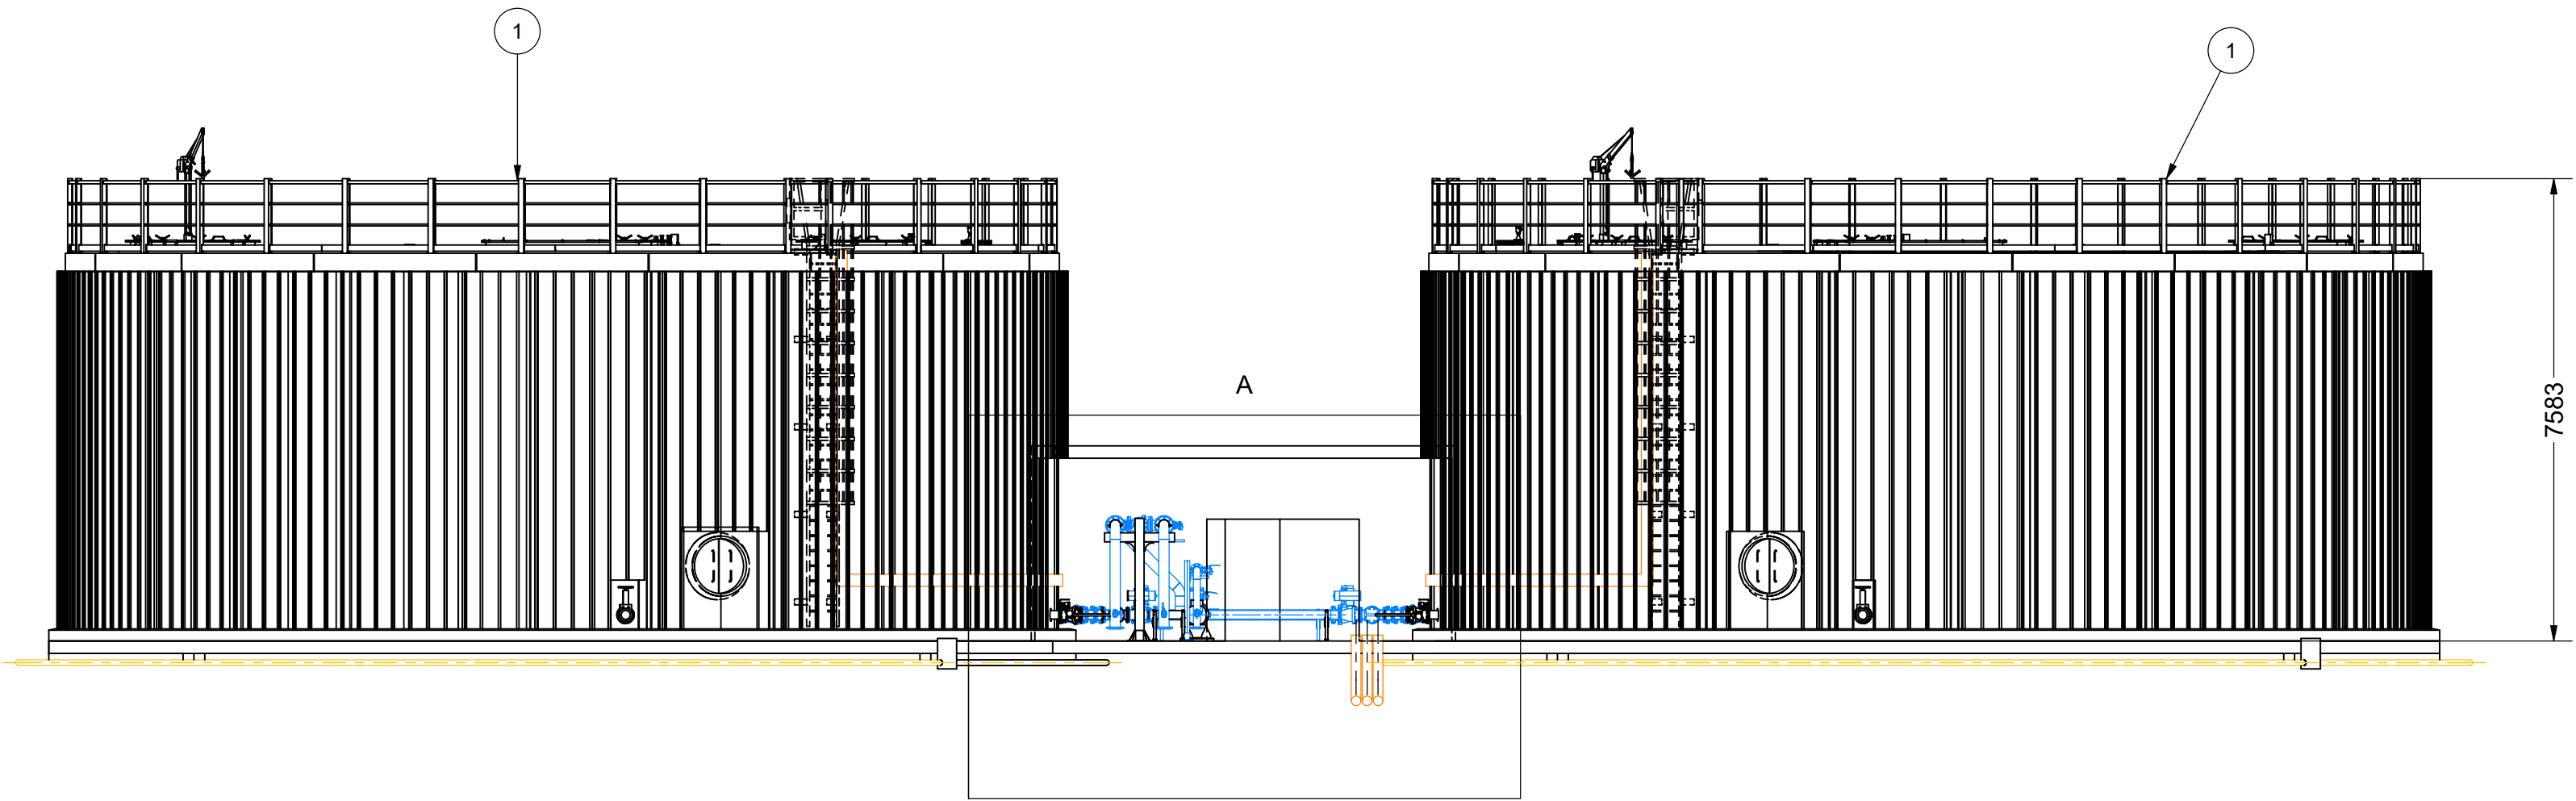


A (1 : 40)

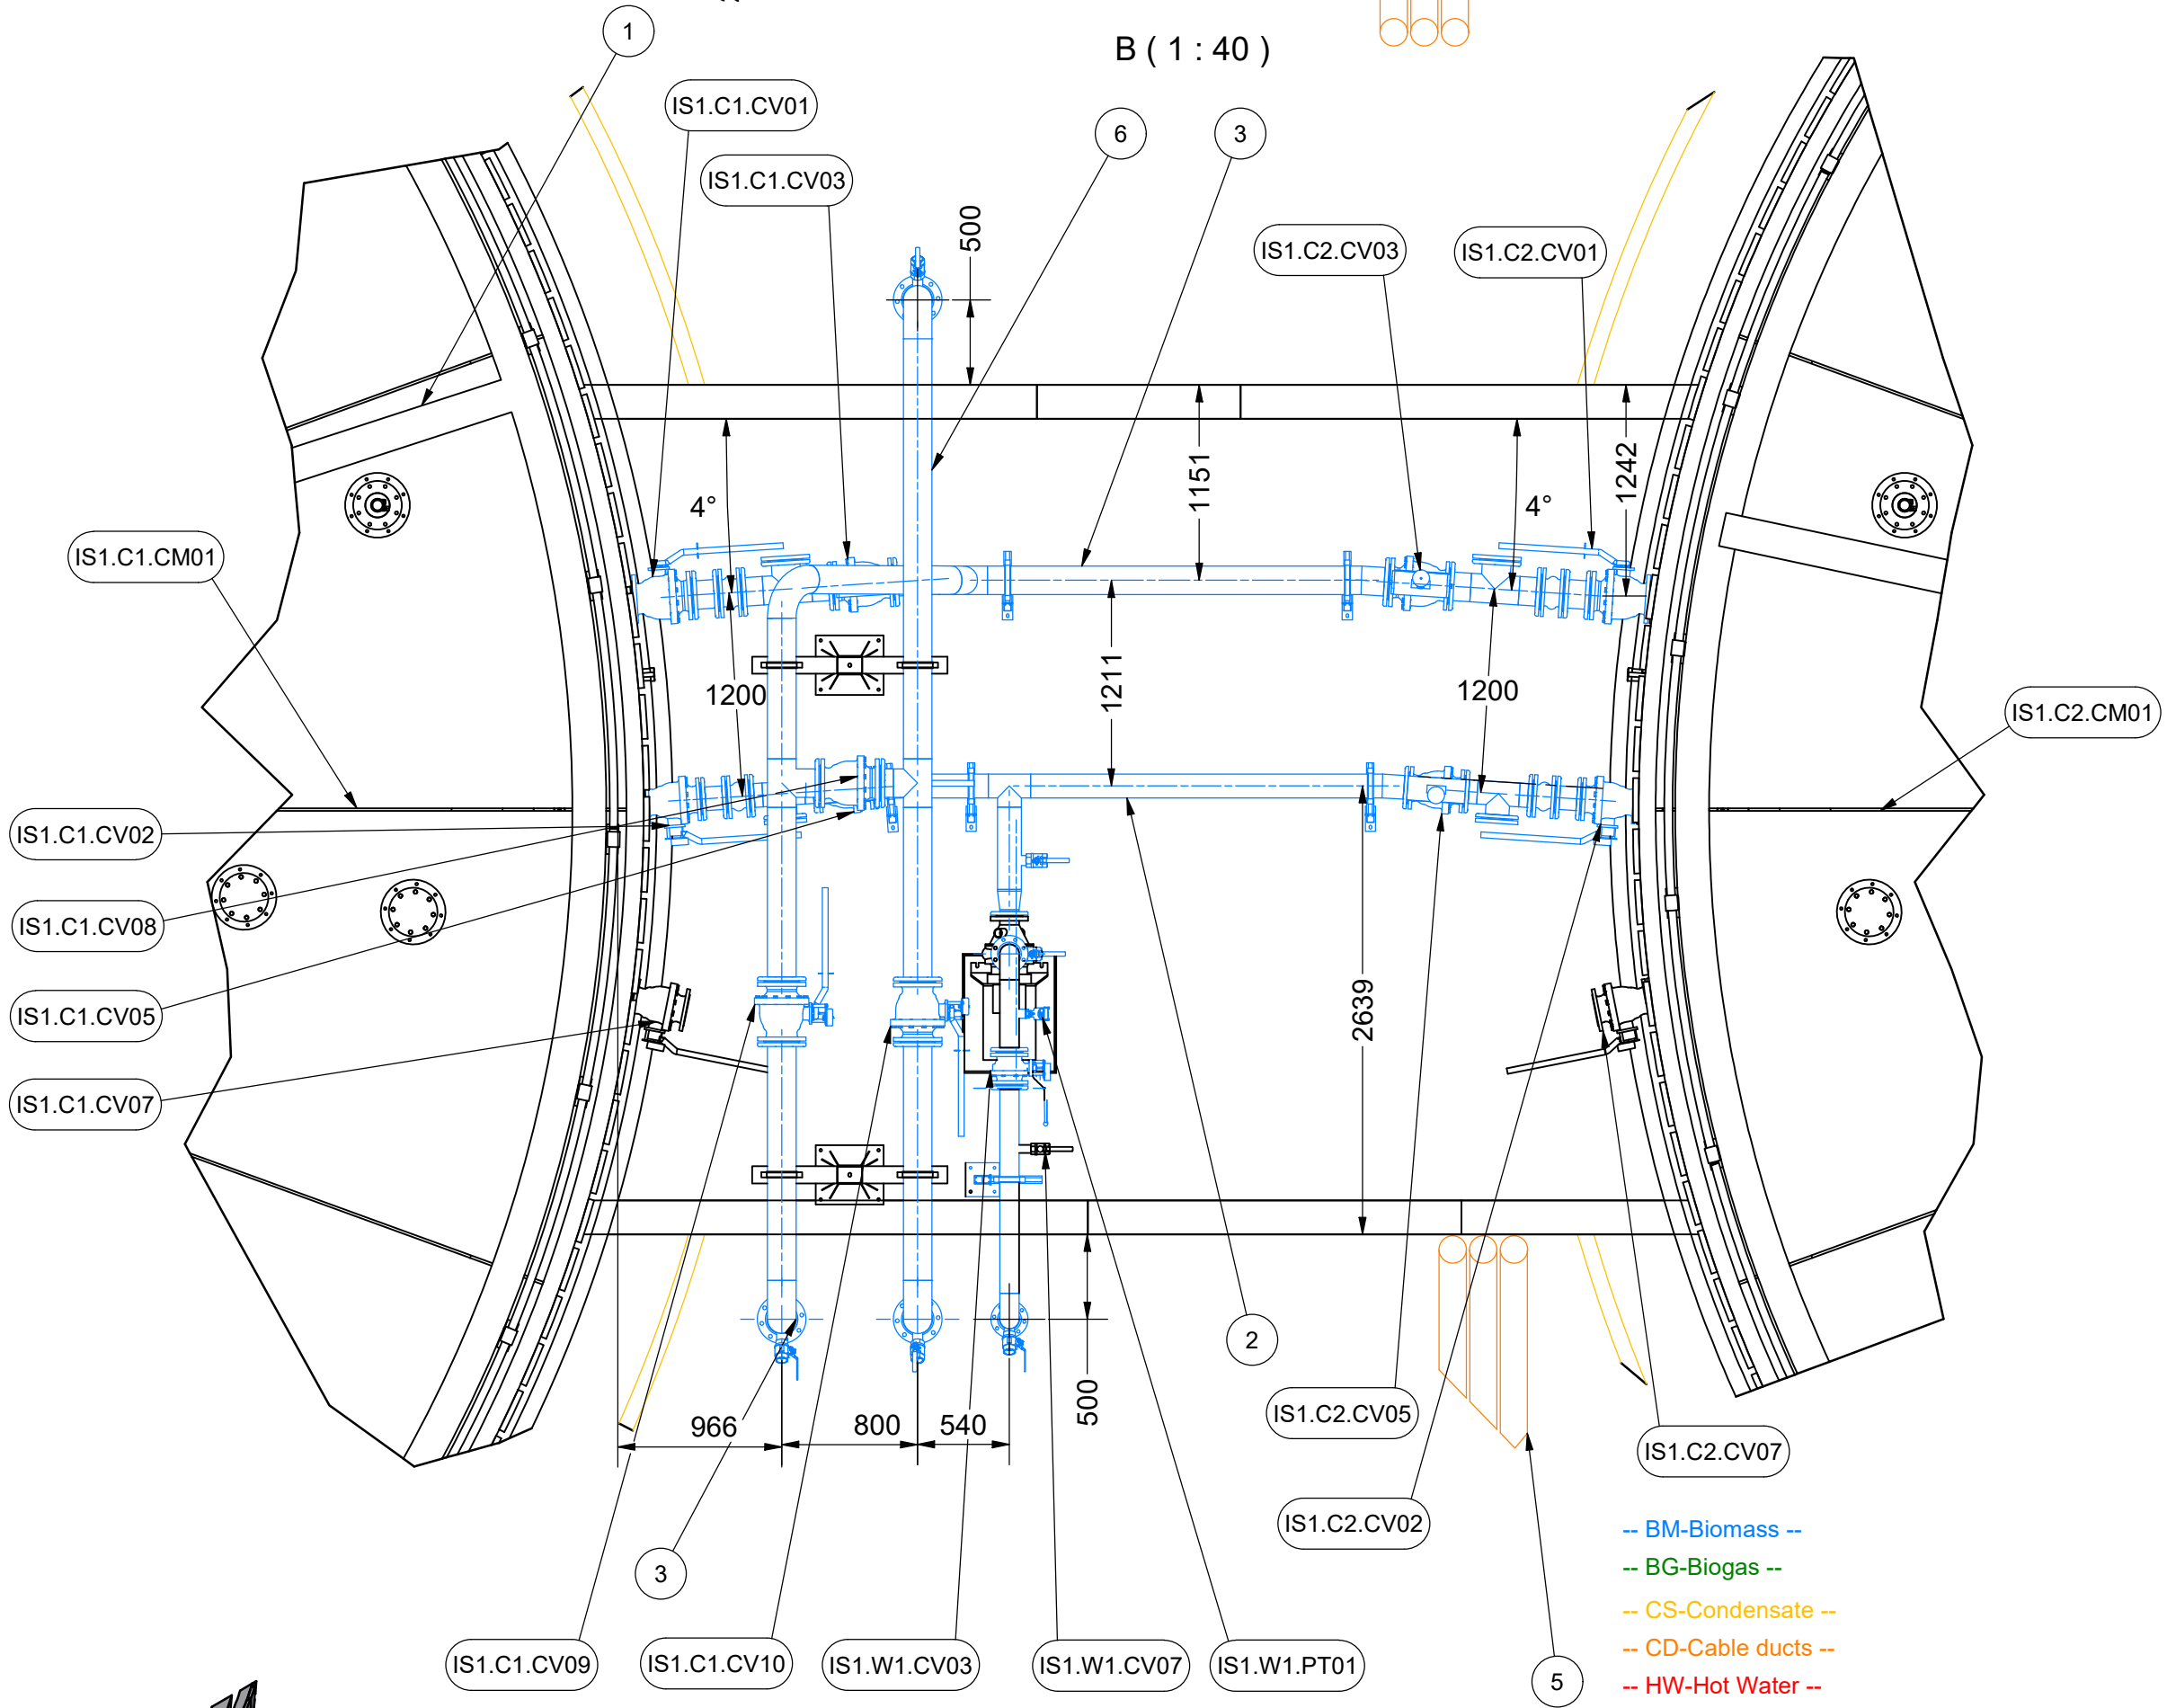

B (1 : 40)

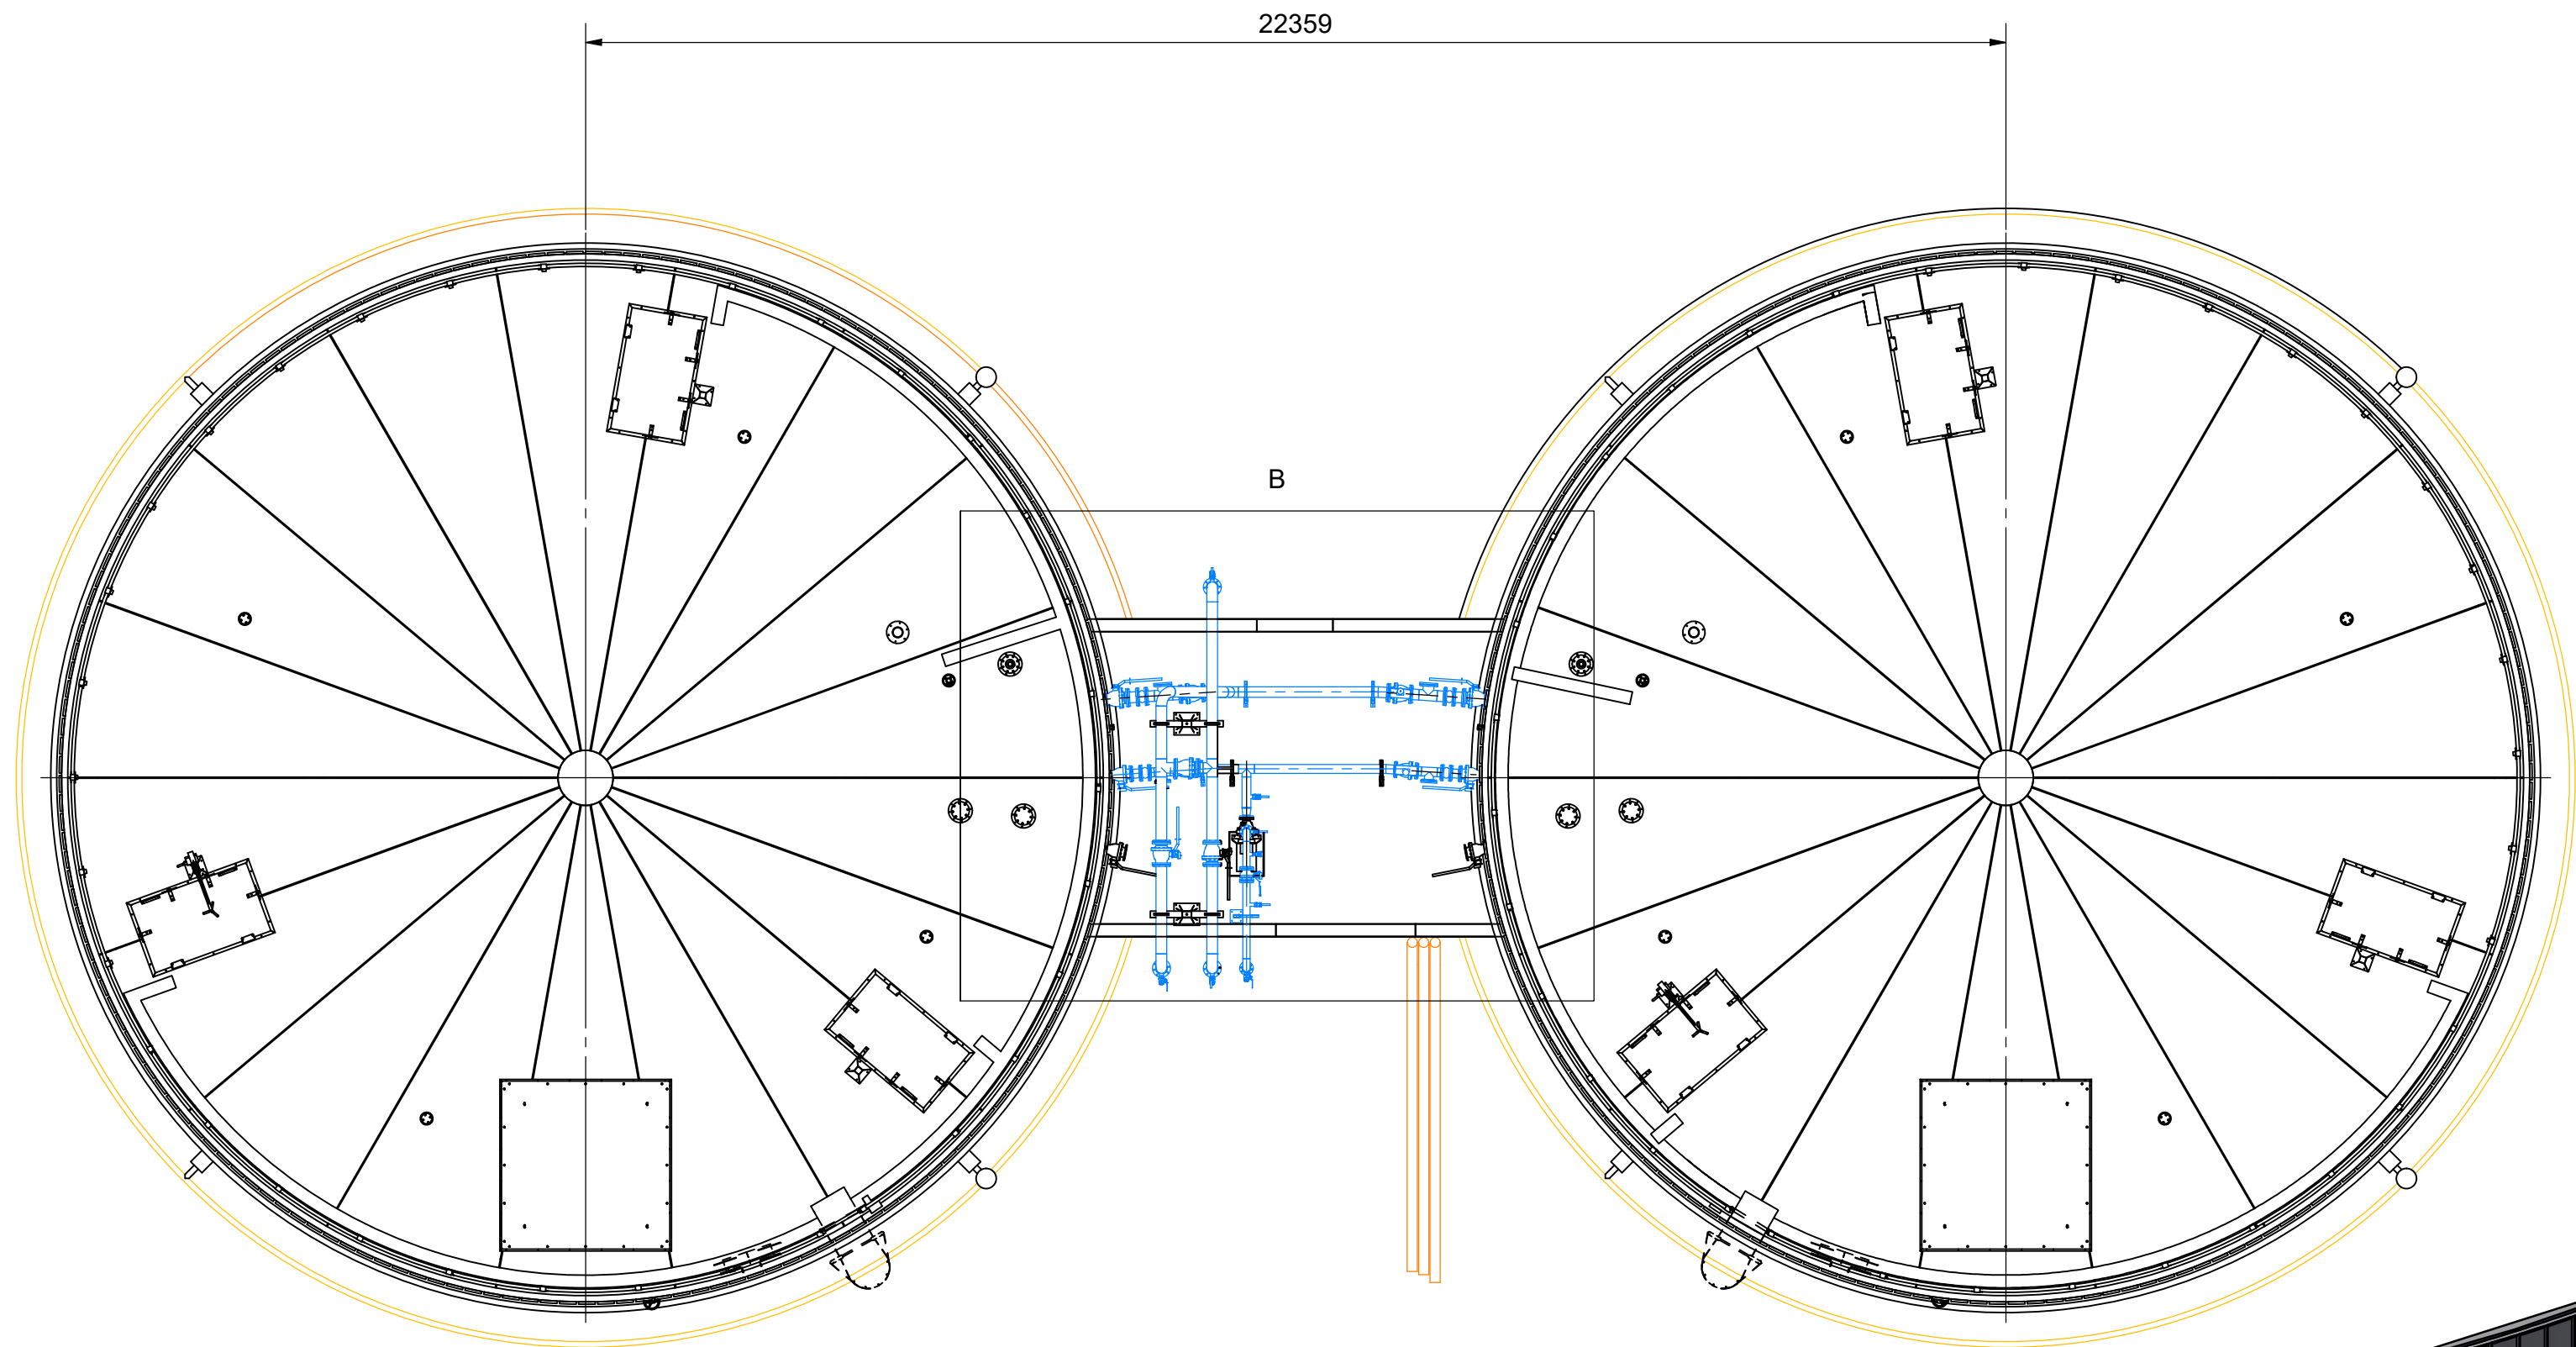


-- BM-Biomass --
-- BG-Biogas --
-- CS-Condensate --
-- CD-Cable ducts --
-- HW-Hot Water --
-- IC-Iron Chloride --

-- PA-Pressurized Air --
-- TD-Technical Drainage --
-- TW-Technical water --
-- OD-Odor --

BK - Bottom Level
RK - Rist Level

If nothing else is mentioned
Pipes must be carried up by the nearest possible wall.

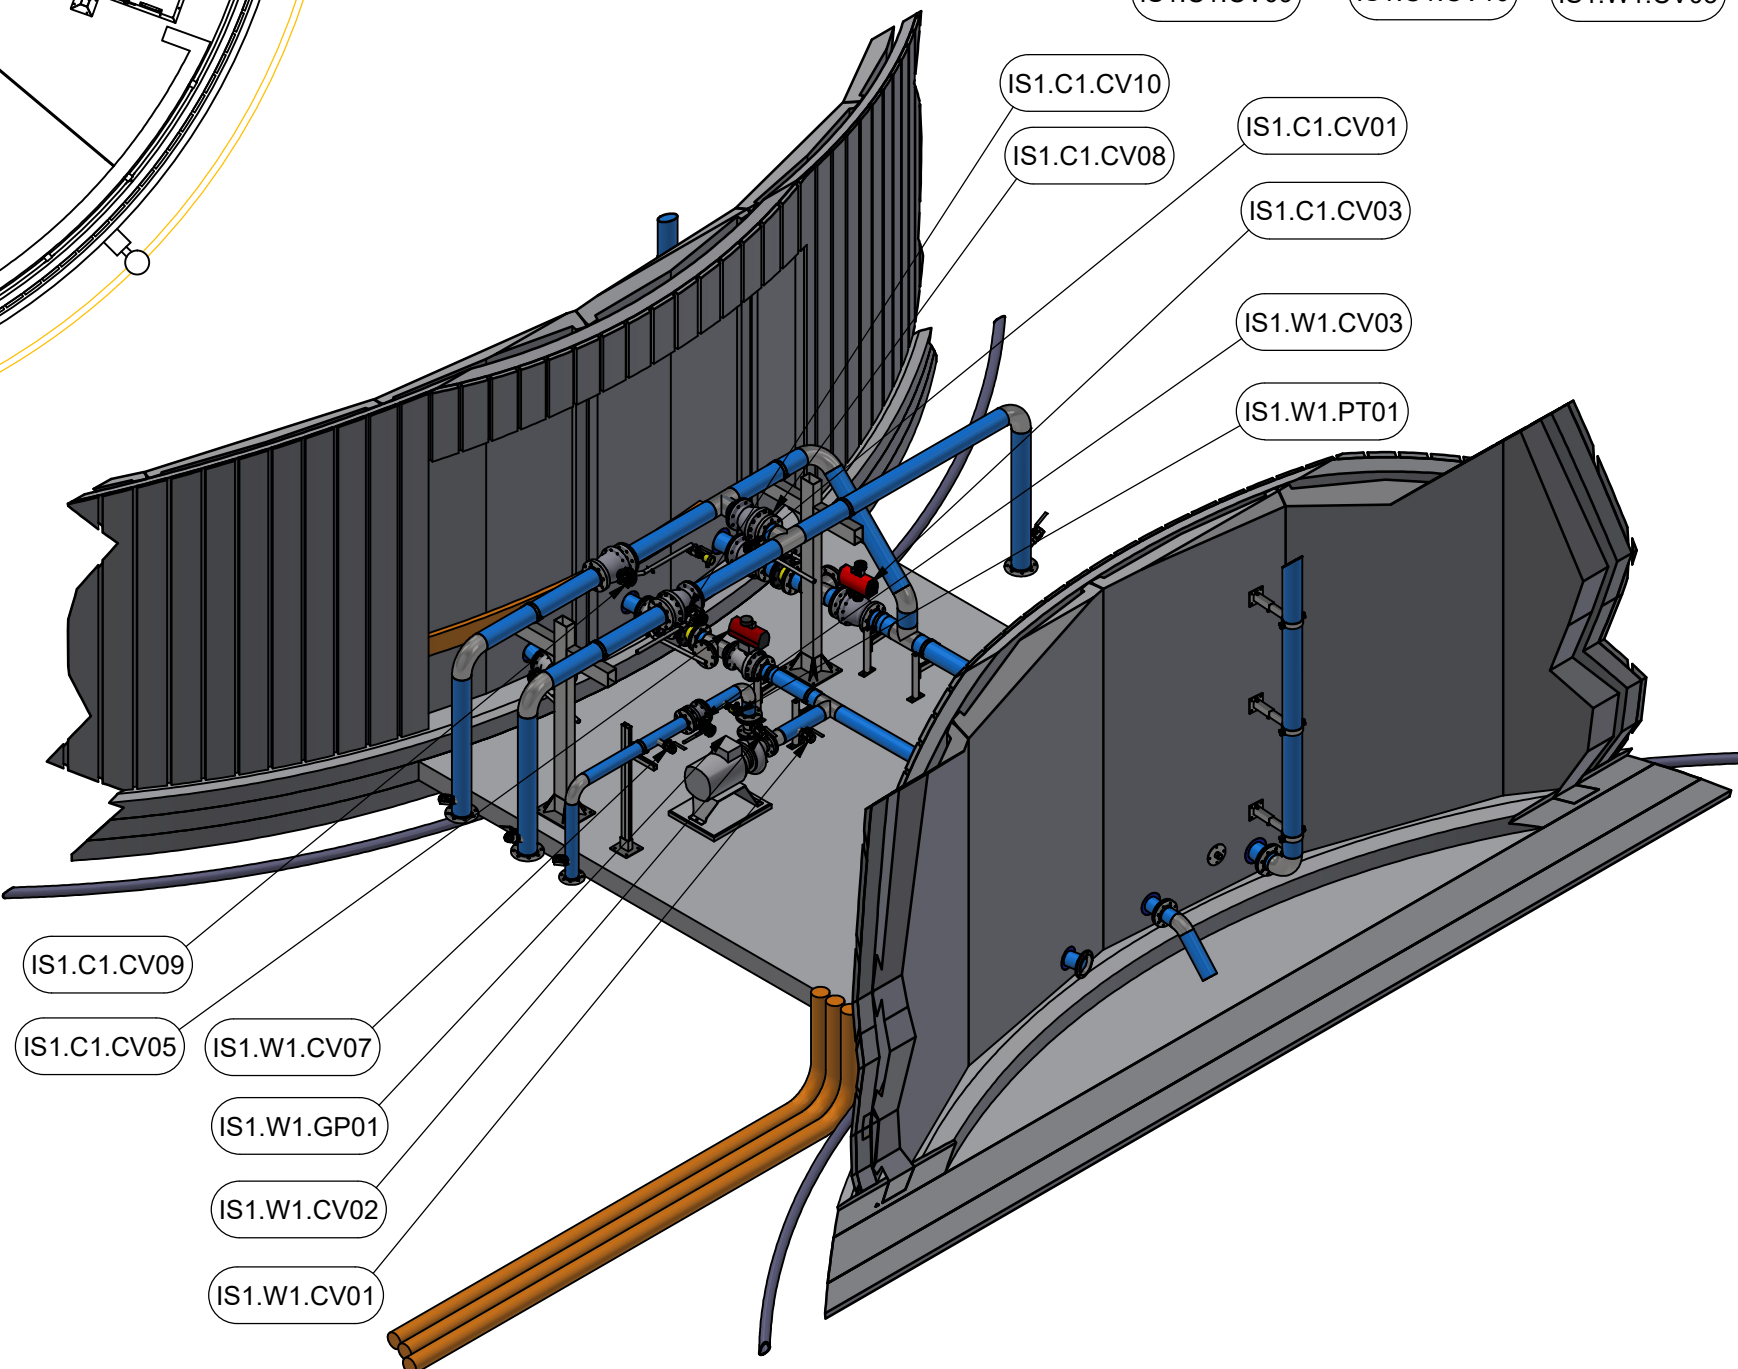

7	2	4003-03-PS28		
6	1	4003-02.1-BM017-02	Bypass Line	
5	1	4003-99-CD001-01-11	Cable Ducts - DVR160,0x12,5 L=18559	PE100
4	1	4003-02.1-BM003-02	Piping from Pump to ground	
3	1	4003-02.1-BM002-01	Distribution Piping to Mixer tanks	
2	1	4003-02.1-BM003-01	Distribution Piping from Mixer tanks to Pump	
1	1	4003-02.1-E01	Equipment Layout	
Pos.	Qty	Part No.	Description	Material

Parts List

Denne tegning må ikke overføres til, kopieres eller udrykkes af uvedkom-
mende uden vor tilladelse.

This drawing remains our property.
Its use without due authority is for-
bidden, and will lead to legal action.

Diese Zeichnung ist unser Eigentum.
Unbefugte Benutzung ist verboten
und wird gerichtlich verfolgt.

Ce dessin est notre propriété. Toute
utilisation indue est interdite sous
peine de poursuites légales.

Bigadan A/S
Dronning Sophies Allé 7A
DK - 8660 Skanderborg
Tel. : +45 86 57 90 90
www.bigadan.com

Drawing State
Released
Scale 1 : 100
Size A1 (594x841 mm)
Dwg No 4003-02.1-A01
Rev -

4003 - Nurmo Bioenergia
Area 02
Mixing Tanks 1 & 3

Date : 29-10-2024
Sheet : 1 of 1