


A-A (1 : 100)

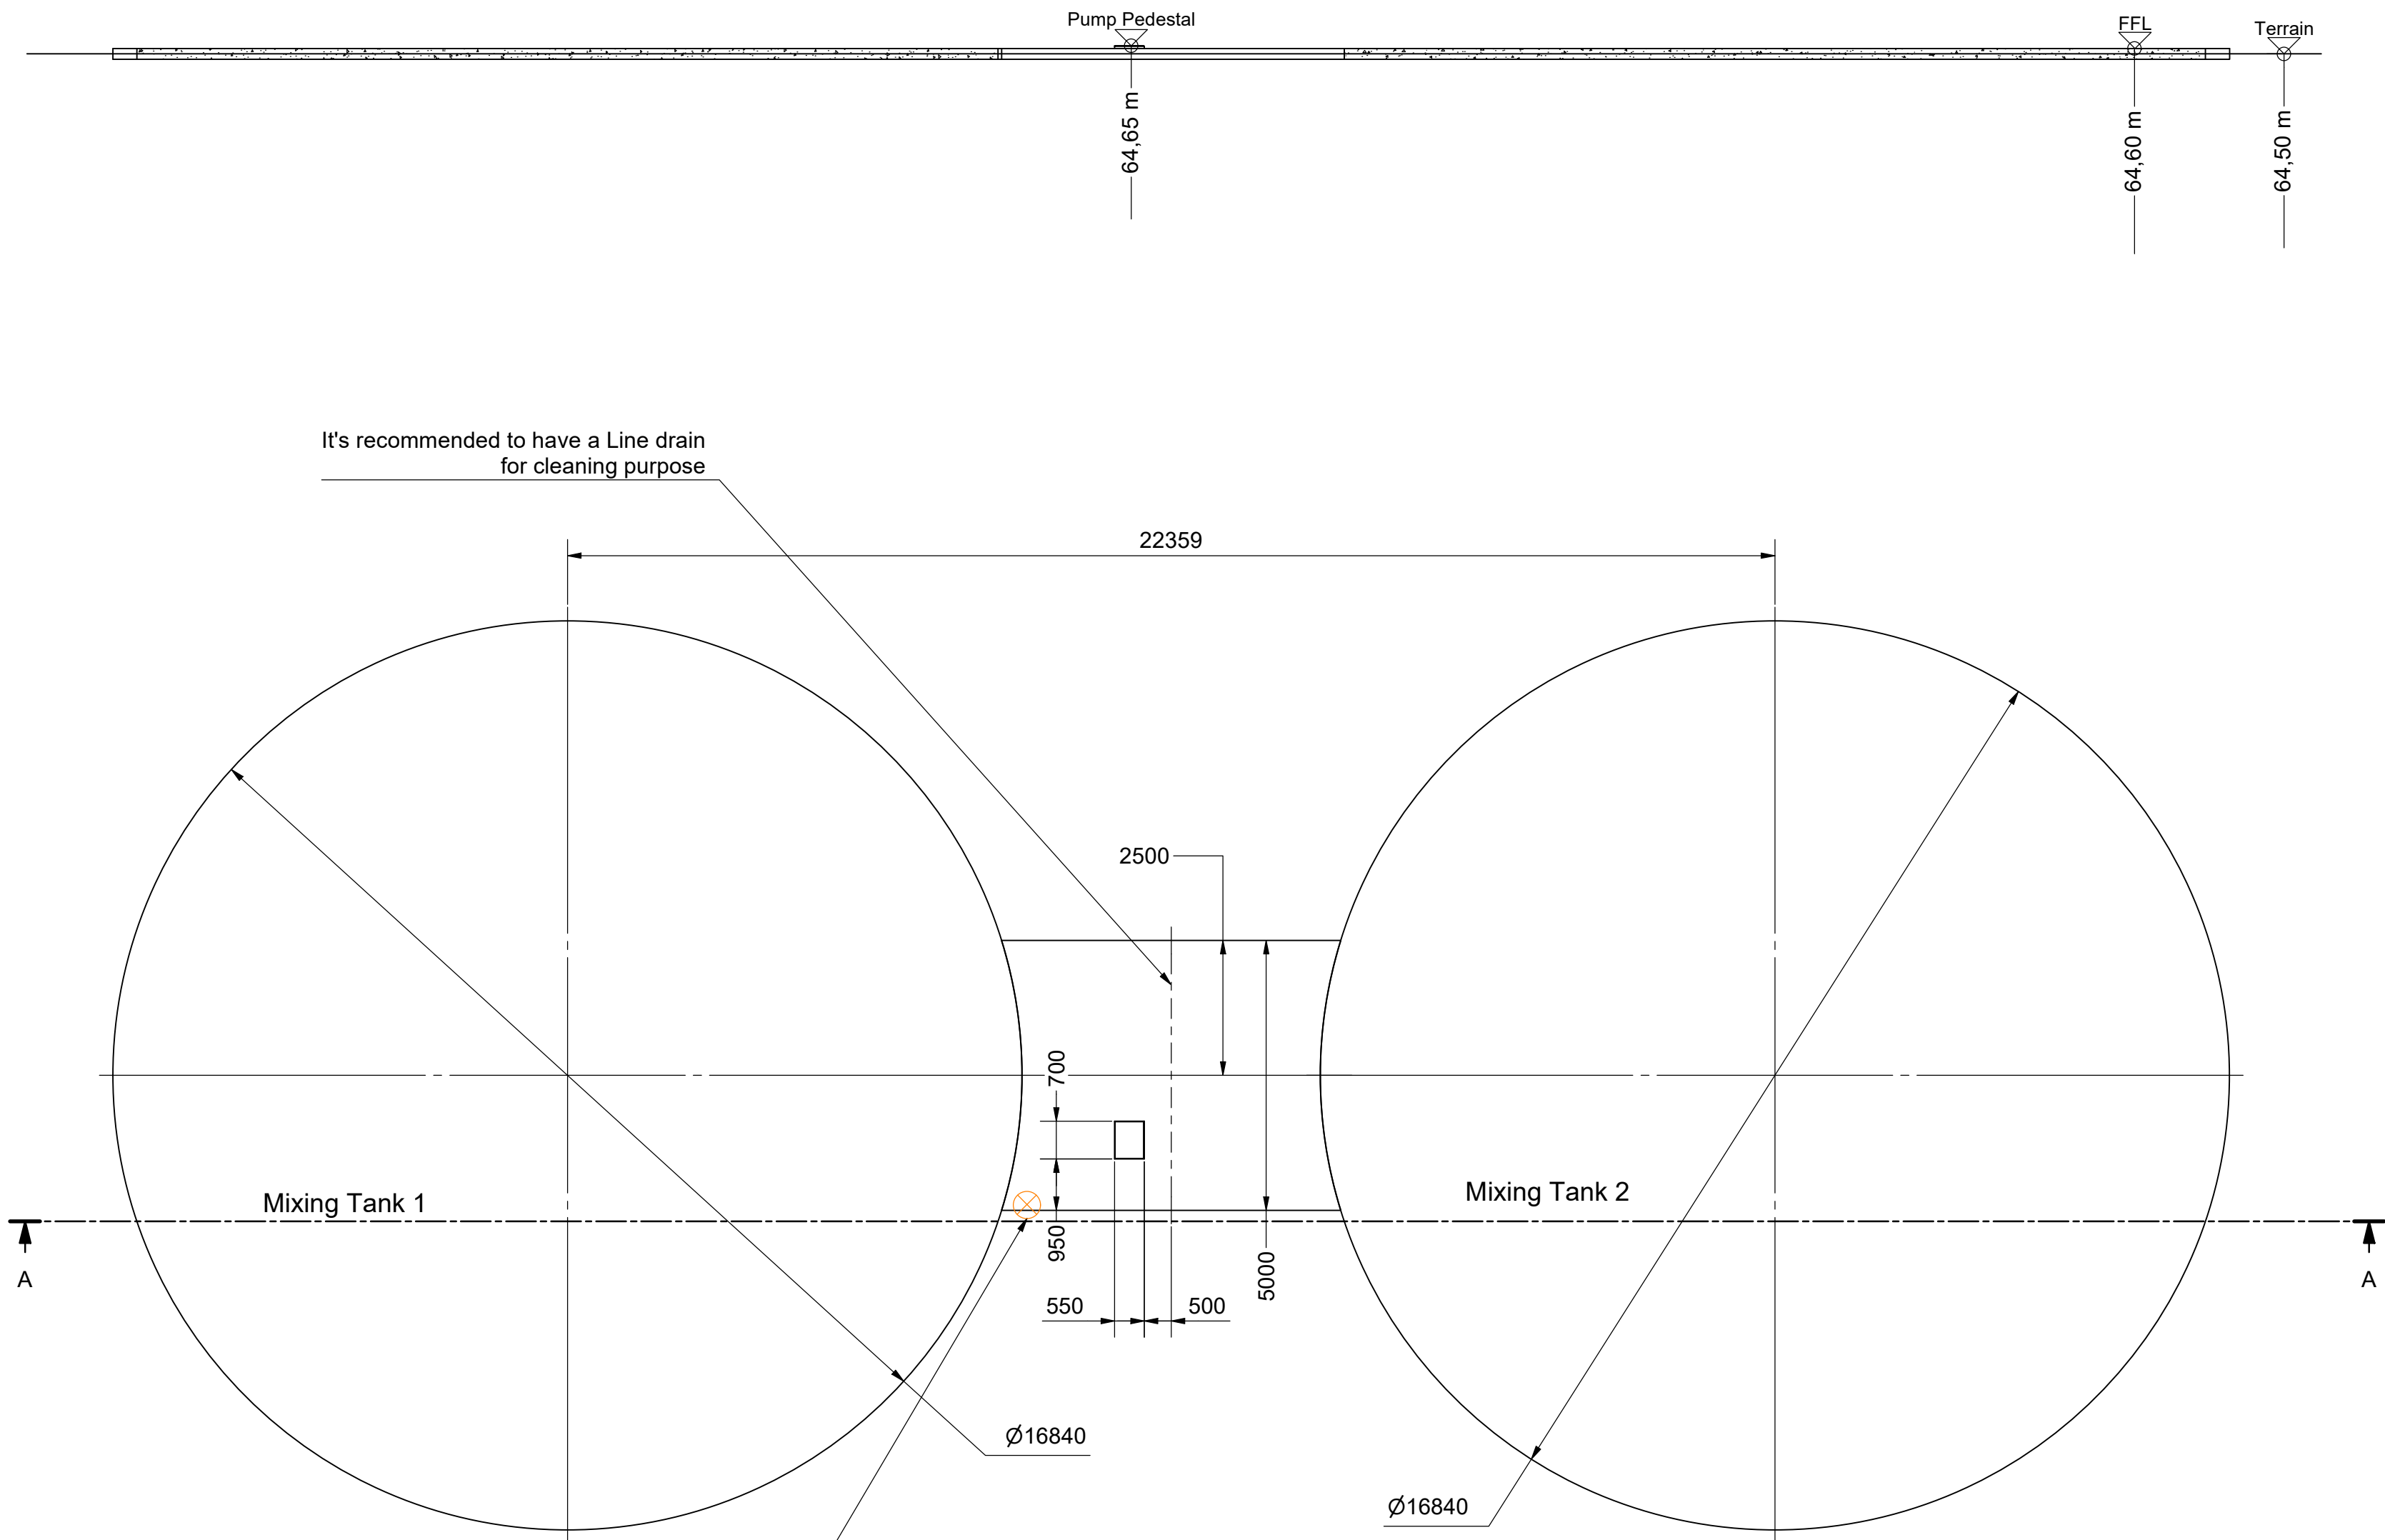

A	25-02-2025	JLH	Level View added	JLH
-	25-09-2024	jch	First Release	JCH
Rev	Date	Rev By	Description	Approved
Revision History				
Denne tegning må ikke overlades til, kopieres eller udnyttes af uvedkom-mende uden vor tilladelse.		This drawing remains our property. Its use without due authority is for-bidden, and will lead to legal action.		Diese Zeichnung ist unser Eigentum. Unbefugte Benutzung ist verboten und wird gerichtlich verfolgt.
				Ce dessin est notre propriété. Toute utilisation indue est interdité sous peine de poursuites légales.
Bigadan A/S Dronning Sophies Allé 7A DK - 8660 Skanderborg Tel. : +45 86 57 90 90 www.bigadan.com			Drawing State Released	
4003 - Nurmo Bioenergia			Scale 1 : 100	
Area 02 - Mixing Tank Area			Size A2 (420x594 mm)	
Foundation Layout			Dwg No 4003-02.1-F01	Rev A
			Date : 25-09-2024	Sheet : 1 of 1

FFL = Finish Floor Level