

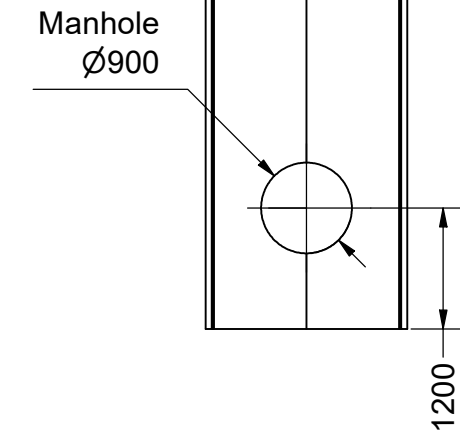
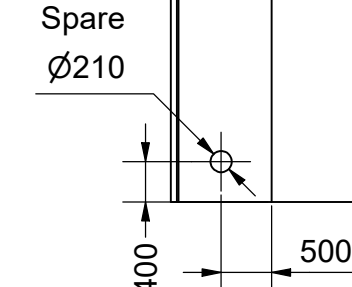
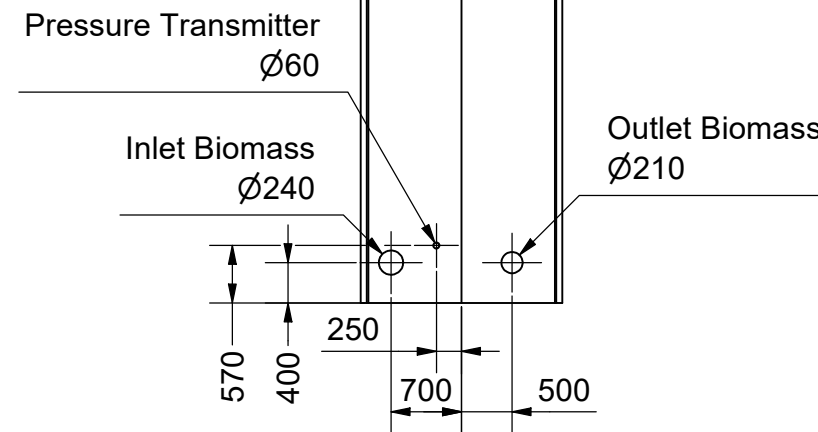
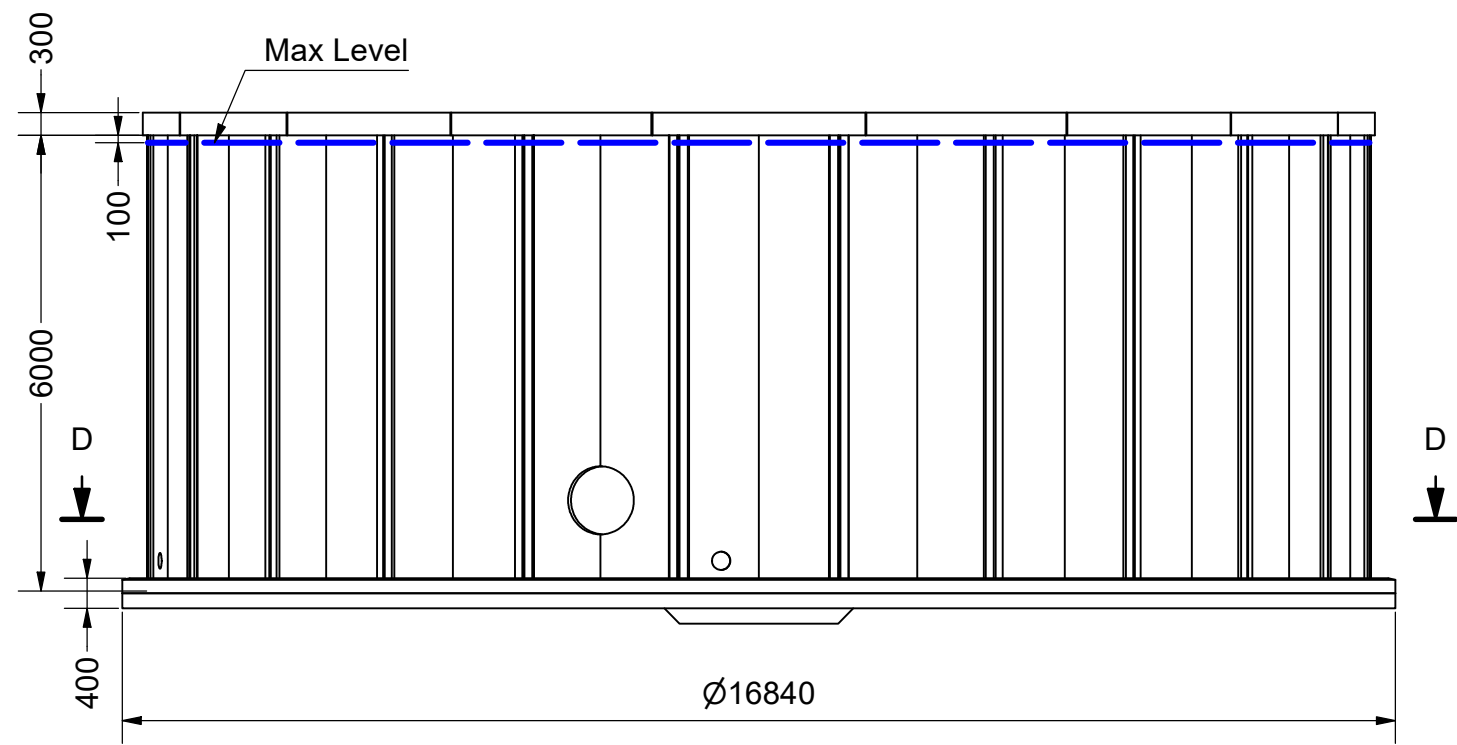
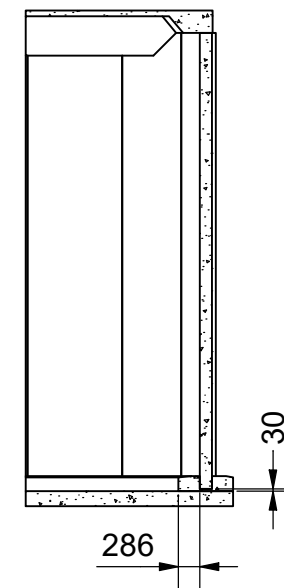
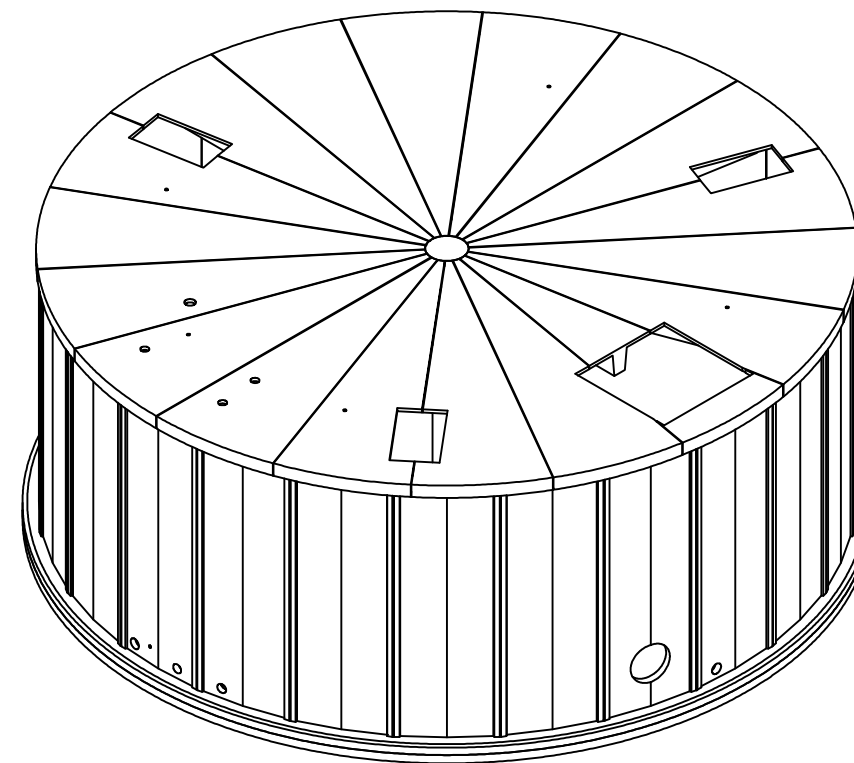


C-C (1 : 100)

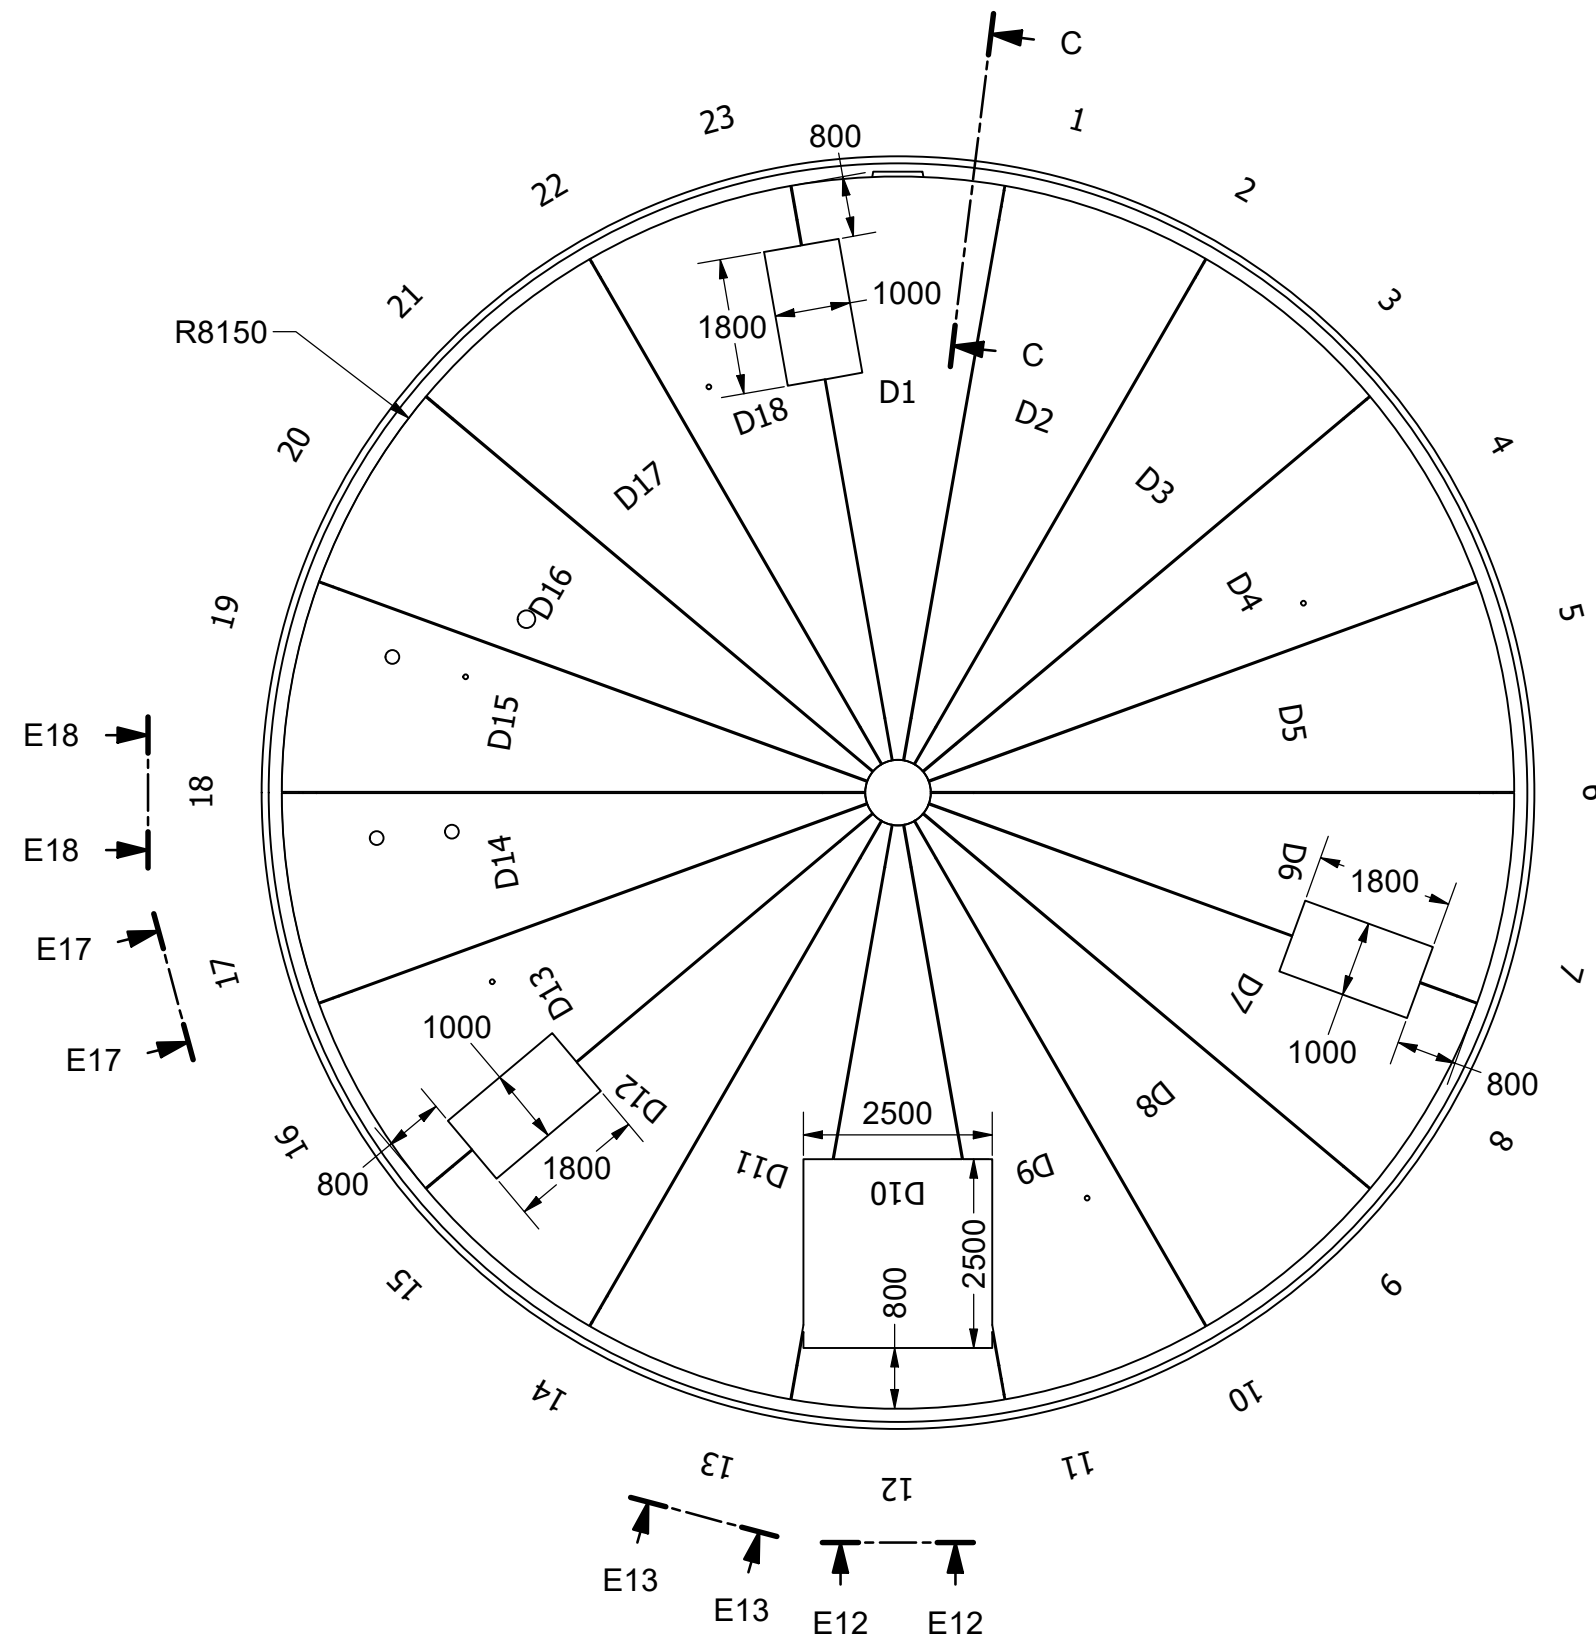

D-D (1 : 150)

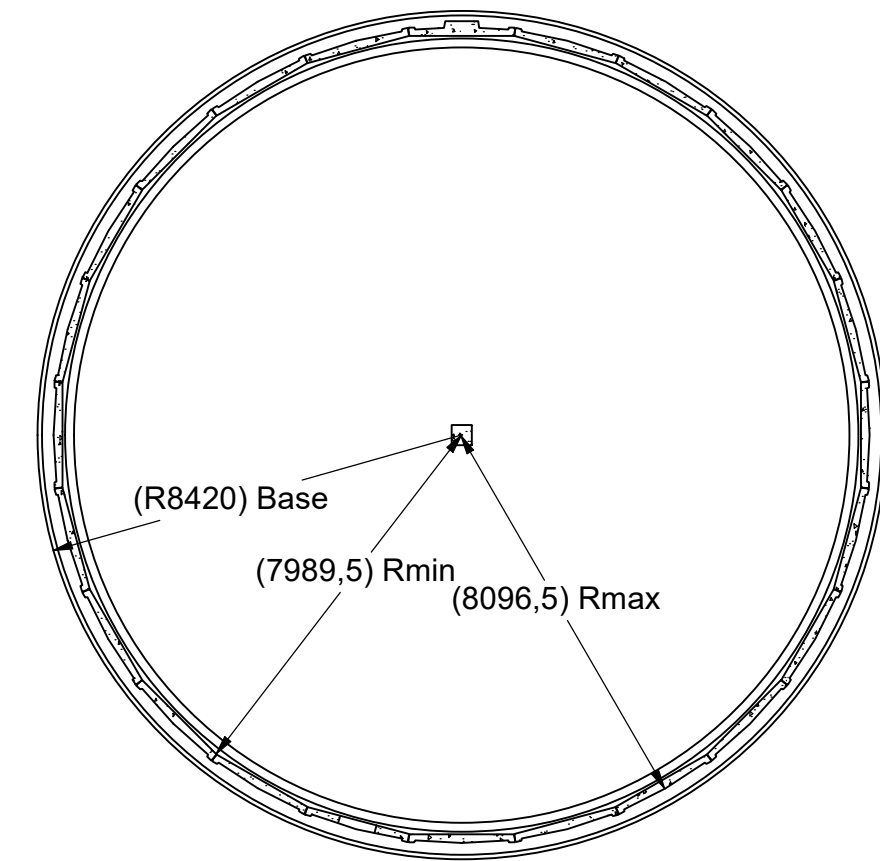


Note: All holes under Ø100 must be drilled on site

B	19-09-2024	JCH	Added and changed hole sizes in concrete elements	JCH
A	09-09-2024	jsc	Added measure of holes	JLH
-	06-09-2024	jsc	First release	JLH
Rev	Date	Rev By	Description	Approved

Revision History

Denne tegning må ikke overlades til, kopieres eller udnyttes af uvedkommende uden vor tilladelse.	This drawing remains our property. Its use without due authority is forbidden, and will lead to legal action.	Diese Zeichnung ist unser Eigentum. Unbefugte Benutzung ist verboten und wird gerichtlich verfolgt.	Ce dessin est notre propriété. Toute utilisation indue est interdite sous peine de poursuites légales.
---	---	---	--

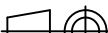 Bigadan A/S Vroldvej 168 DK - 8660 Skanderborg Tel. : +45 86 57 90 90 www.bigadan.com	Drawing State		
	Scale 1 : 100		
	Size A2 (420x594 mm)		
	Dwg No 4003-613-D02		
4003 - Nurmo Bioenergia Area 02 - Mixing Area Mixing Tank 2		Rev A	
Date : 31-08-2023		Sheet : 1 of 1	