

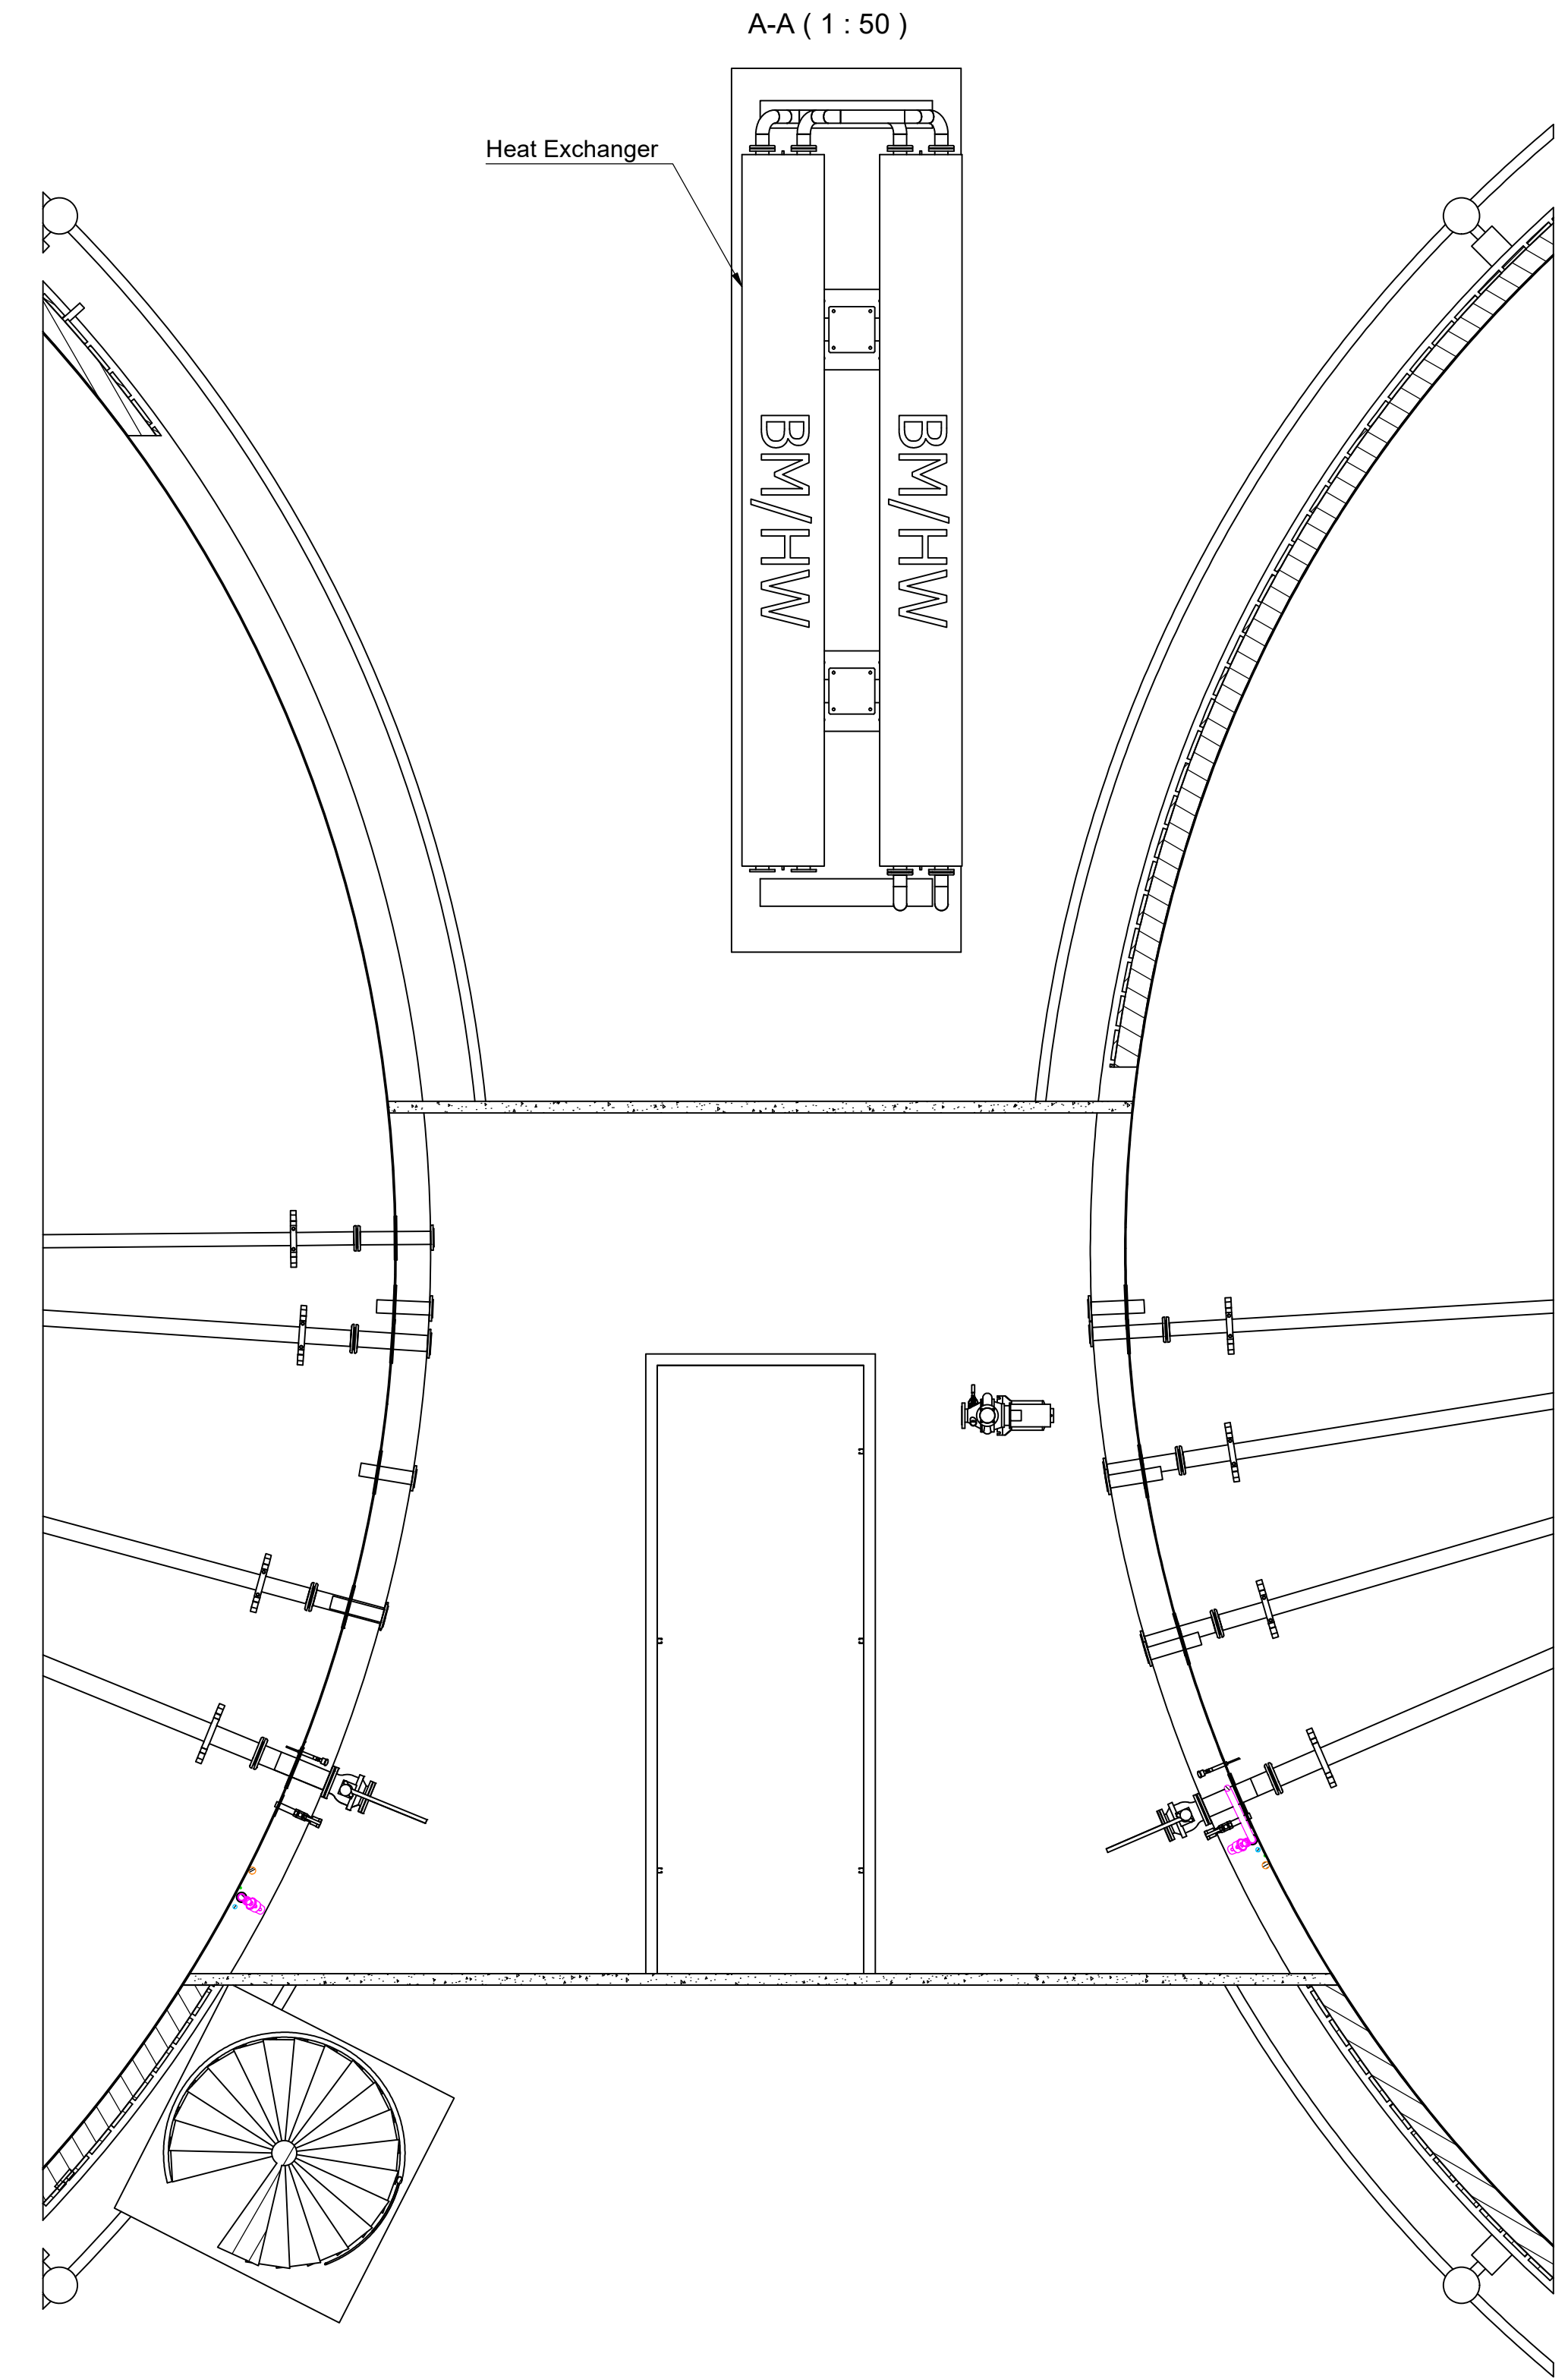


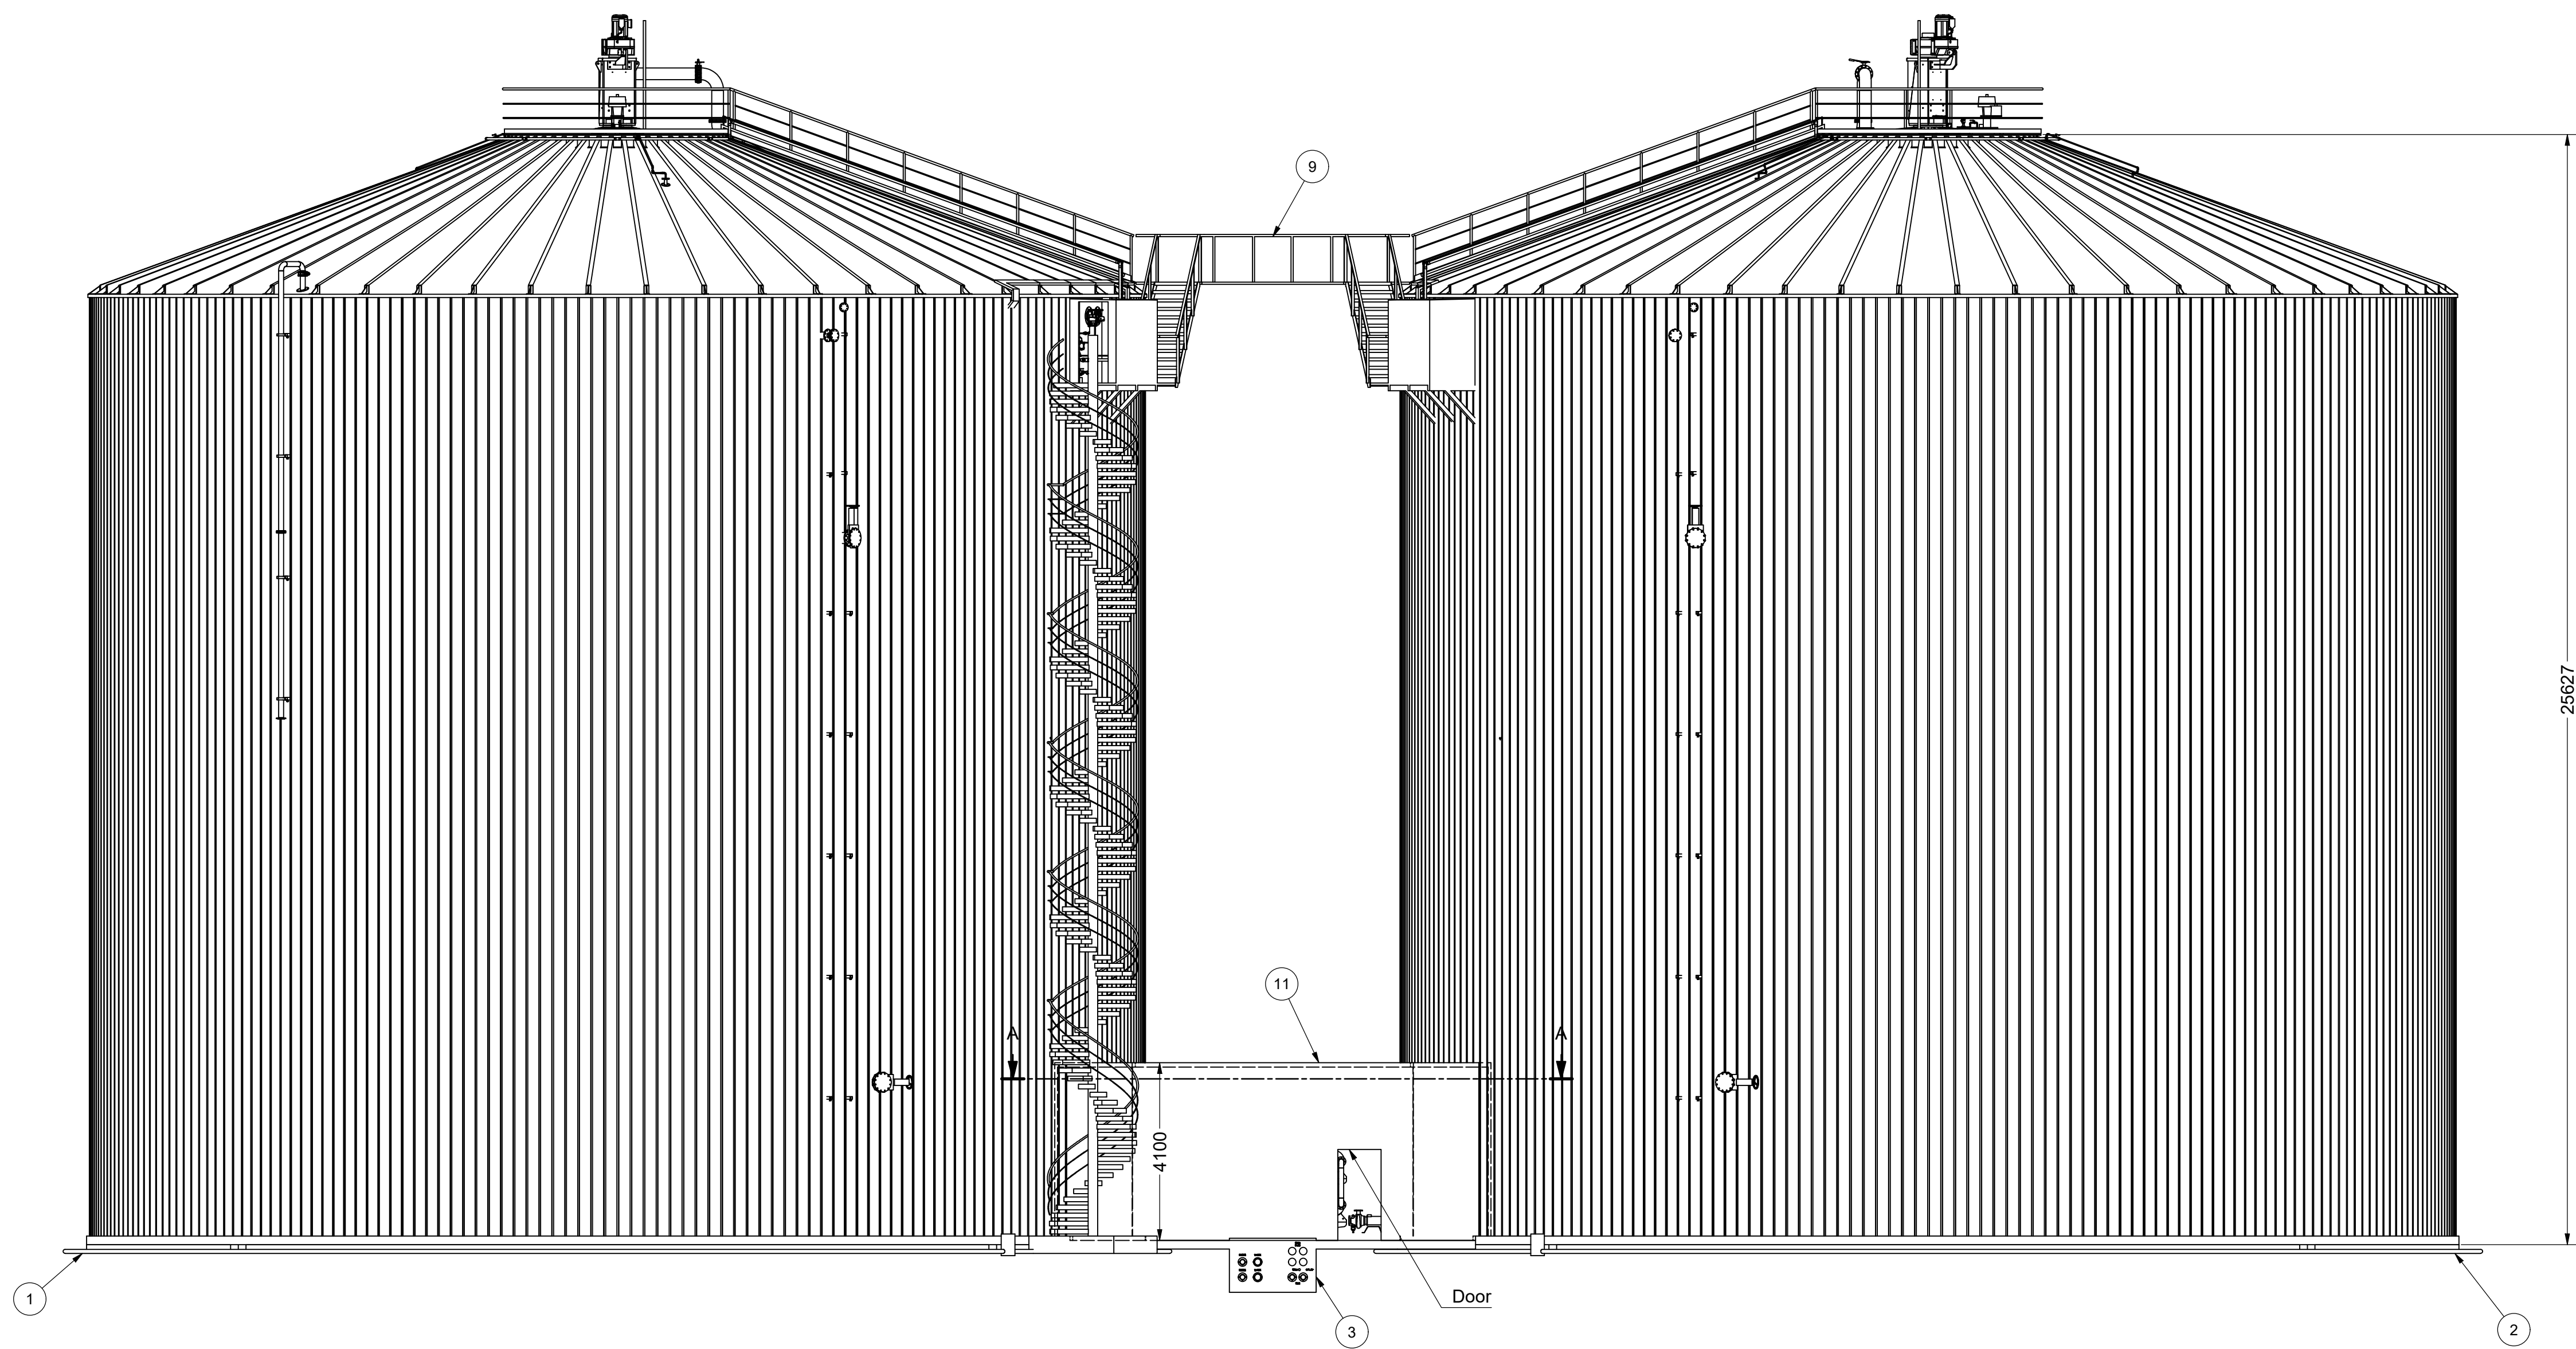

Mixing Tank 2 - 1197m³
Ø16,3mx h6,0m

Area 04

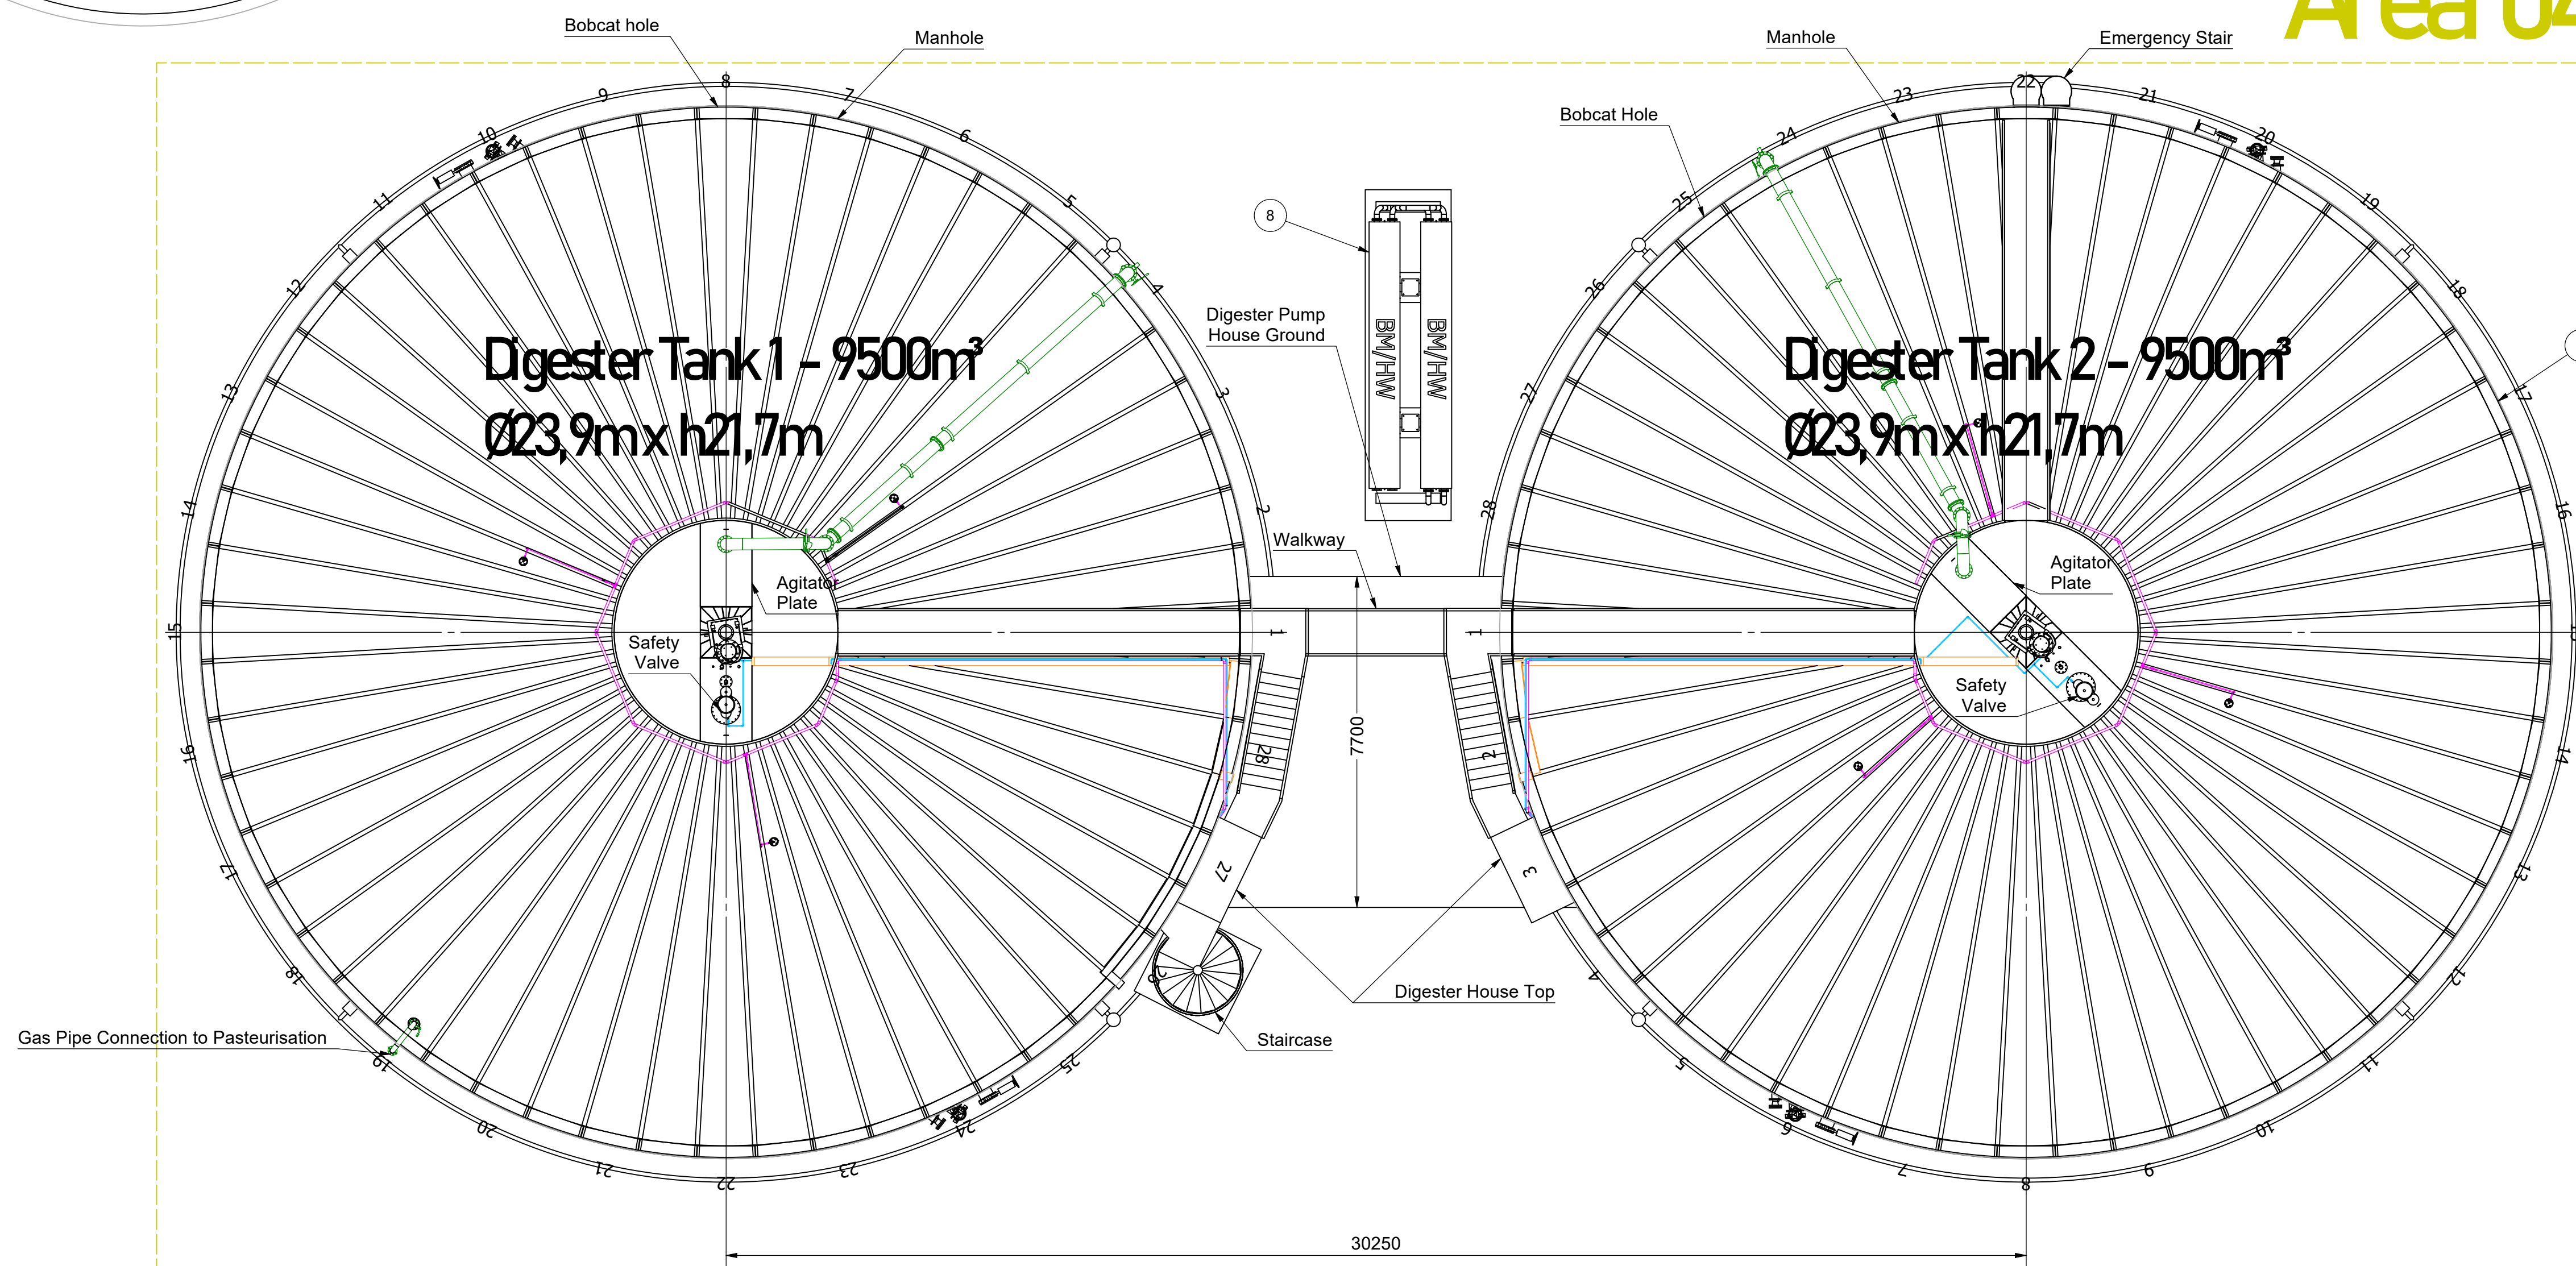

Post Digester - 3188m³
Ø26,0mx h6,0m

16	1	4003-04.1-PS10	Hilti Assembly		
15	1	0000-701-001	Ball valve - DN50 - manual - Valtor V-106		Stainless Steel
14	1	4003-04.1-PS06	Hilti Assembly		
13	3	4003-04.1-PS05	Hilti Assembly		
12	1	0000-700-002	Pump - DN100 - 5,5kW - MPTK-i 80		N/A
11	1	4003-04.1-B01	Digester Pump House Ground		Concrete
10	1	4003-04.1-PS05-01-01	Grid		SS 1.4301 - AISI 304
9	1	4003-04.1-PS01	Walkway		SS 1.4301 - AISI 304
8	1	4003-615-A04	Heat-Exchangers		
7	1	4003-615-A02	Digester 2 - 9500m³		
6	1	4003-615-A01	Digester 1 - 9500m³		
5	1	4003-621-F01	HEX Foundation		Concrete
4	1	4003-615-F03	Staircase Foundation		Concrete
3	1	4003-04.1-F01	Digester House Foundation		Concrete
2	1	4003-615-F02	Digester Foundation		Concrete
1	1	4003-615-F01	Digester Foundation		Concrete

Pos.	Qty	Part No.	Description	Material
Parts List				
Digester Equipment Layout				

Bigadan A/S Dronning Stephanie Allé 7A DK - 8000 Århus C Tel.: +45 86 57 99 90 www.bigadan.com		Drawing Scale 1:100 Size A0 (841x1189 mm)	
4003 - Nurmio Bioenergia Area 04.1 Digester Equipment Layout		Released 4003-04.1-E01 Date: 11-09-2024	