
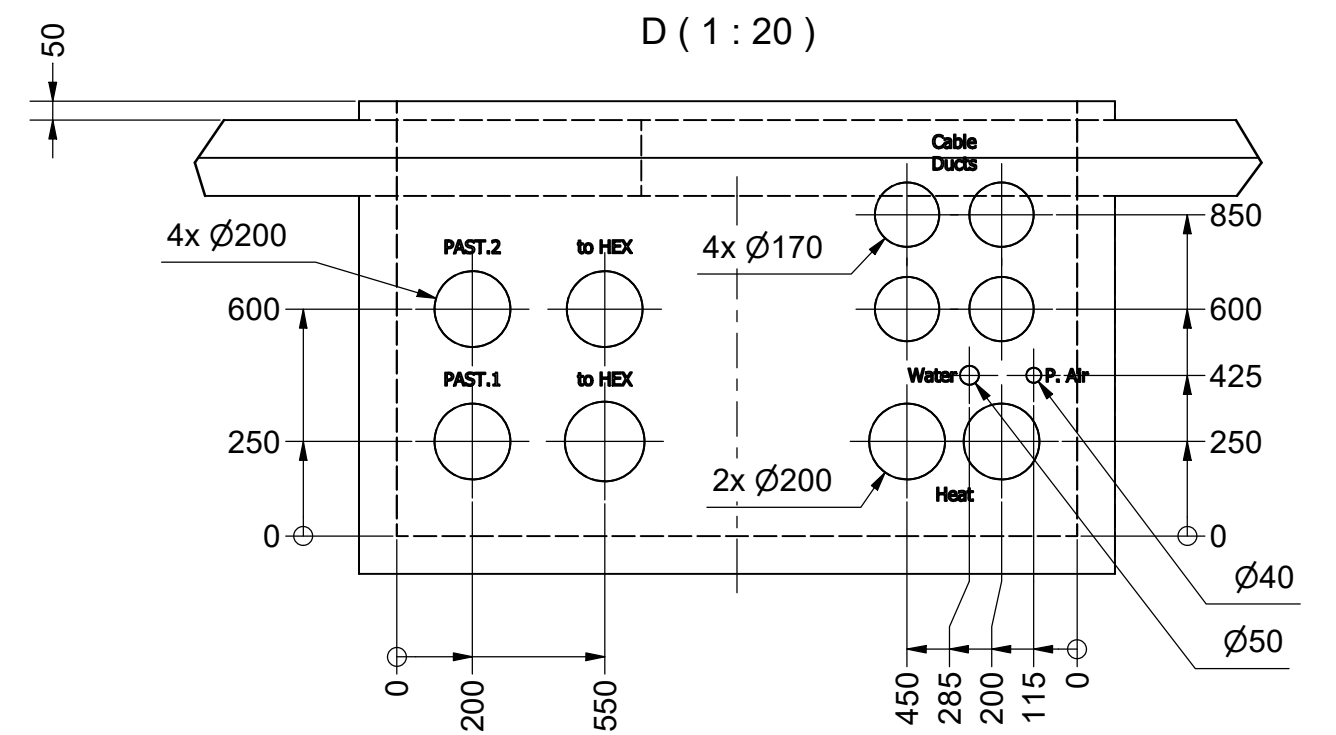
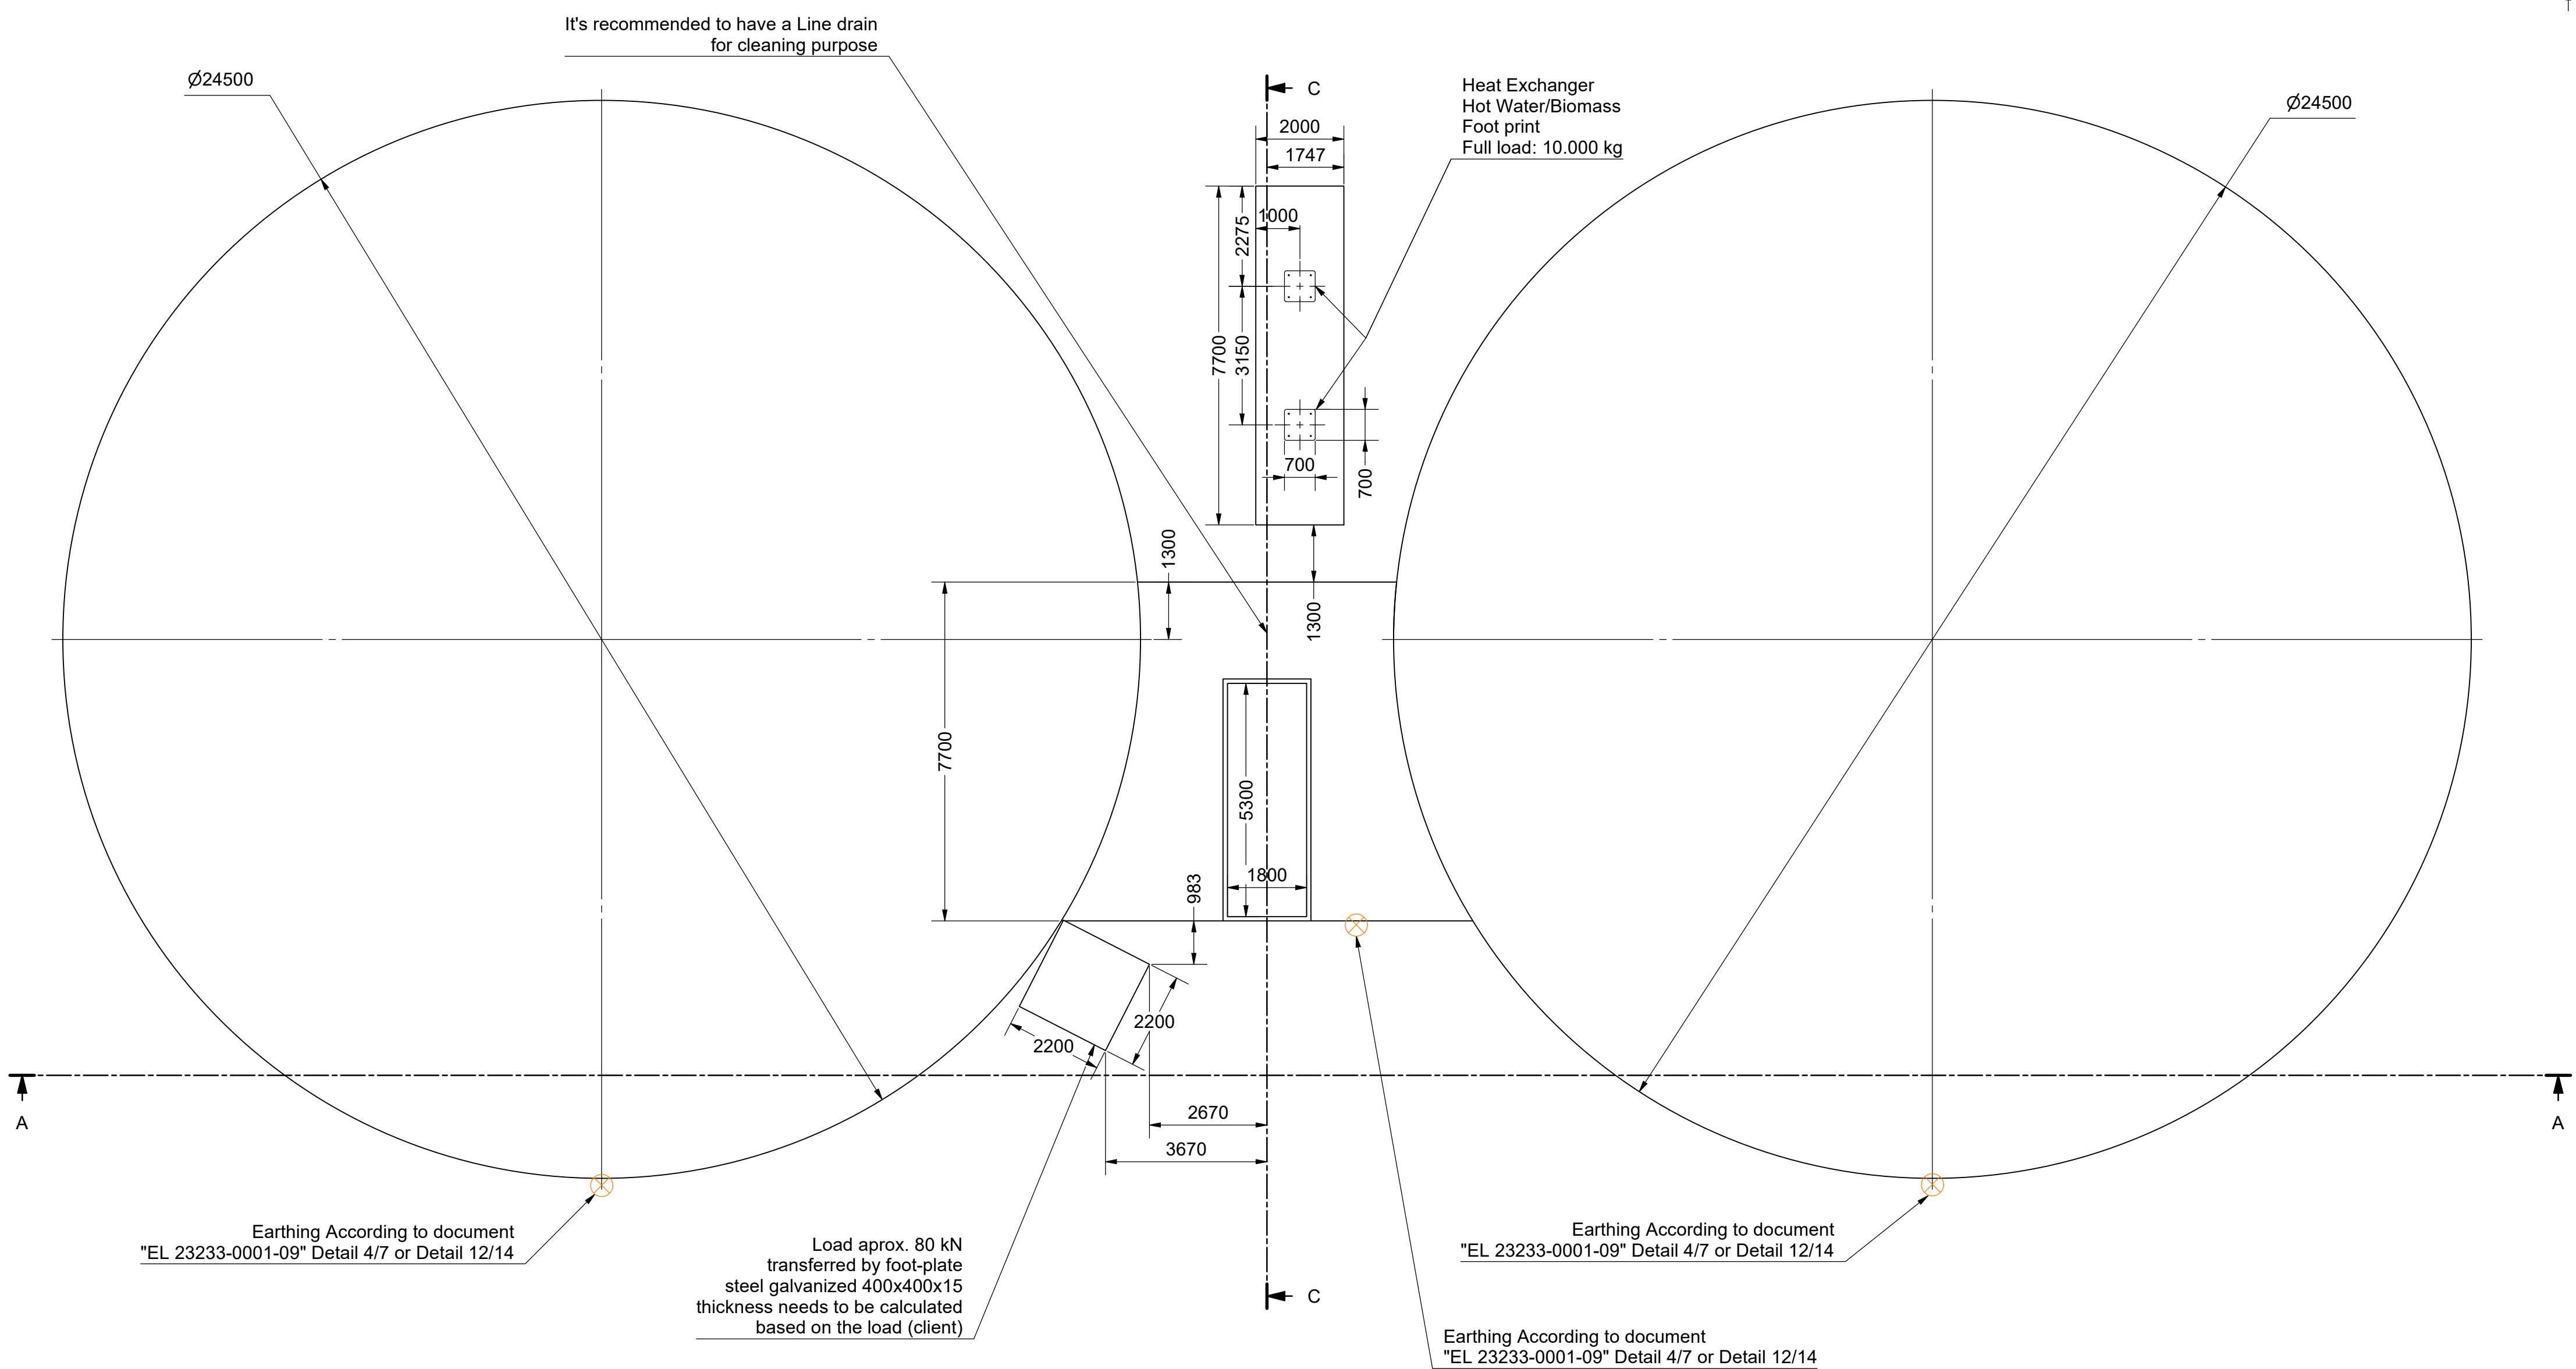


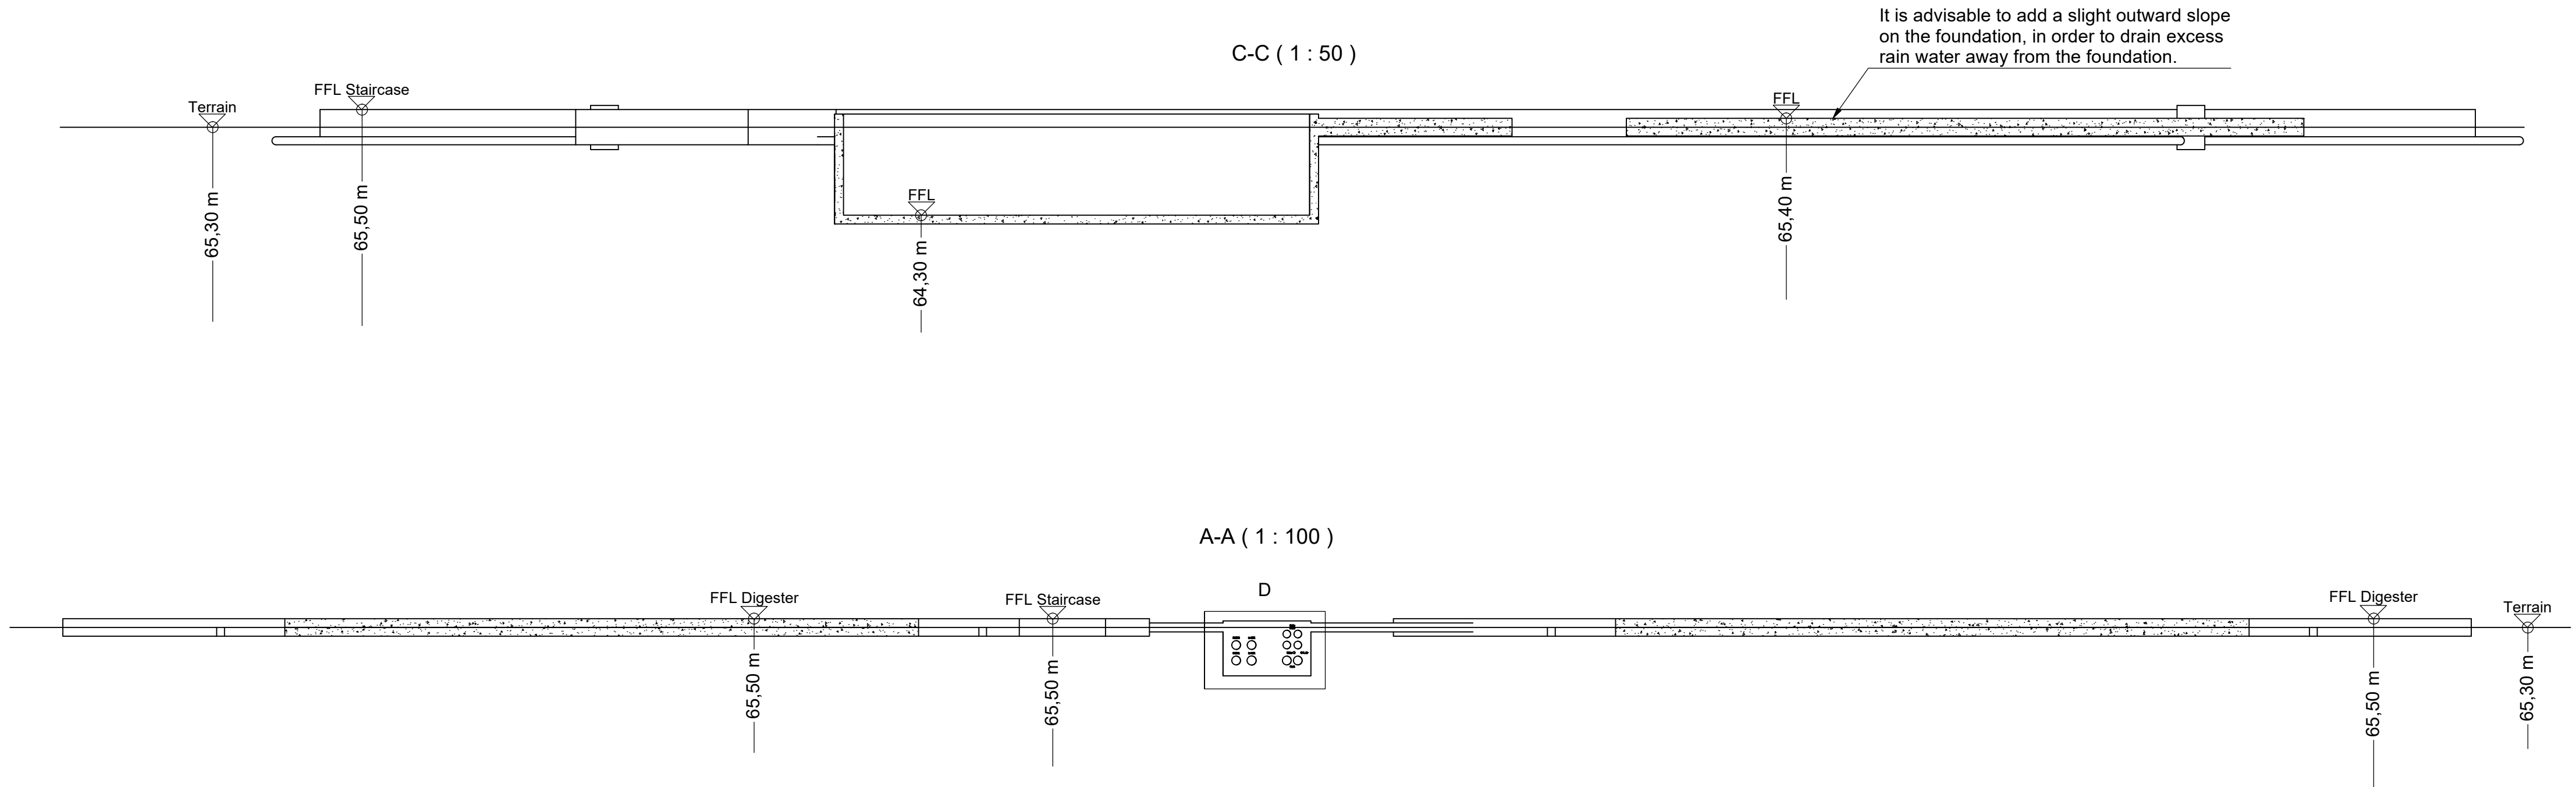

B	25-02-2025	JLH	Level View Added	JLH
A	18-01-2025	JSc	Model updated	JSc
-	01-11-2024	JSc	First Release	JLH
Rev	Date	Rev By	Description	Approved
Revision History				
Denne tegning må ikke overlades til, kopieres eller udrykkes af uvedkom-mende uden vor tilladelse.		This drawing remains our property. Its use without due authority is for-bidden, and will lead to legal action.		Diese Zeichnung ist unser Eigentum. Unbefugte Benutzung ist verboten und wird gerichtlich verfolgt.
Bigadan A/S Dronning Sophies Allé 7A DK - 8660 Skanderborg Tel. : +45 86 57 90 90 www.bigadan.com		Drawing State		Ce dessin est notre propriété. Toute utilisation indue est interdite sous peine de poursuites légales.
4003 - Nurno		Size		Released
Area 04		Dwg No		1 : 100
Foundation Layout		Rev		A1 (594x841 mm)
		Date :		4003-04.1-F01
		Sheet :		B
				1 of 1

FFL = Finish Floor Level