

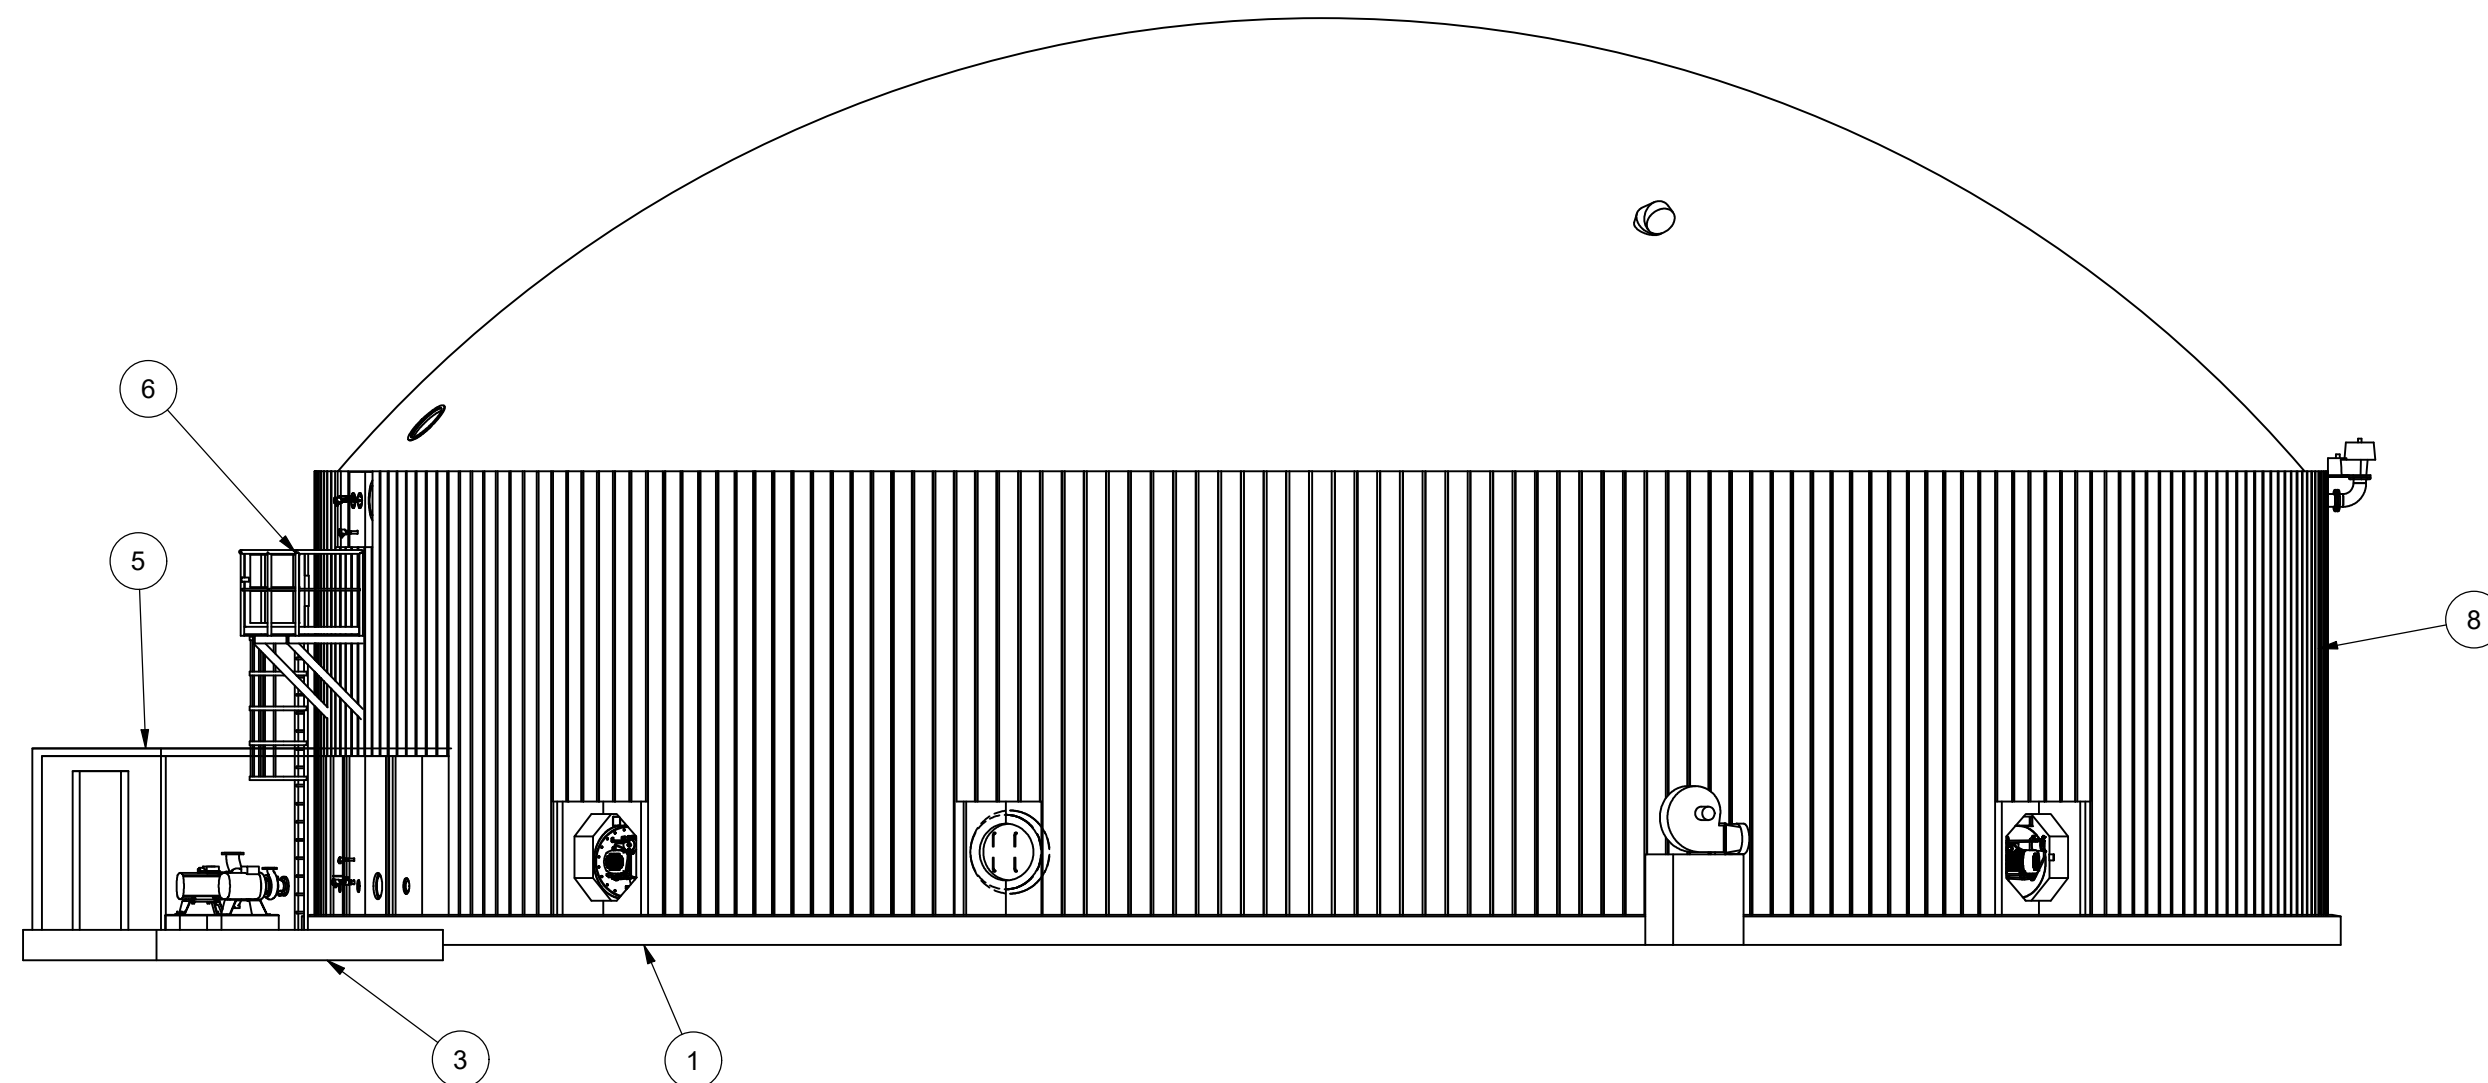
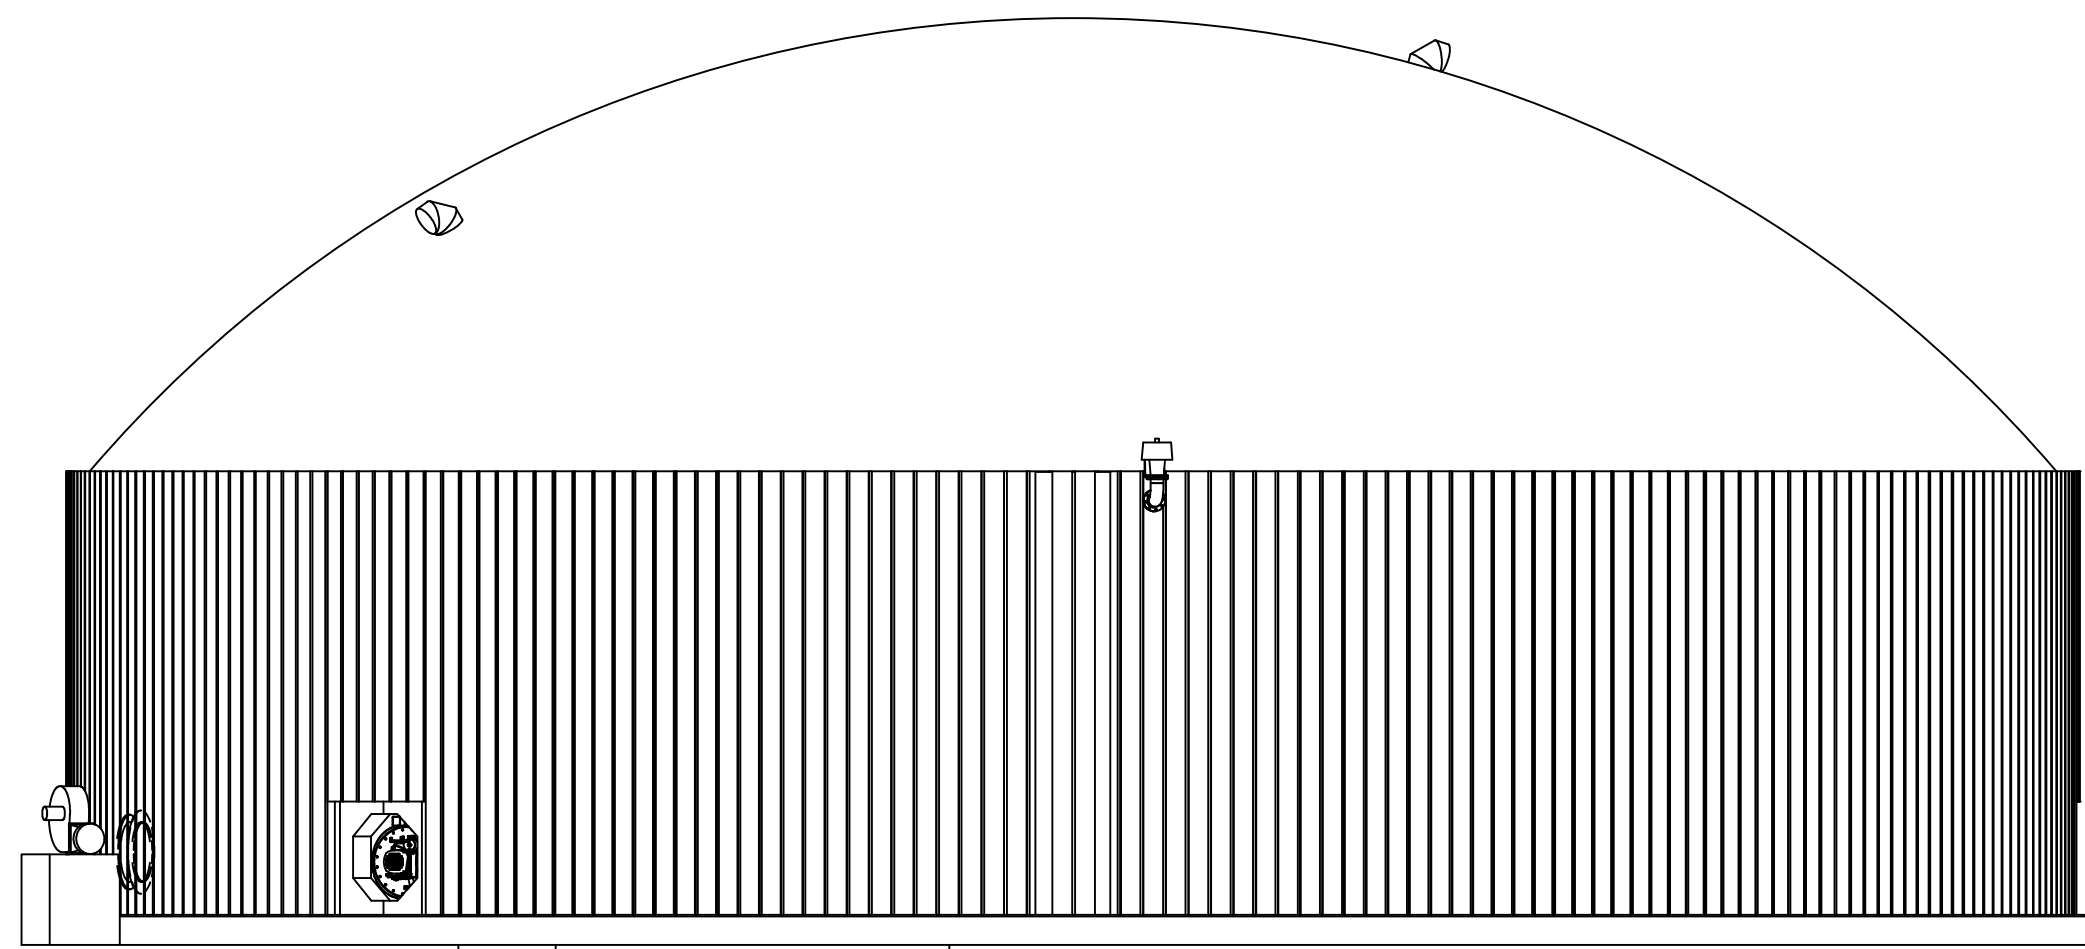
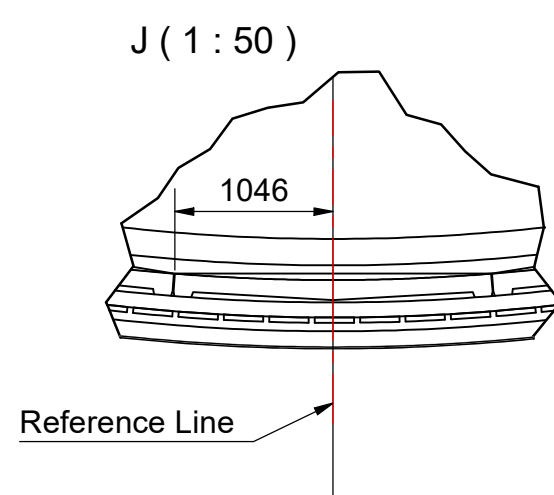


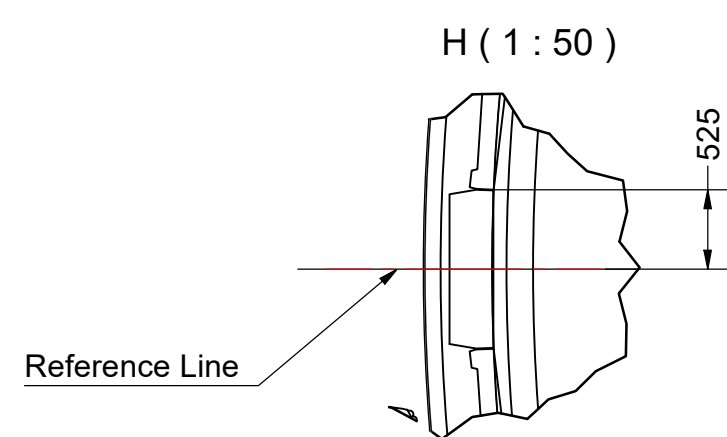


A-A (1 : 50)

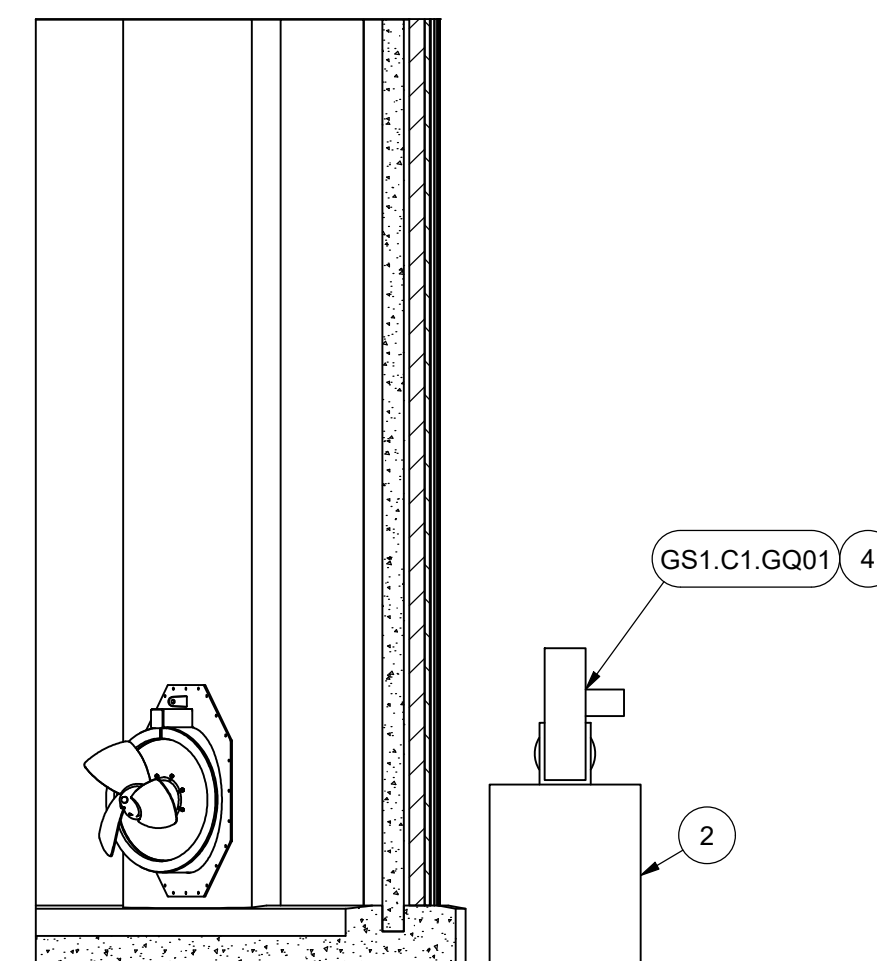


Digester Tank 2 - 9500m³
Ø23,9mx h21,7m

Post Digester - 3188m³
Ø26,0mx h6,0m

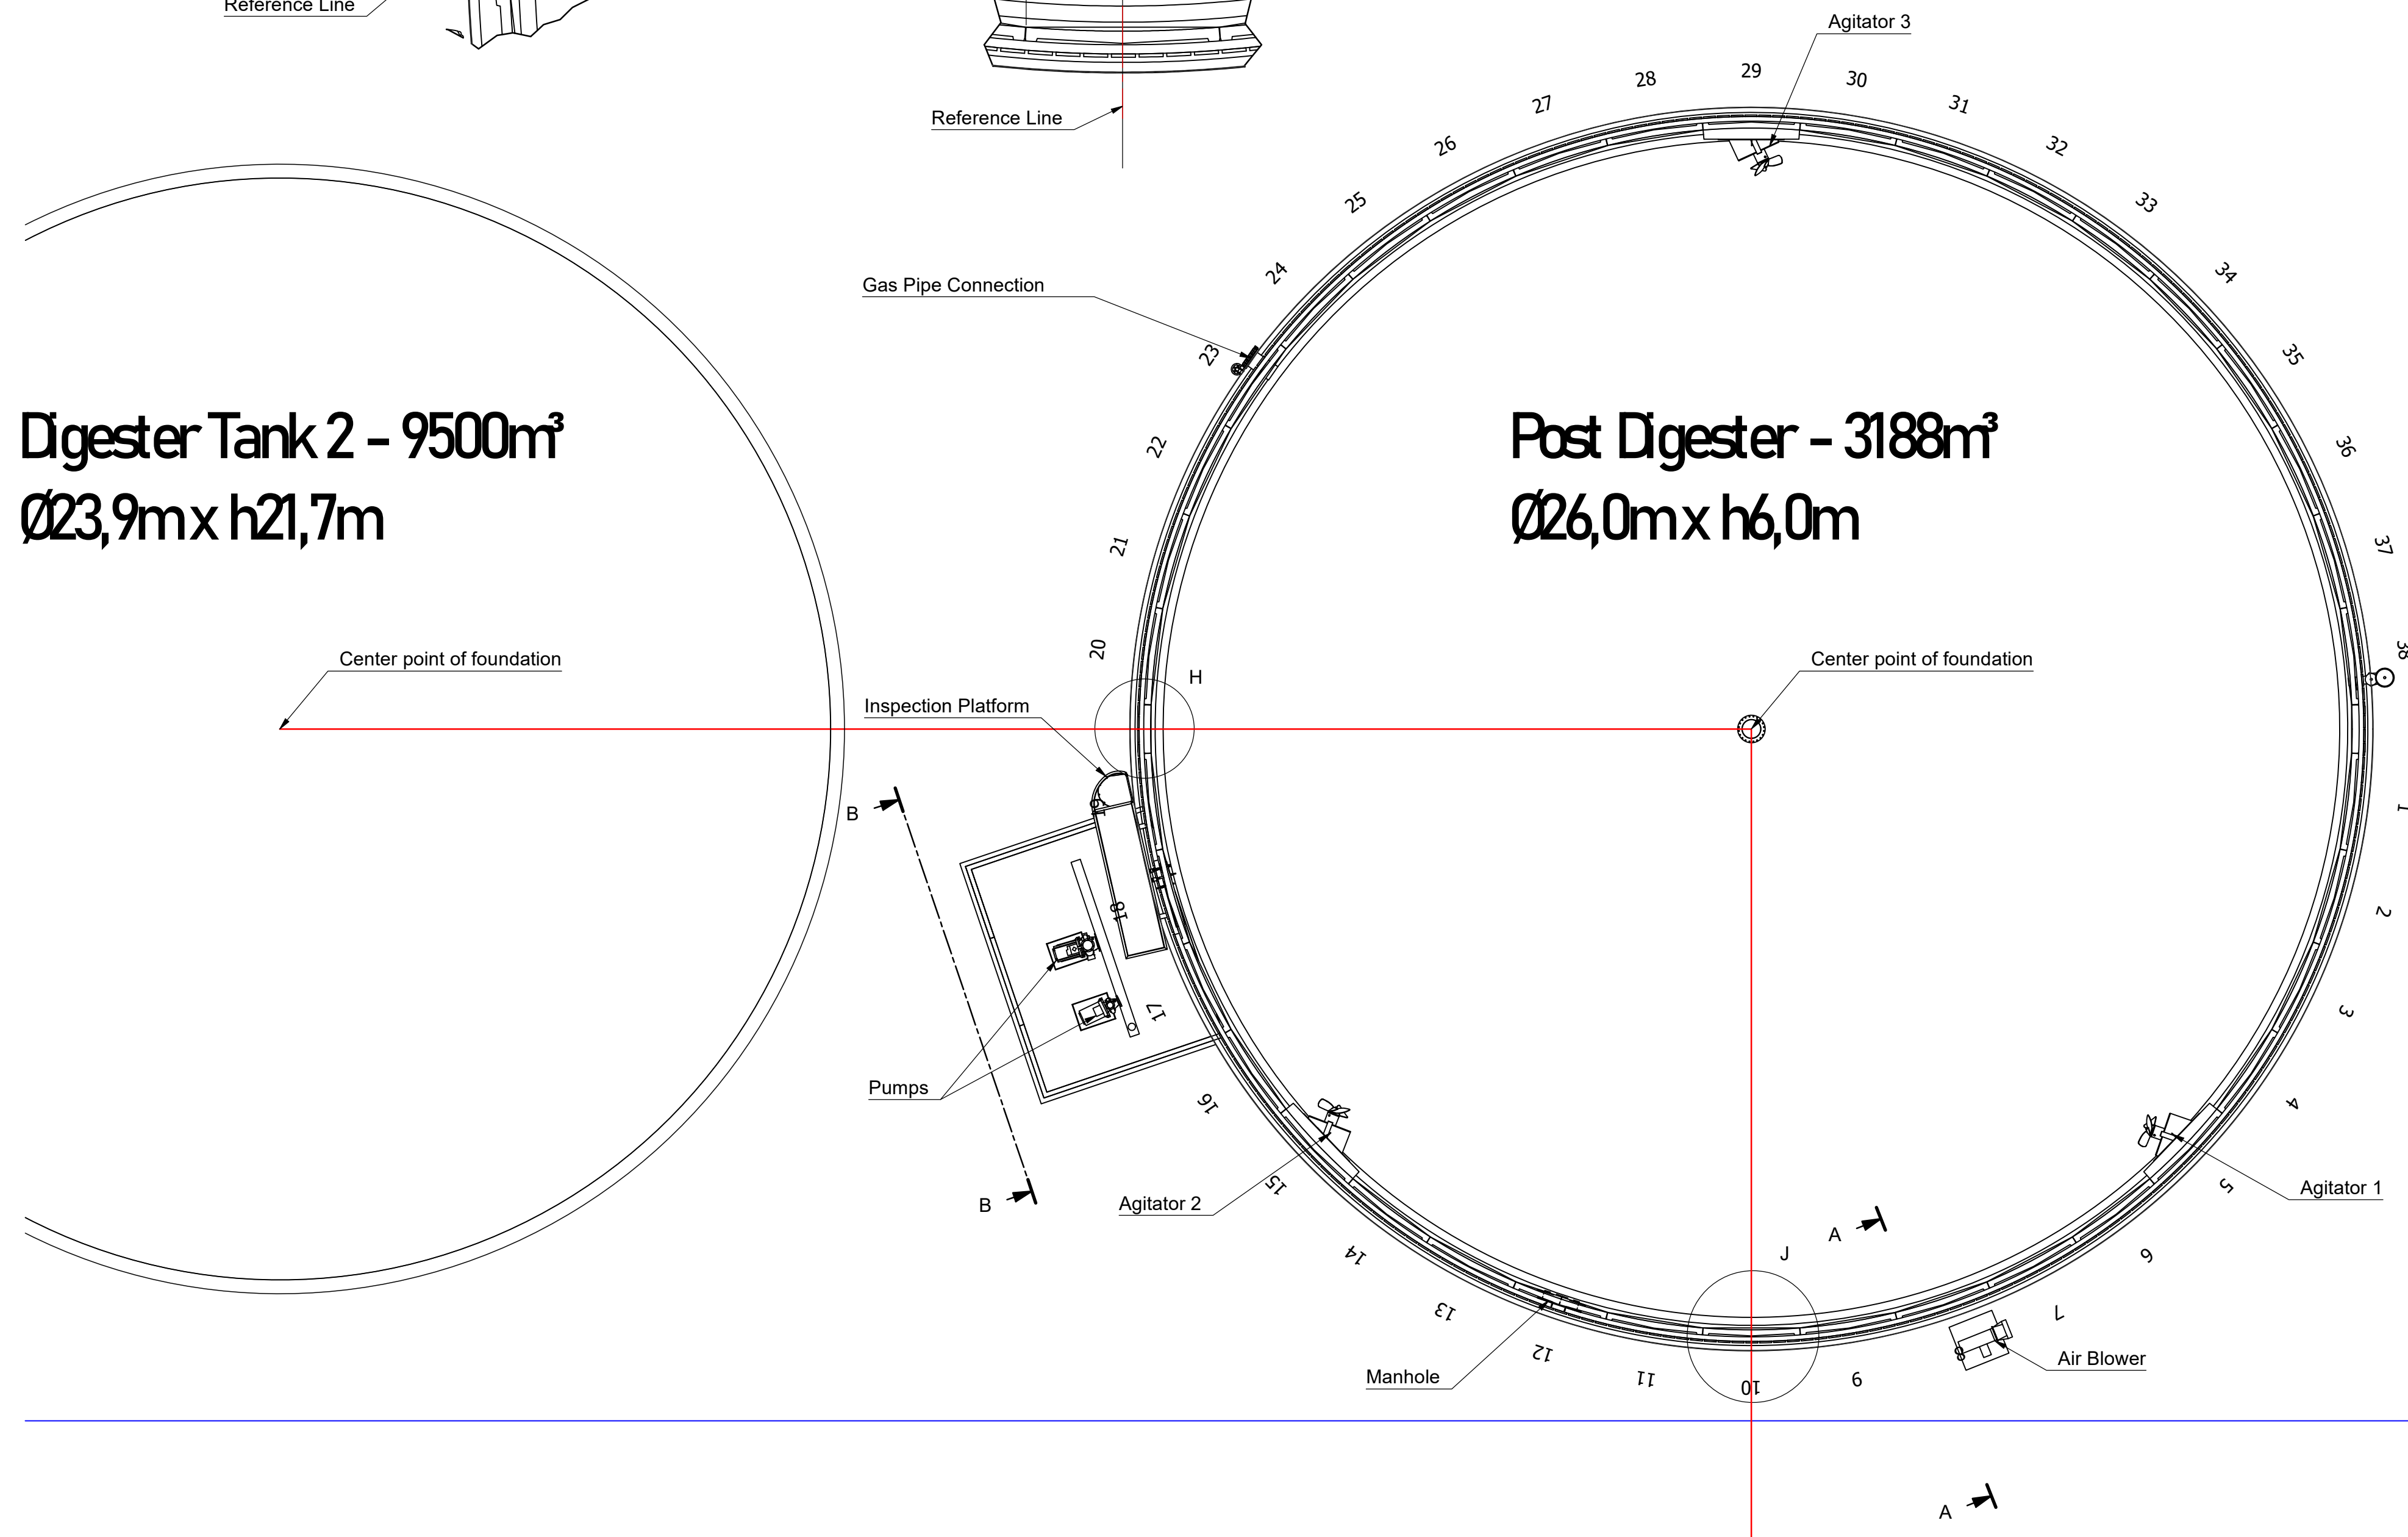

B-B (1 : 50)

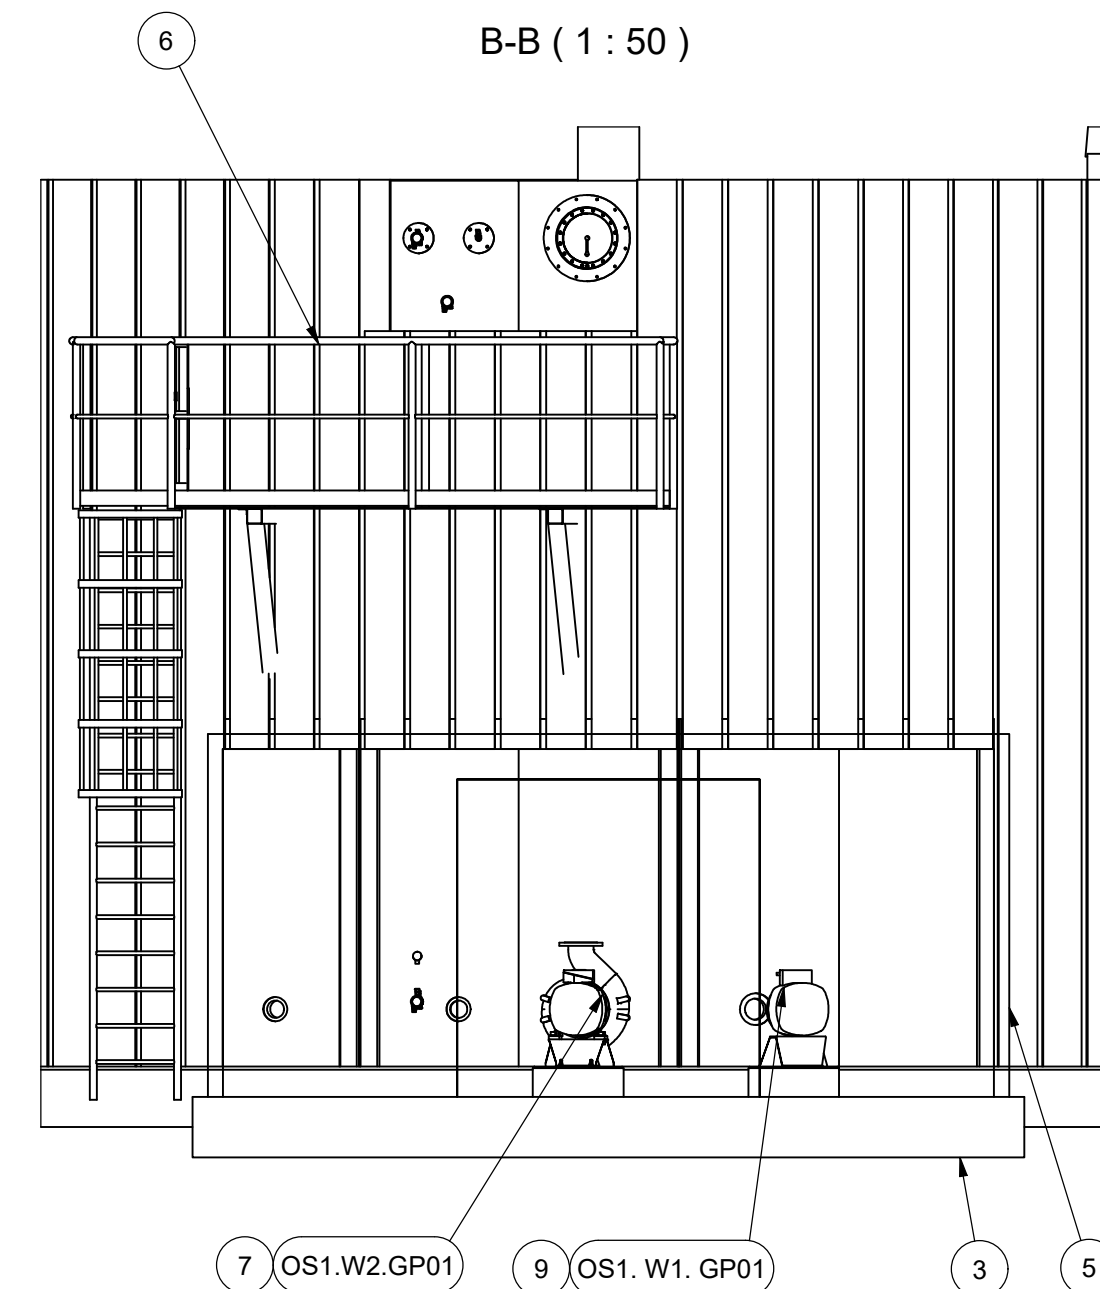

A	28-02-2025	jsc	adjust to A-Consult drawing, changed transmitter height, pump house changes	mca
-	18.09.2024	jsc		JLH
Rev	Date	Rev By	Description	Approved
Revision History				
9	1	0000-700-002	Pump - DN125 - 22kW - MPTK-I 80	N/A
8	1	4003-654-D01-03	Insulation 100mm	N/A
7	1	0000-700-002	Pump - DN250-SS - MPTK-I 150-30kW-1500rpm	N/A
6	1	4003-05-PS10	Inspection platform 2500x800	
5	1	4003-05-PS12-01	Pump House	-
4	1	0000-700-027	Air Blower - DNG 14-110 - 1,1kW - Klein	-
3	1	4003-05.1-BF02	Foundation Pipe Arrangement Biomass Outlet	Concrete
2	1	4003-05.1-BF01	Foundation Air Blower for Gas storage	Concrete
1	1	4003-619-A01	Storage Tank 1 - Equipment Assembly	
Pos. Qty	Part No.		Description	Material
Parts List				
Denne tegning må ikke overføres til, kopieres eller udrykkes af uvedkommande uden vor tilladelse.		This drawing remains our property. Its use without due authority is forbidden, and will lead to legal action.		Diese Zeichnung ist unser Eigentum. Unbefugte Benutzung ist verboten und wird gerichtlich verfolgt.
Ce dessin est notre propriété. Toute utilisation indue est interdite sous peine de poursuites légales.				
 Bigadan			Drawing State	
4003 - Nurmo Bioenergia Area 05 Storage Tank - Equipment			Released	
			Scale 1 : 100	
			Size A1 (594x841 mm)	
			Dwg No 4003-05.1-E01	
			Rev A	
Date : 02-11-2023			Sheet : 1 of 1	