


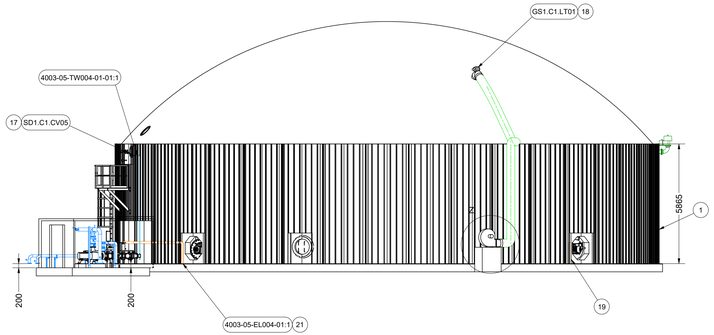


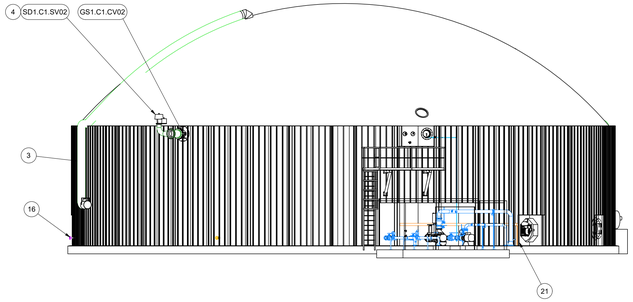


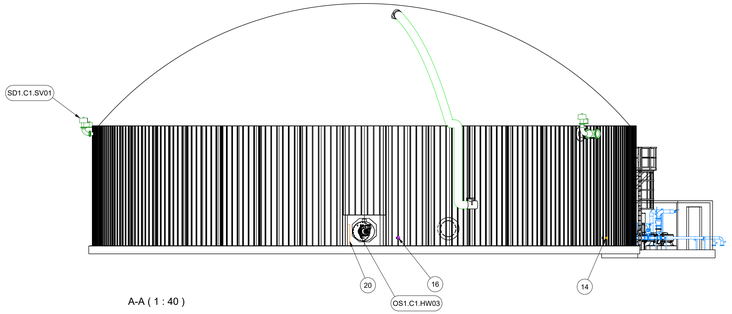


Z (1 : 50)

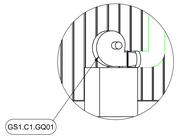


C-C (1 : 20)

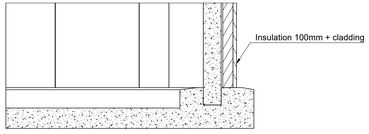


G-G (1 : 50)

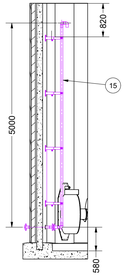


D-D (1 : 50)

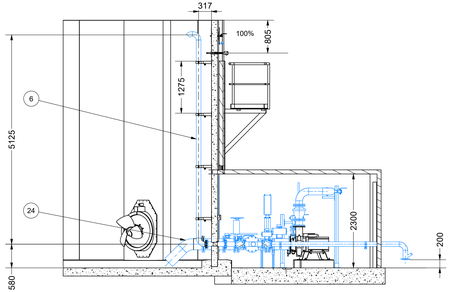


E-E (1 : 50)

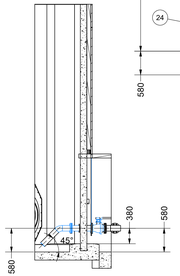


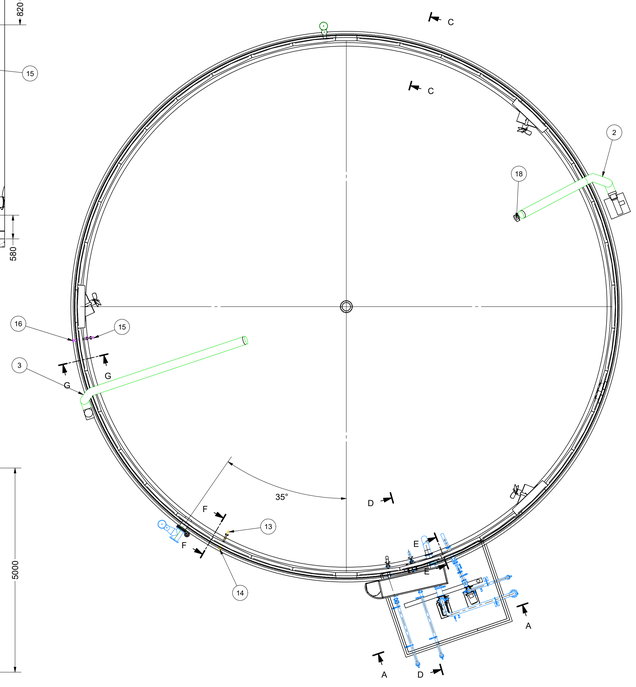


F-F (1 : 50)

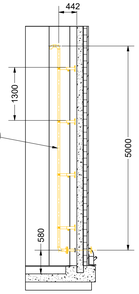

A-A (1 : 40)

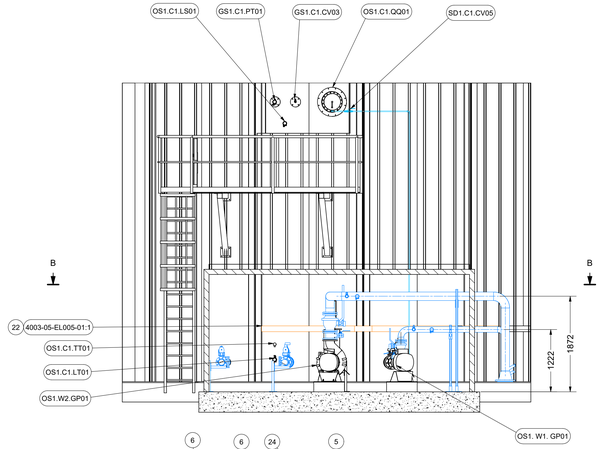

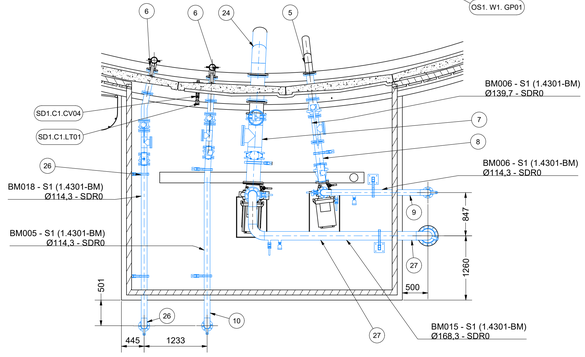

-- BM-Biomass --
-- BG-Biogas --
-- CS-Condensate --
-- CD-Cable ducts --
-- HW-Hot Water --
-- IC-Iron Chloride --
-- AF-Anti-Foam --
-- PA-Pressurized Air --
-- TD-Technical Drainage --
-- TW-Technical water --
-- OD-Odor --

BK - Bottom Level
RK - Rist Level

If nothing else is mentioned
Pipes must be carried up by the nearest possible wall.

Pos.	Qty	Part No.	Description	Material
27	1	4003-05.1-BM015-03	Piping DN125 - Biomass Outlet - Pump to ground	
26	1	4003-05.1-BM18-01	Biomass In BM018	
25	2	4003-05.2-BM005-03-02	Connection Pipe Through Wall	
24	1	4003-05-PS13	Piping DN125 - Biomass Outlet	
23	2	0000-701-001	Ball valve - DN50 - manual - Valtor V-106	Stainless Steel
22	1	4003-05.1-EL005	Cable Tray	
21	1	4003-05.1-EL004	Cable Tray	
20	1	4003-05.1-EL003	Cable Tray	
19	1	4003-05.1-EL002	Cable Tray	
18	1	0000-700-109	Level Transmitter - Tecon - Dummy	-
17	2	4003-05.1-TW004-01	Piping DN15 - Technical Water to Sight Glass	
16	1	4003-05.1-SL001-02	Piping DN50 - Sulphurous Liquid - Link Seal Pipe	
15	1	4003-05.1-SL001-01	Piping DN50 - Inlet Sulphurous Liquid	
14	1	4003-05.1-CS001-02	Piping DN50 - Condensate - Link Seal Pipe	
13	1	4003-05.1-CS001-01	Piping DN50 - Condensate	
12	1	4003-05.1-BM015-01	Piping DN100 - Biomass Outlet - Link Seal Pipe	
11	1	4003-05.1-BM006-01	Piping DN100 - Biomass Outlet - Link Seal Pipe	
10	1	4003-05.1-BM005-01	Piping DN100 - Biomass Inlet - Link Seal Pipe	
9	1	4003-05.1-BM006-03	Piping DN125 - Biomass Outlet - Pump to ground	
8	1	4003-05.1-BM006-02	Piping DN125 - Biomass Outlet	
7	1	4003-05.1-BM015-02	Piping DN125 - Biomass Outlet	
6	2	4003-05-PS08	Piping DN100 - Biomass Inlet	
5	1	4003-05-PS07	Piping DN125 - Biomass Outlet	
4	1	4003-05.1-BG005-01	Piping DN350 - Main Gas Pipe	
3	1	4003-05.1-AA002-01	Air Outlet	
2	1	4003-05.1-AA001-01	Air Inlet	
1	1	4003-05.1-E01	Storage Tank - Equipment	

Parts List

Denne tegning må ikke overdades til kopieres eller udnyttes af uvedkommende uden vor tilladelse.

This drawing remains our property. Its use without due authority is forbidden, and will lead to legal action.

Diese Zeichnung ist unser Eigentum. Unbefugte Benutzung ist verboten und wird gerichtlich verfolgt.

Ce dessin est notre propriété. Toute utilisation indue est interdite sous peine de poursuites légales.

Bigadan A/S
Dronning Sophies Allé 7A
DK - 9000 Aalborg
Tel.: +45 88 57 90 90
www.bigadan.com

Drawing State: Released

4003 - Nurmo Bioenergia
Area 05
Storage Tank Area

Scale: 1 : 100
Size: A1 (594x1261 mm)
Dwg No: 4003-05.1-A01
Rev: -
Date: 13-02-2023
Sheet: 1 of 1