



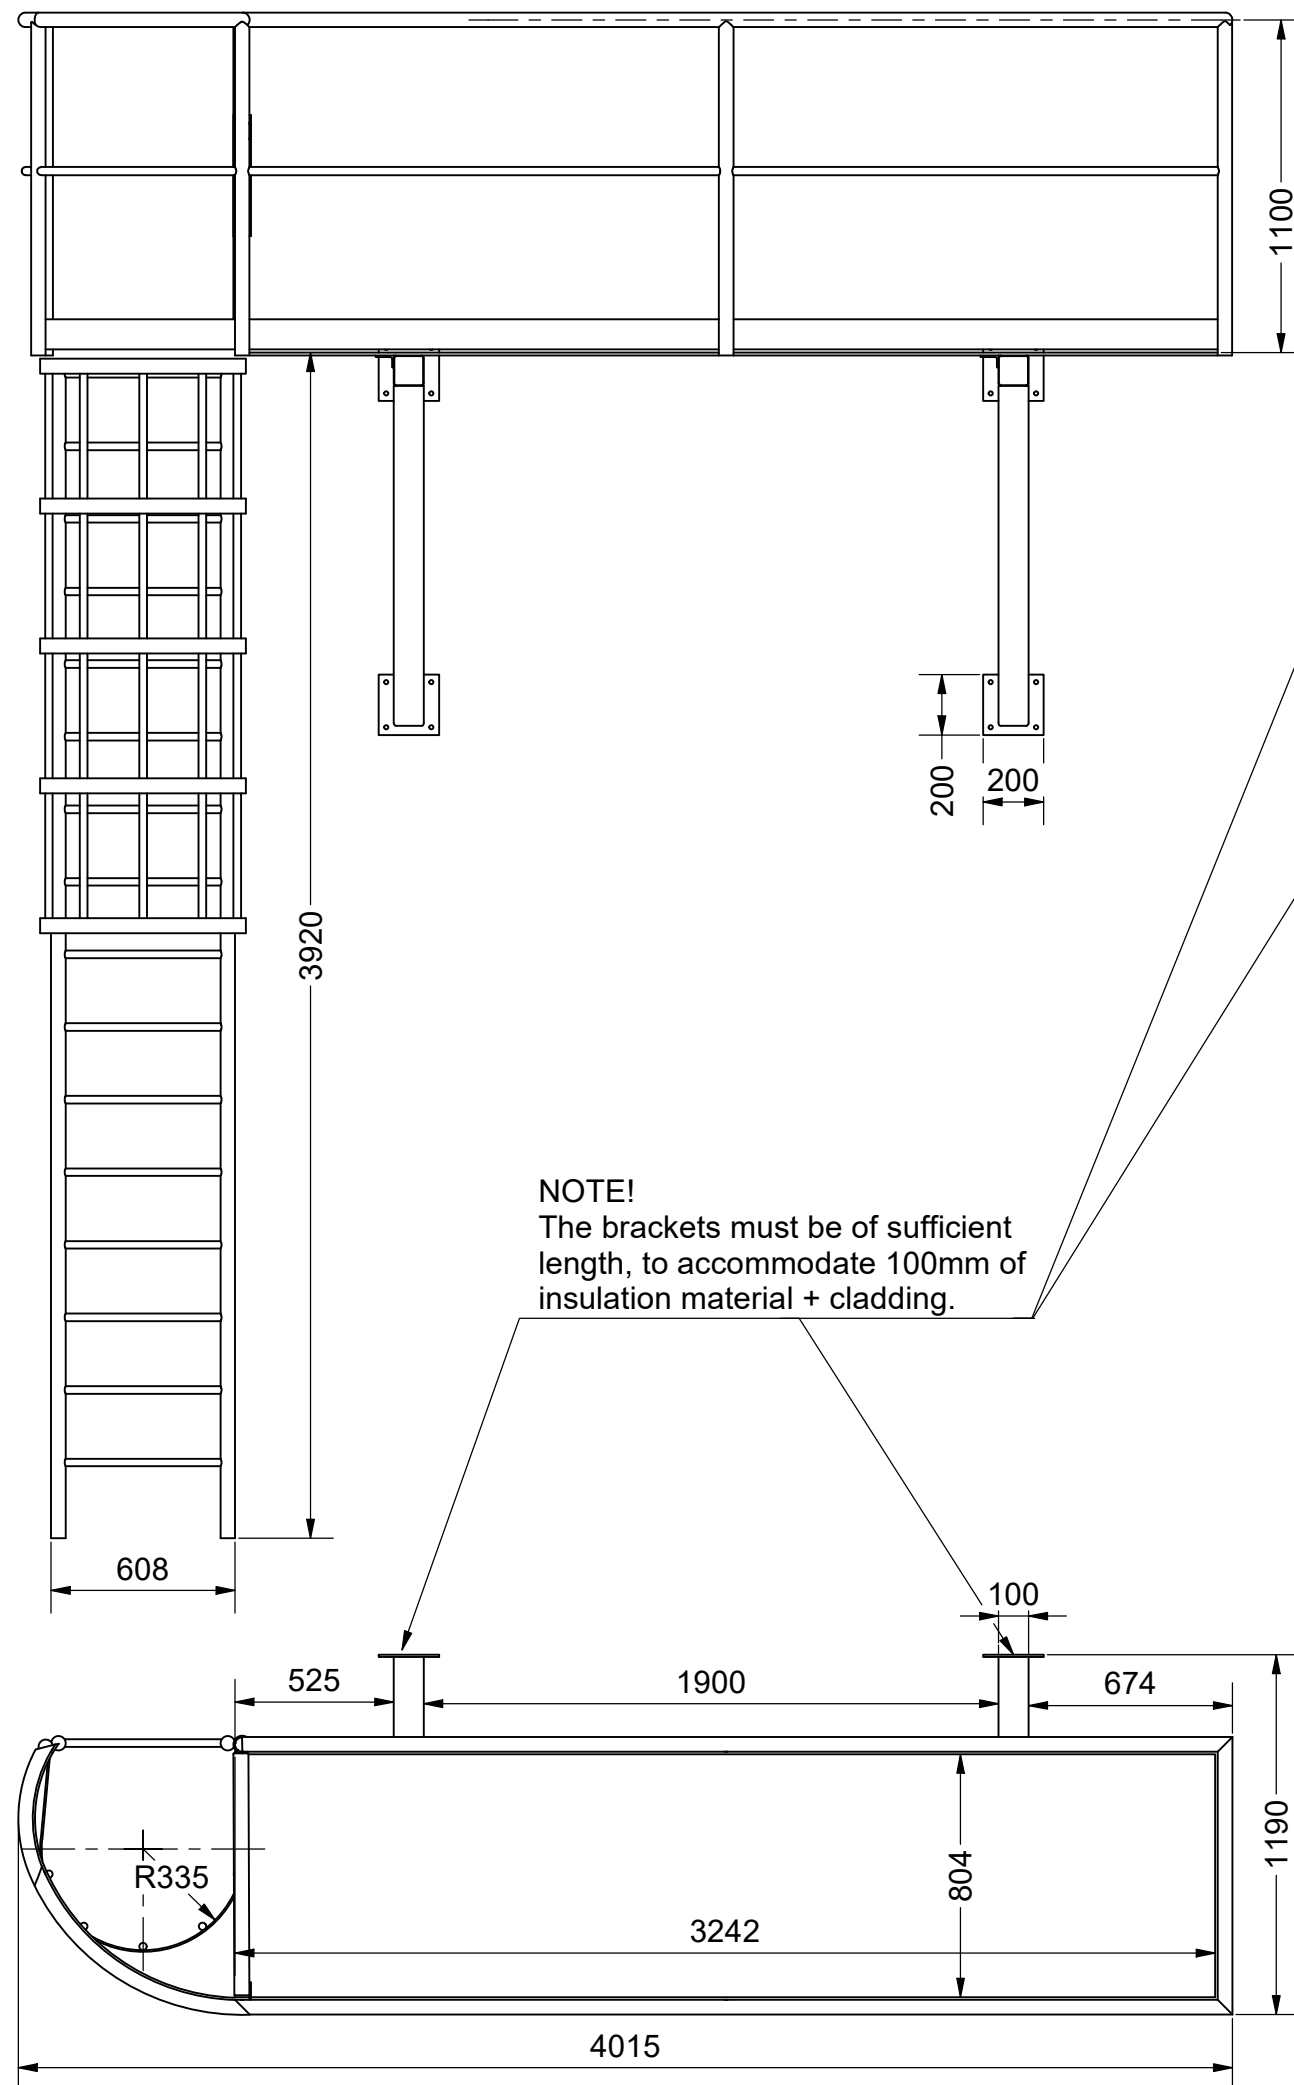

NOTE!
The brackets must be of sufficient length, to accommodate 100mm of insulation material + cladding.

NOTE!
Safety Door
Must be added

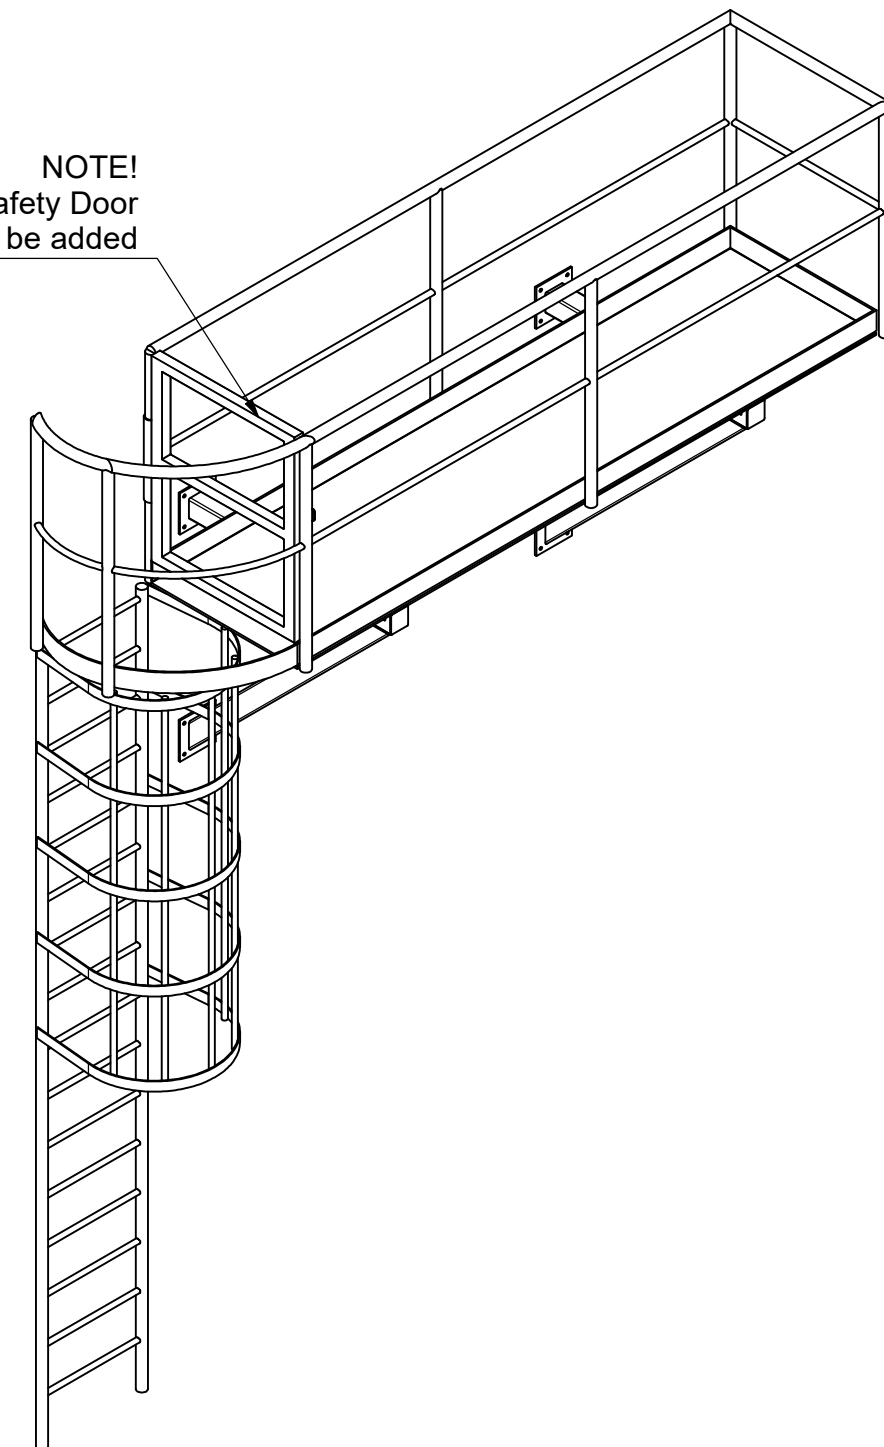

Denne tegning må ikke overlades til, kopieres eller udnyttes af uvedkommende uden vor tilladelse.

This drawing remains our property. Its use without due authority is forbidden, and will lead to legal action.

Diese Zeichnung ist unser Eigentum. Unbefugte Benutzung ist verboten und wird gerichtlich verfolgt.

Ce dessin est notre propriété. Toute utilisation indue est interdite sous peine de poursuites légales.



Bigadan A/S
Dronning Sophies Allé 7A
DK - 8660 Skanderborg
Tel. : +45 86 57 90 90
www.bigadan.com

Drawing State

Released

Scale 1 : 25

Size A3 (297x420 mm)

Dwg No

4003-05-PS10

Date : 12-12-2024

Sheet : 1 of 1

4003 - Nurmo Bioenergia

Inspection platform 2500x800