


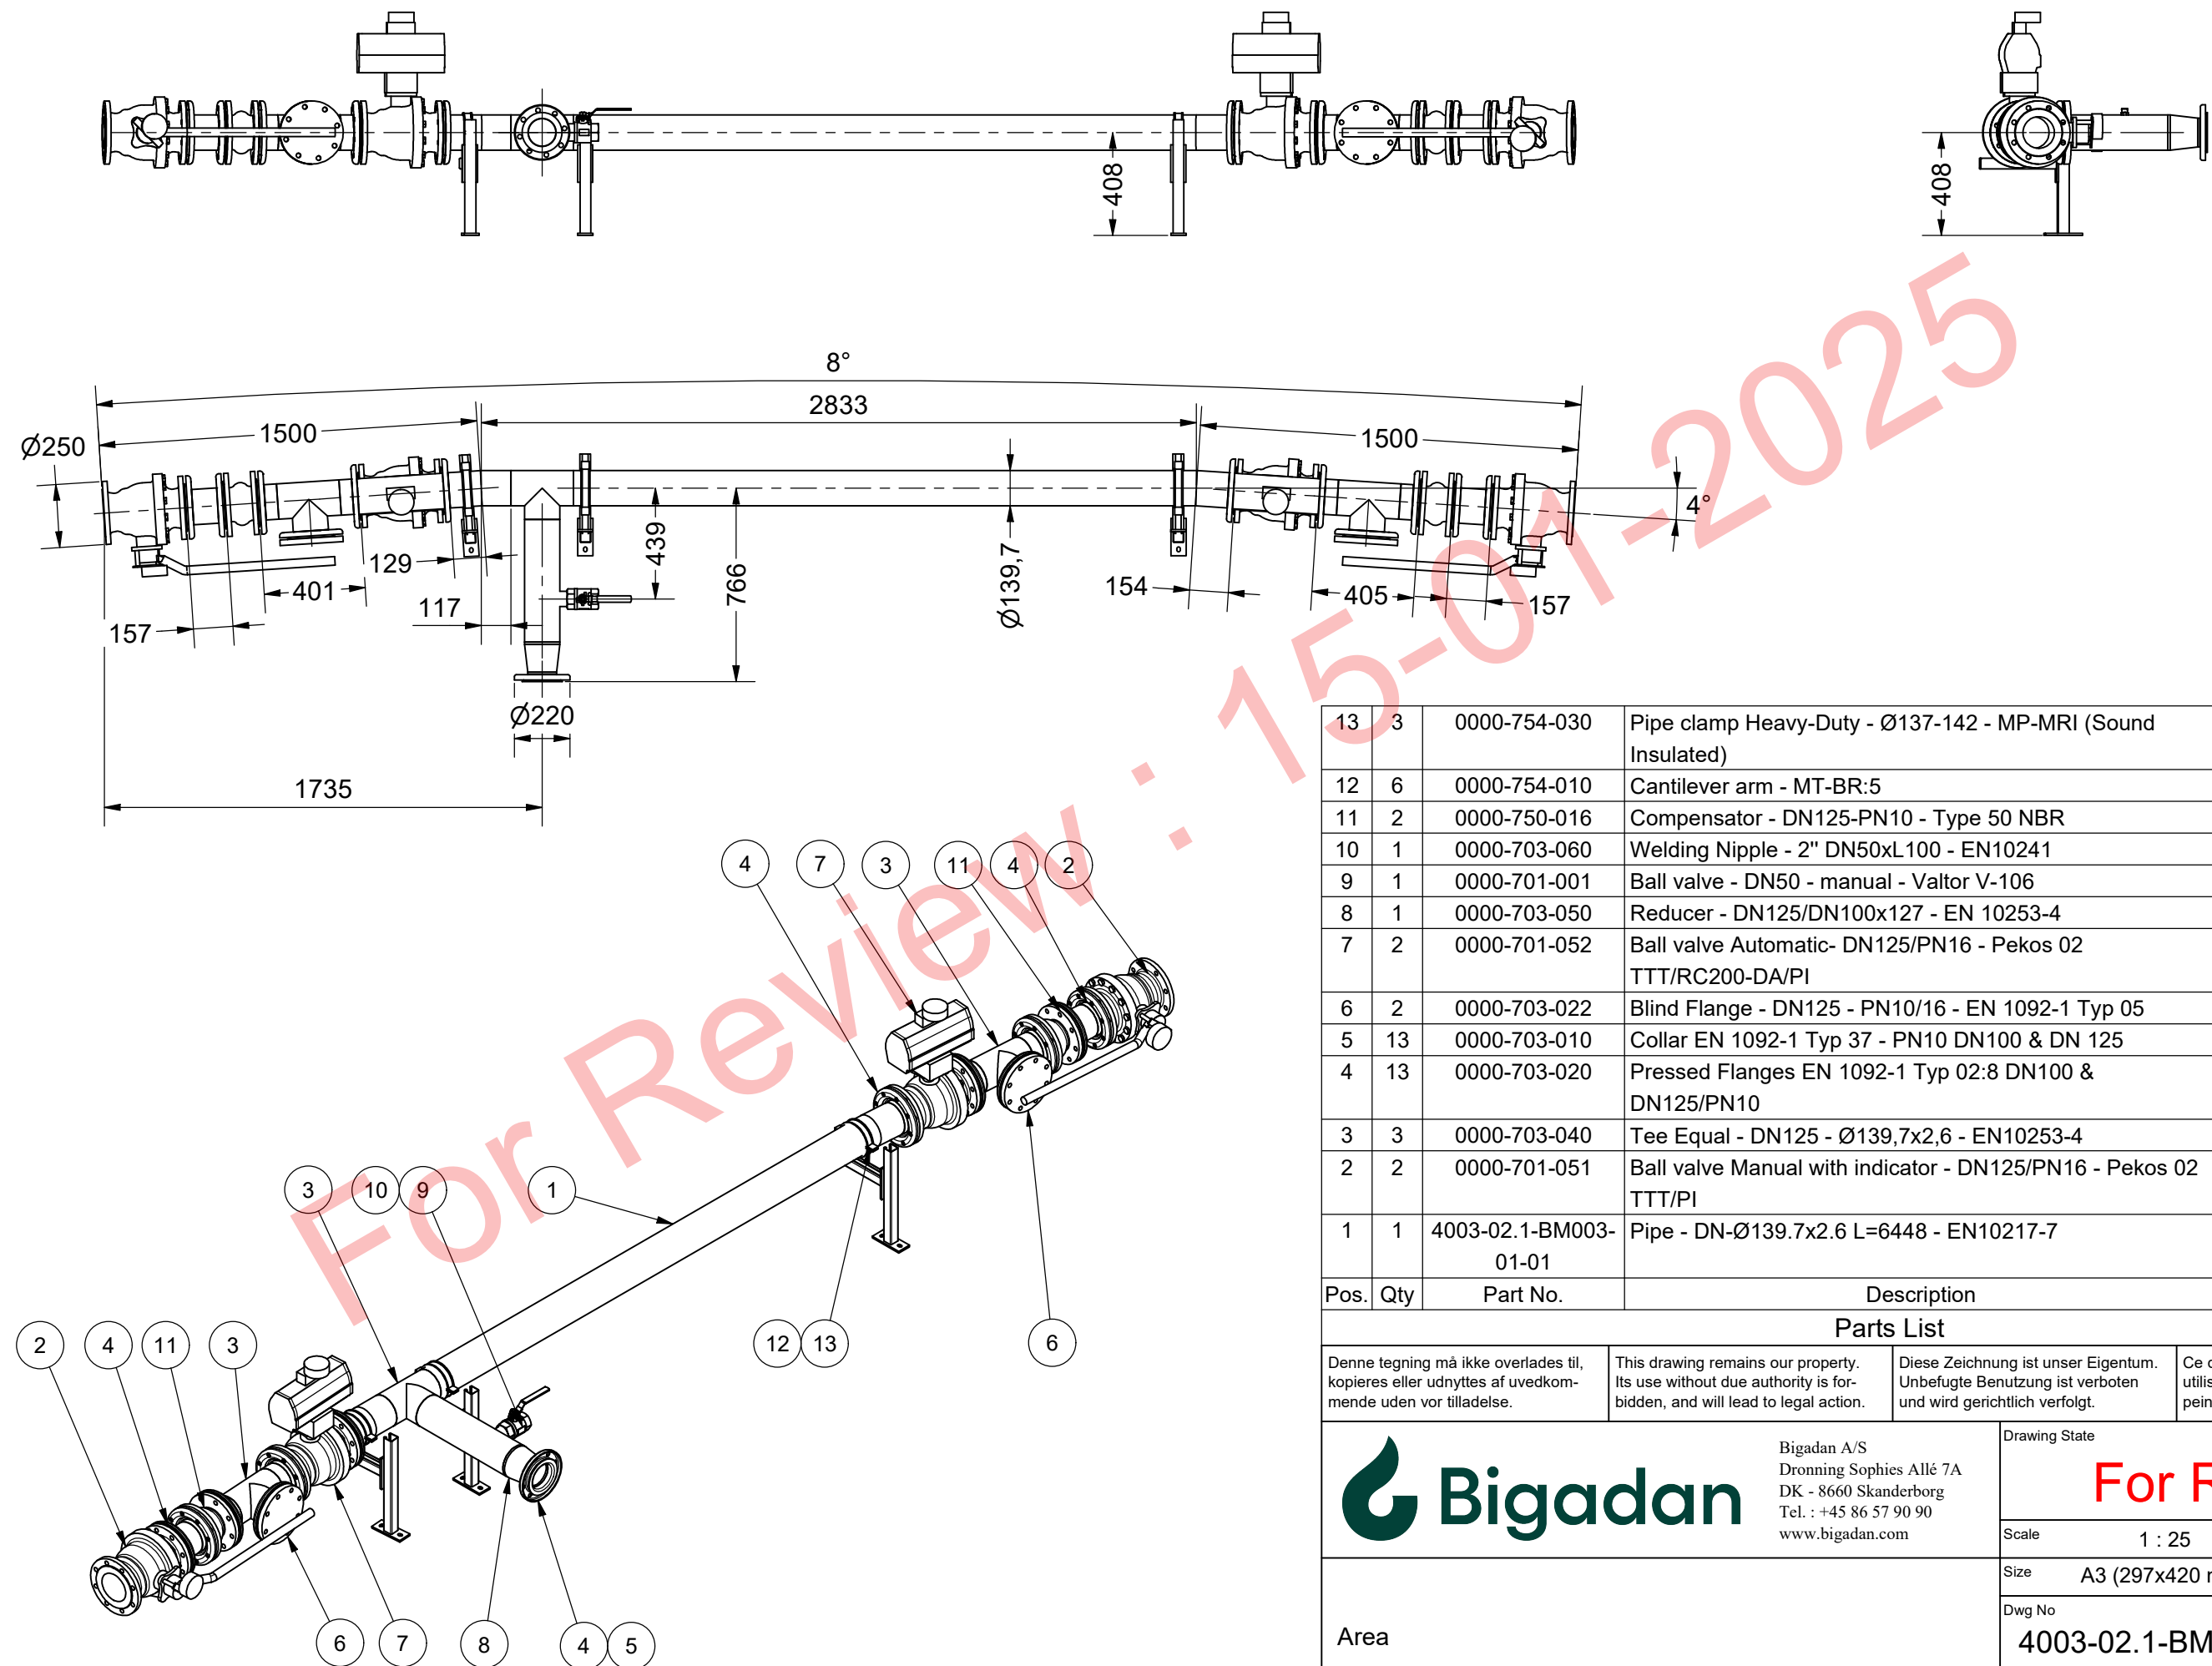

13	3	0000-754-030	Pipe clamp Heavy-Duty - Ø137-142 - MP-MRI (Sound Insulated)	Steel, Galv.
12	6	0000-754-010	Cantilever arm - MT-BR:5	Steel, Galv.
11	2	0000-750-016	Compensator - DN125-PN10 - Type 50 NBR	-
10	1	0000-703-060	Welding Nipple - 2" DN50xL100 - EN10241	SS 1.4571 - AISI 316Ti
9	1	0000-701-001	Ball valve - DN50 - manual - Valtor V-106	Stainless Steel
8	1	0000-703-050	Reducer - DN125/DN100x127 - EN 10253-4	SS 1.4571 - AISI 316Ti
7	2	0000-701-052	Ball valve Automatic- DN125/PN16 - Pekos 02 TTT/RC200-DA/PI	N/A
6	2	0000-703-022	Blind Flange - DN125 - PN10/16 - EN 1092-1 Typ 05	SS 1.4571 - AISI 316Ti
5	13	0000-703-010	Collar EN 1092-1 Typ 37 - PN10 DN100 & DN 125	SS 1.4571 - AISI 316Ti
4	13	0000-703-020	Pressed Flanges EN 1092-1 Typ 02:8 DN100 & DN125/PN10	SS 1.4301 - AISI 304
3	3	0000-703-040	Tee Equal - DN125 - Ø139,7x2,6 - EN10253-4	SS 1.4571 - AISI 316Ti
2	2	0000-701-051	Ball valve Manual with indicator - DN125/PN16 - Pekos 02 TTT/PI	N/A
1	1	4003-02.1-BM003-01-01	Pipe - DN-Ø139.7x2.6 L=6448 - EN10217-7	SS 1.4301 - AISI 304
Pos.	Qty	Part No.	Description	Material

Parts List

Denne tegning må ikke overlades til, kopieres eller udnyttes af uvedkomende uden vor tilladelse.

This drawing remains our property. Its use without due authority is forbidden, and will lead to legal action.

Diese Zeichnung ist unser Eigentum. Unbefugte Benutzung ist verboten und wird gerichtlich verfolgt.

Ce dessin est notre propriété. Toute utilisation indue est interdite sous peine de poursuites légales.



Bigadan A/S
Dronning Sophies Allé 7A
DK - 8660 Skanderborg
Tel. : +45 86 57 90 90
www.bigadan.com

Drawing State

For Review

Scale 1 : 25

Size A3 (297x420 mm)

Dwg No

4003-02.1-BM003-01

Date : 16-12-2024

Sheet : 1 of 1

Area

Distribution Piping from Mixer tanks to Pump