

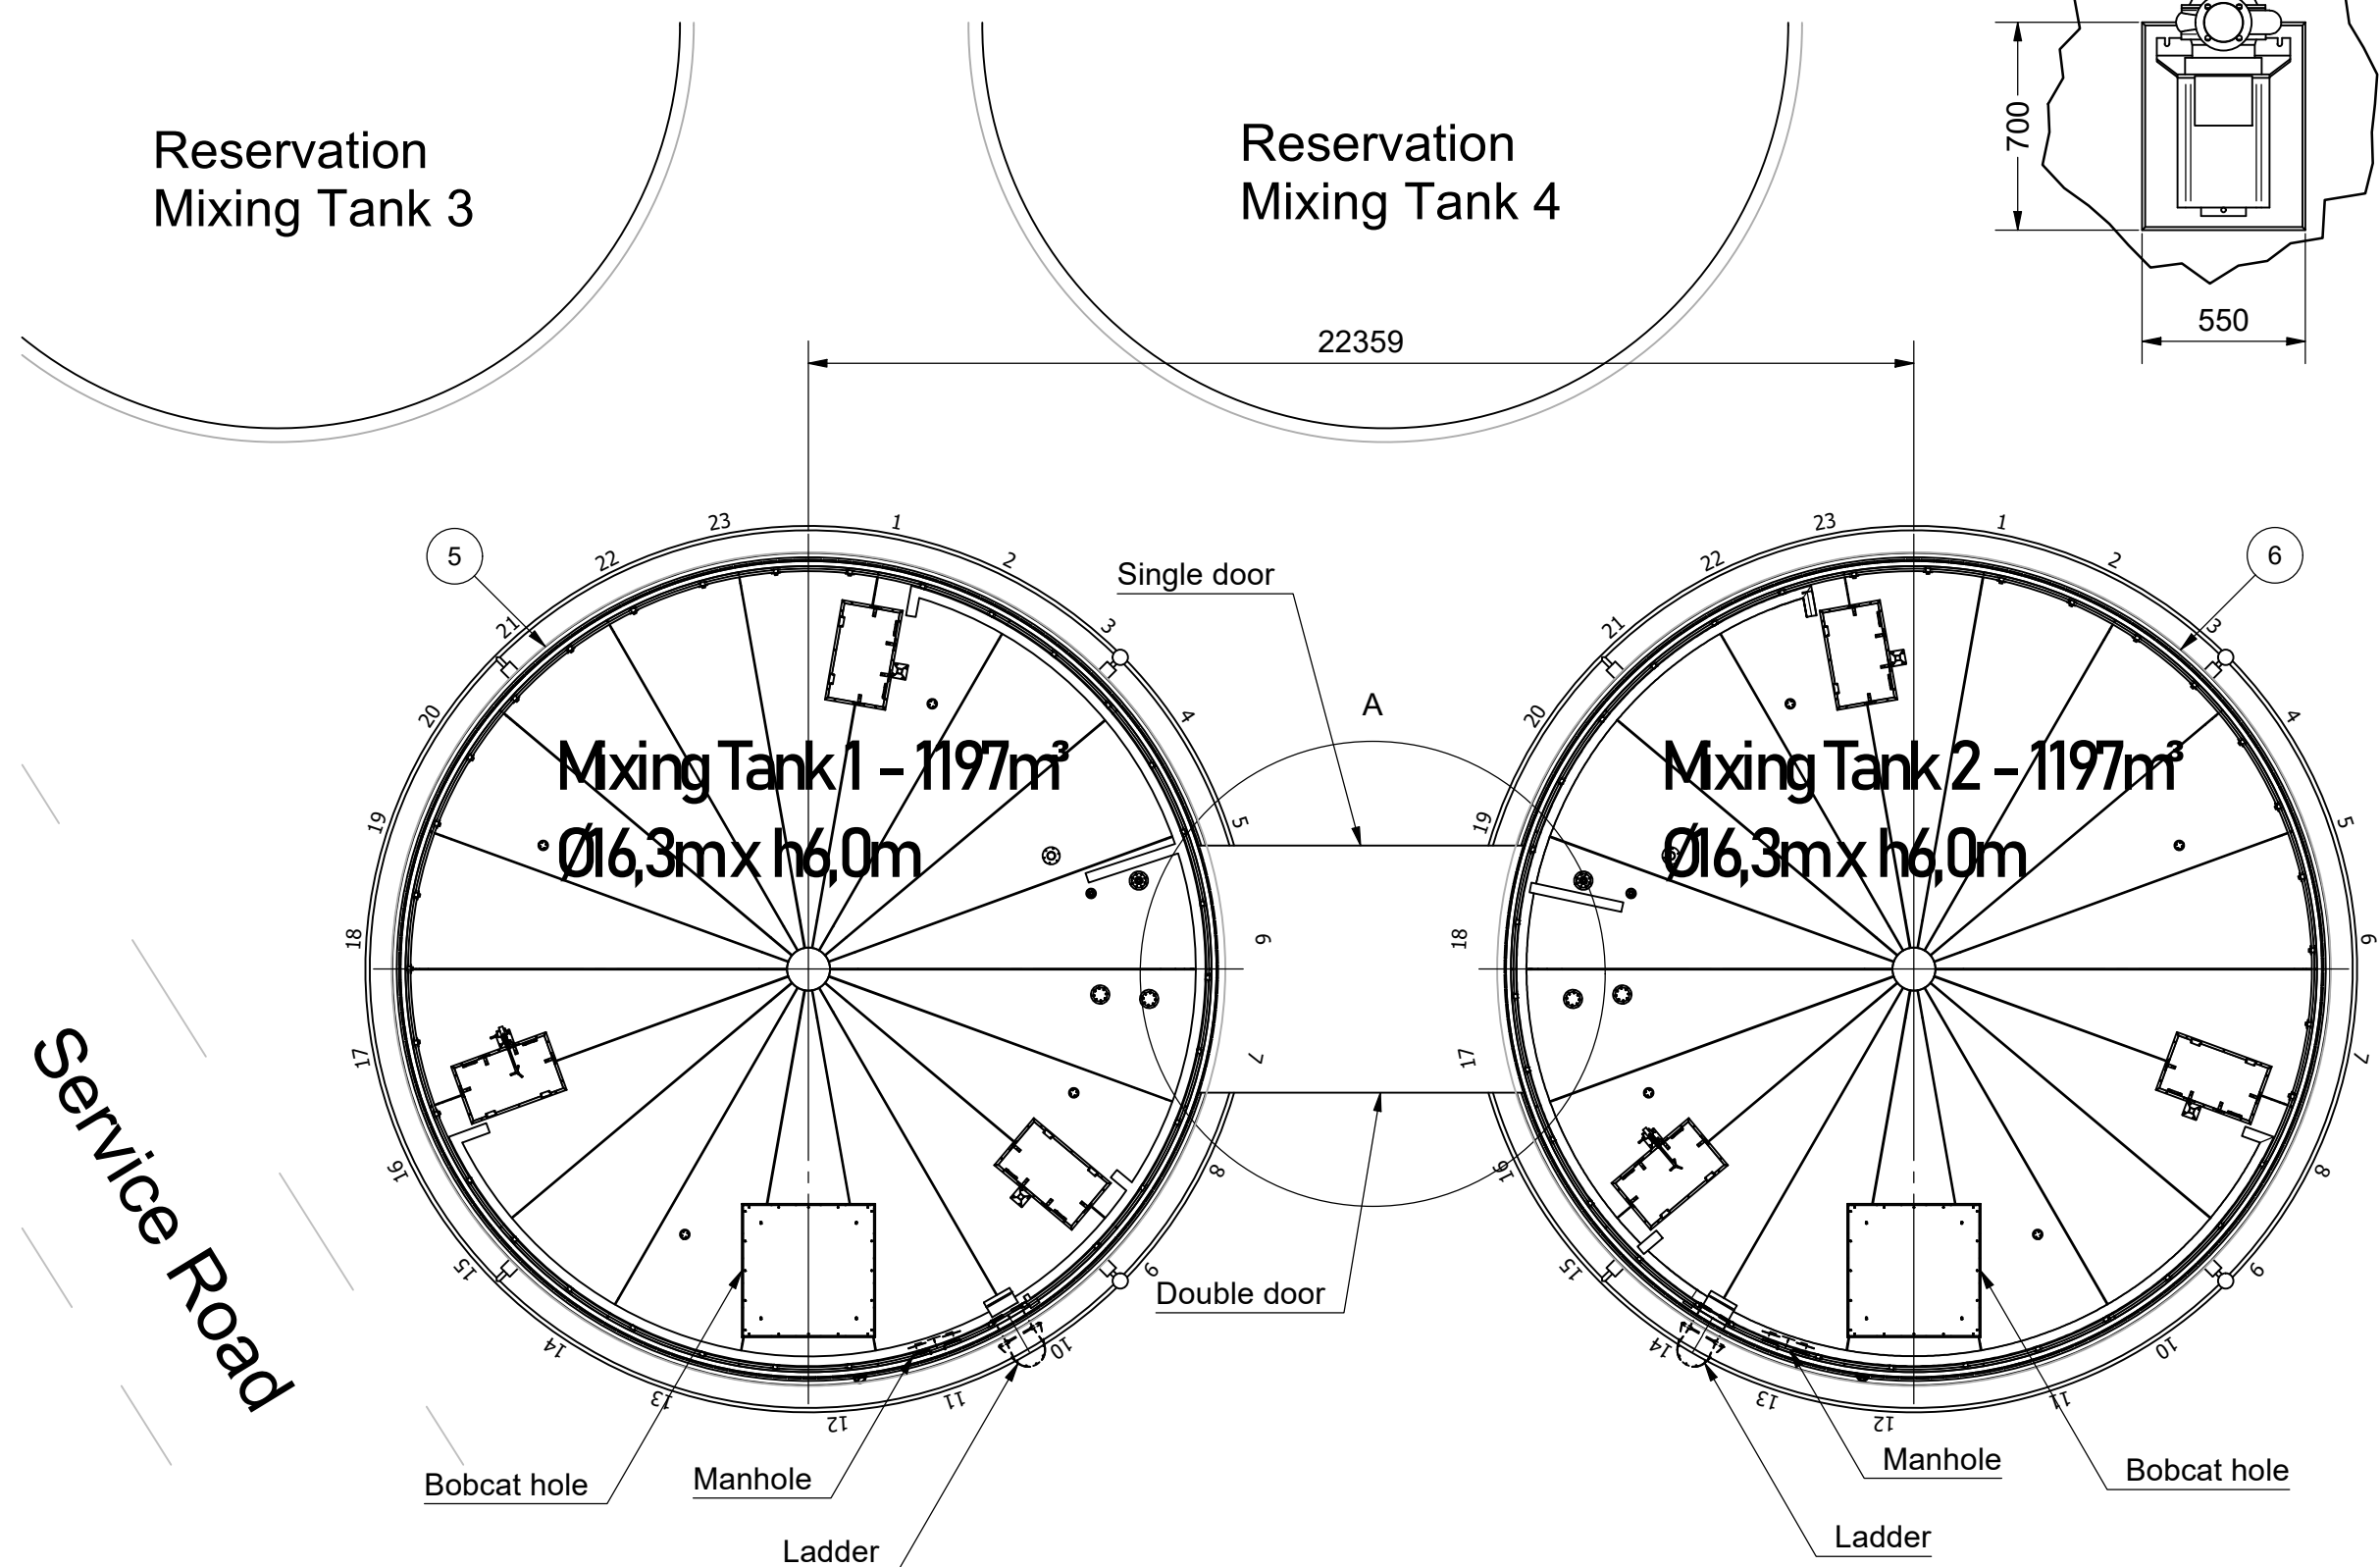
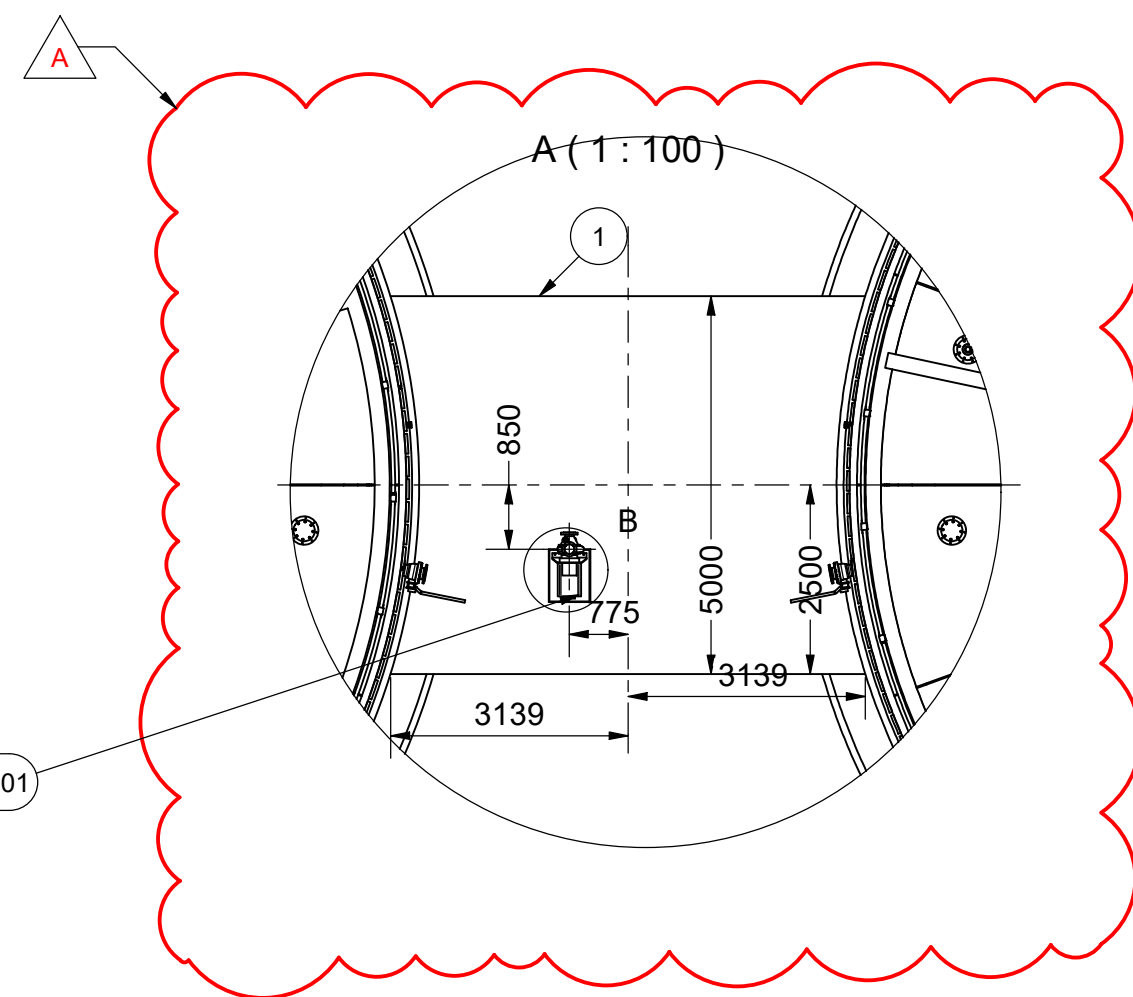
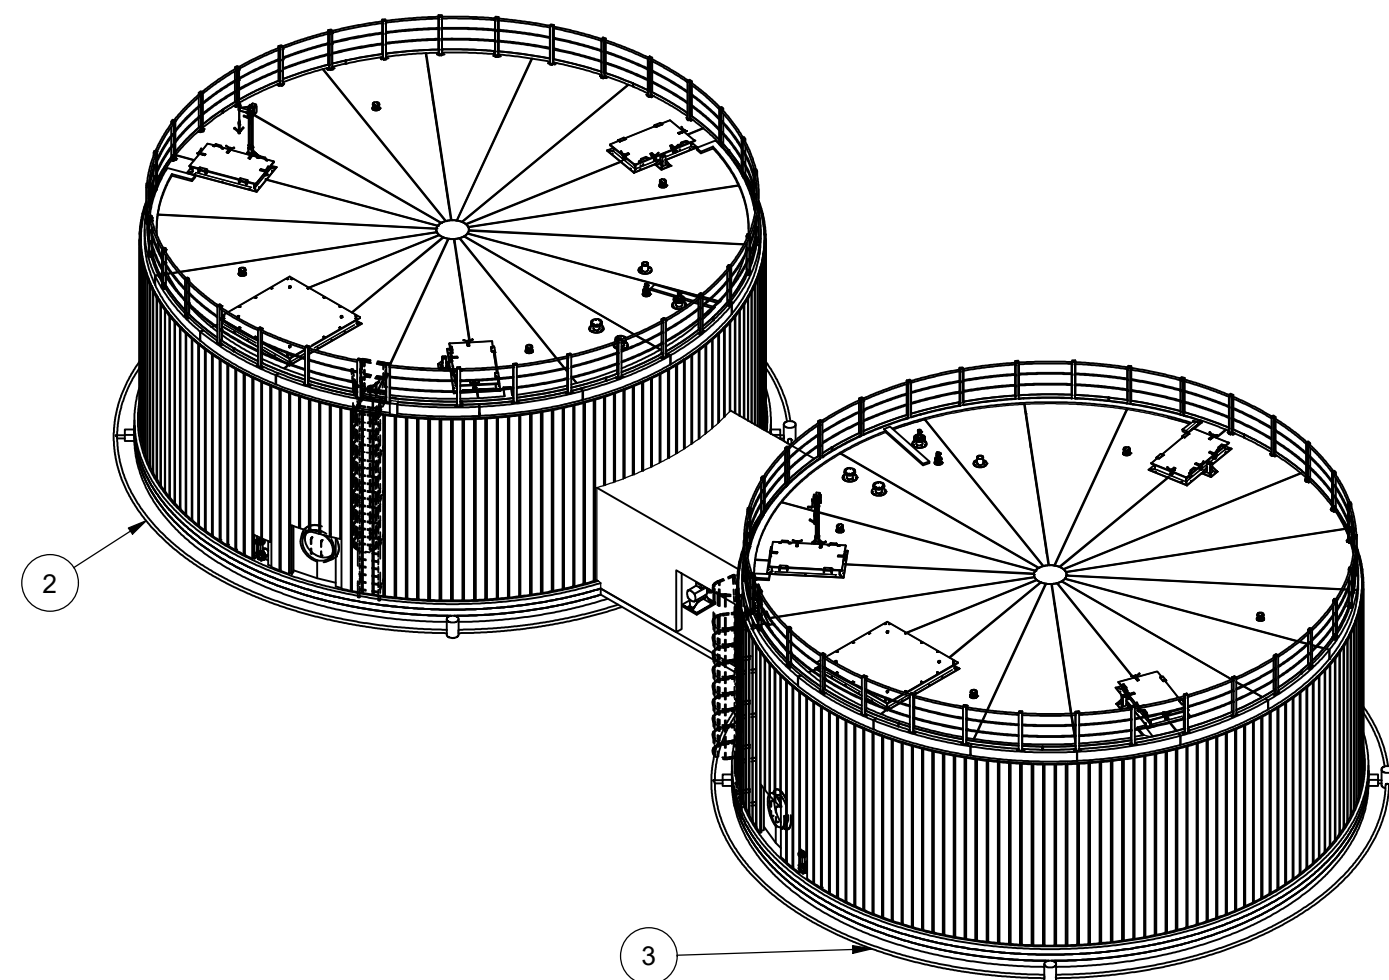
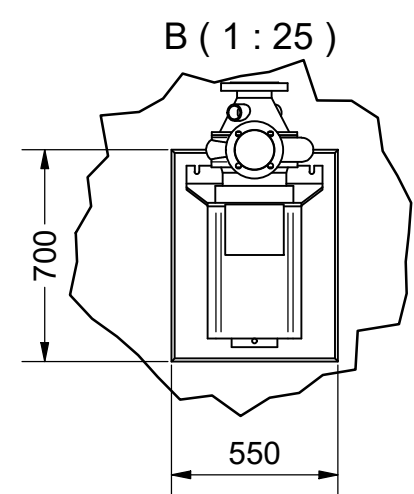


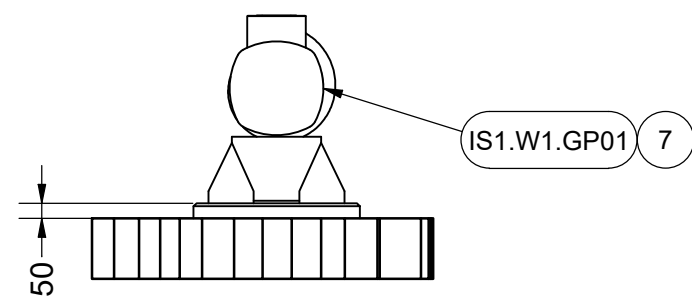

A	25-09-2024	jch	Moved pump house foundation and pump	JCH
-	18-09-2024	jch		JLH
Rev	Date	Rev By	Description	Approved

Revision History				
7	1	0000-700-002	Pump - DN100 - 18,5kW - MPTK-I 80	N/A
6	1	4003-613-A02	Mixing Tank 2	
5	1	4003-613-A01	Mixing Tank 1	
4	1	4003-02.1-B01	Common Pump House	-
3	1	4003-613-F02	Mixing Tank 2 Foundation	Concrete
2	1	4003-613-F01	Mixing Tank 1 Foundation	Concrete
1	1	4003-02.1-F01	Pump House Foundation	Concrete
Pos.	Qty	Part No.	Description	Material

Parts List			
Denne tegning må ikke overlades til, kopieres eller udnyttes af uvedkommende uden vor tilladelse.	This drawing remains our property. Its use without due authority is forbidden, and will lead to legal action.	Diese Zeichnung ist unser Eigentum. Unbefugte Benutzung ist verboten und wird gerichtlich verfolgt.	Ce dessin est notre propriété. Toute utilisation indue est interdite sous peine de poursuites légales.

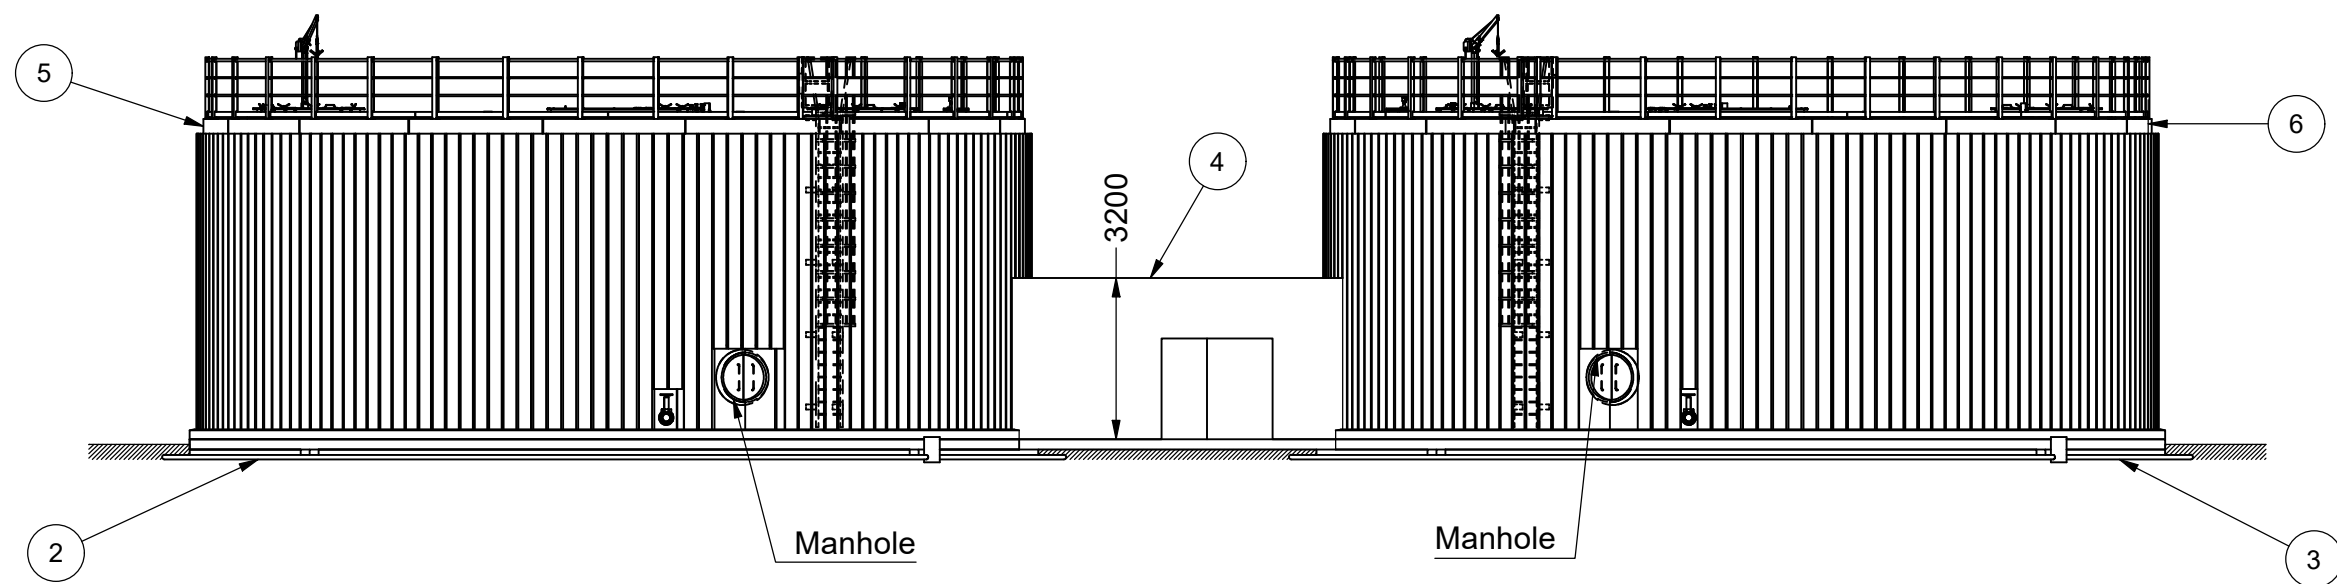

Bigadan A/S
Dronning Sophies Allé 7A
DK - 8660 Skanderborg
Tel. : +45 86 57 90 90
www.bigadan.com

Drawing State
Released

Scale
1 : 150

Size
A2 (420x594 mm)

Dwg No
4003-02.1-E01

Date : 17-09-2024

4003 - Nurmo Bioenergia
Area 02 - Mixing Tank Area
Equipment Layout

Rev
A

Sheet : 1 of 1