


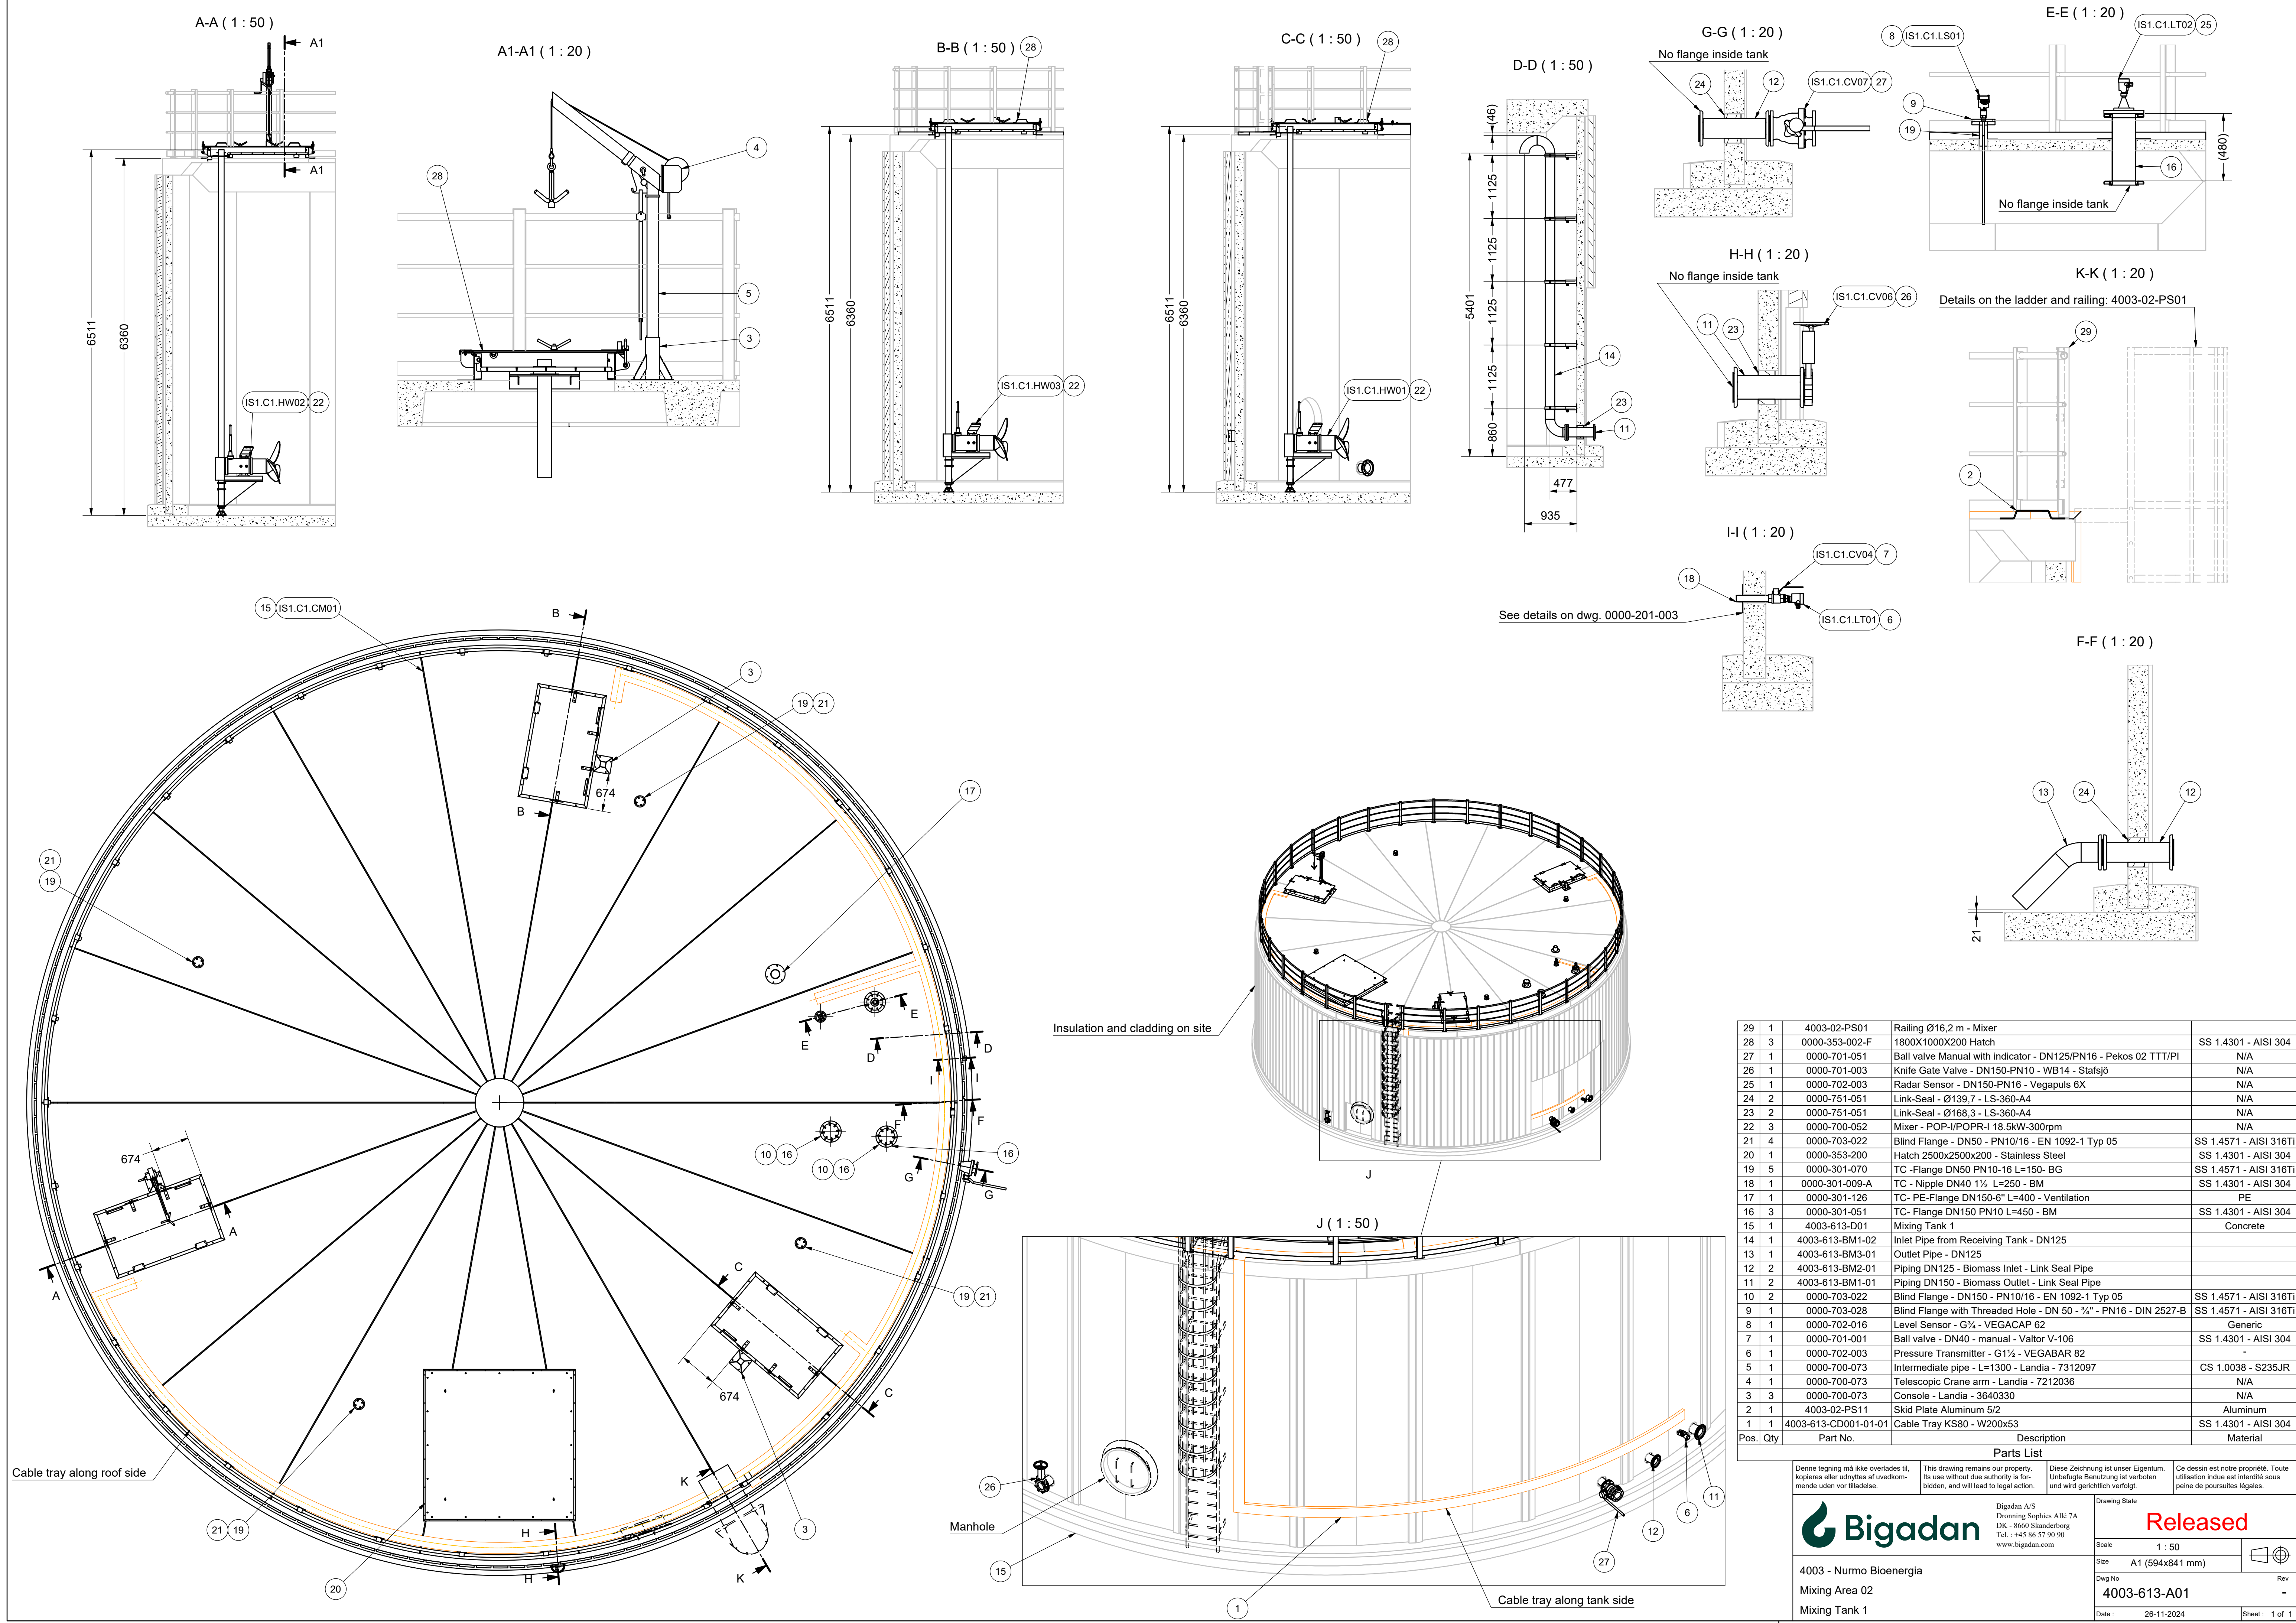

29	1	4003-02-PS01	Railing Ø16.2 m - Mixer	
28	3	0000-353-002-F	1800X1000X200 Hatch	SS 1.4301 - AISI 304
27	1	0000-701-051	Ball valve Manual with indicator - DN125/PN16 - Pekos 02 TTT/PI	N/A
26	1	0000-701-003	Knife Gate Valve - DN150-PN10 - WB14 - Stafsjö	N/A
25	1	0000-702-003	Radar Sensor - DN150-PN16 - Vegapuls 6X	N/A
24	2	0000-751-051	Link-Seal - Ø139.7 - LS-360-A4	N/A
23	2	0000-751-051	Link-Seal - Ø168.3 - LS-360-A4	N/A
22	3	0000-700-052	Mixer - POP-I/POPR-I 18.5kW-300rpm	N/A
21	4	0000-703-022	Blind Flange - DN50 - PN10/16 - EN 1092-1 Typ 05	SS 1.4571 - AISI 316Ti
20	1	0000-353-200	Hatch 2500x2500x200 - Stainless Steel	SS 1.4301 - AISI 304
19	5	0000-301-070	TC - Flange DN50 PN10-16 L=150- BG	SS 1.4571 - AISI 316Ti
18	1	0000-301-009-A	TC - Nipple DN40 1½ L=250 - BM	SS 1.4301 - AISI 304
17	1	0000-301-126	TC- PE-Flange DN150-6" L=400 - Ventilation	PE
16	3	0000-301-051	TC- Flange DN150 PN10 L=450 - BM	SS 1.4301 - AISI 304
15	1	4003-613-D01	Mixing Tank 1	Concrete
14	1	4003-613-BM1-02	Inlet Pipe from Receiving Tank - DN125	
13	1	4003-613-BM3-01	Outlet Pipe - DN125	
12	2	4003-613-BM2-01	Piping DN125 - Biomass Inlet - Link Seal Pipe	
11	2	4003-613-BM1-01	Piping DN150 - Biomass Outlet - Link Seal Pipe	
10	2	0000-703-022	Blind Flange - DN150 - PN10/16 - EN 1092-1 Typ 05	SS 1.4571 - AISI 316Ti
9	1	0000-703-028	Blind Flange with Threaded Hole - DN 50 - ¾" - PN16 - DIN 2527-B	SS 1.4571 - AISI 316Ti
8	1	0000-702-016	Level Sensor - G¾ - VEGACAP 62	Generic
7	1	0000-701-001	Ball valve - DN40 - manual - Valtor V-106	SS 1.4301 - AISI 304
6	1	0000-702-003	Pressure Transmitter - G1½ - VEGABAR 82	-
5	1	0000-700-073	Intermediate pipe - L=1300 - Landia - 7312097	CS 1.0038 - S235JR
4	1	0000-700-073	Telescopic Crane arm - Landia - 7212036	N/A
3	3	0000-700-073	Console - Landia - 3640330	N/A
2	1	4003-02-PS11	Skid Plate Aluminum 5/2	Aluminum
1	1	4003-613-CD001-01-01	Cable Tray KS80 - W200x53	SS 1.4301 - AISI 304
Pos.	Qty	Part No.	Description	Material
Parts List				
Denne tegning må ikke overlades til, kopieres eller udtrykkes af uvedkom- mende uden vor tilladelse.				
This drawing remains our property. Its use without due authority is for- bidden, and will lead to legal action.				
Diese Zeichnung ist unser Eigentum. Unbefugte Benutzung ist verboten und wird gerichtlich verfolgt.				
Ce dessin est notre propriété. Toute utilisation indue est interdite sous peine de poursuites légales.				
Bigadan A/S Dronning Sophies Allé 7A DK - 8660 Skanderborg Tel. : +45 86 57 90 90 www.bigadan.com			Drawing State Released	
4003 - Nurmo Bioenergia Mixing Area 02 Mixing Tank 1			Scale 1 : 50 Size A1 (594x841 mm)	Rev -
Dwg No 4003-613-A01			Date : 26-11-2024	Sheet : 1 of 1