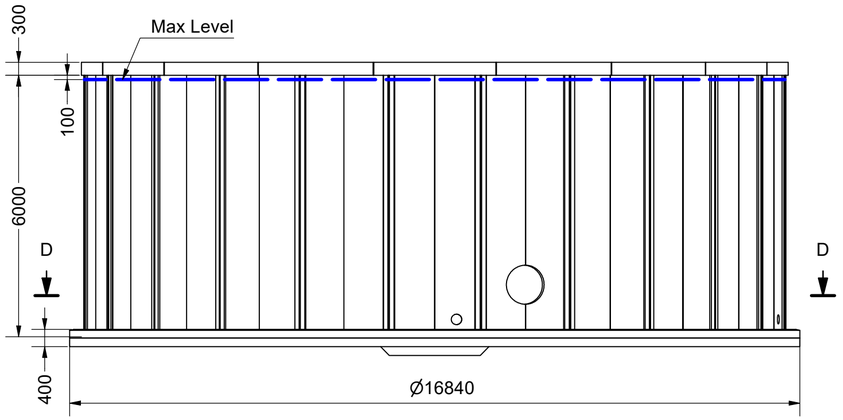

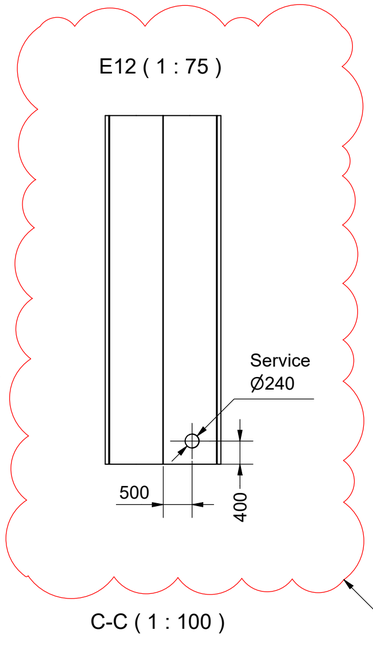

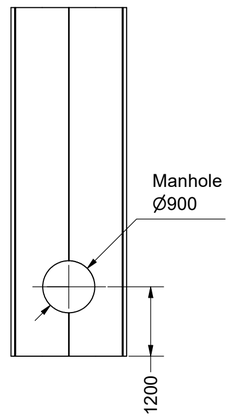

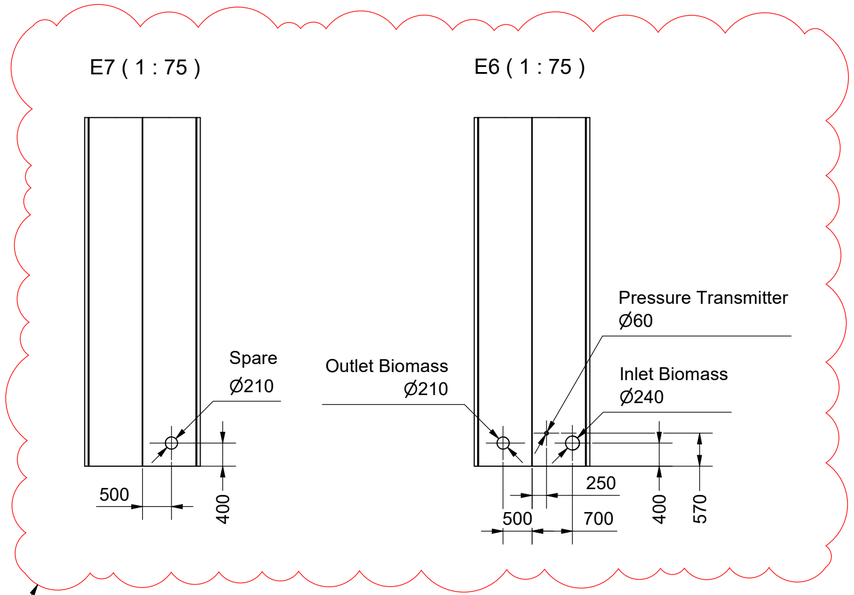

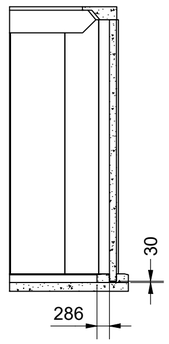

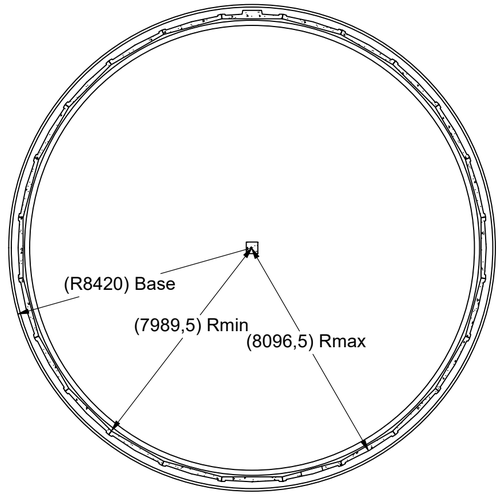

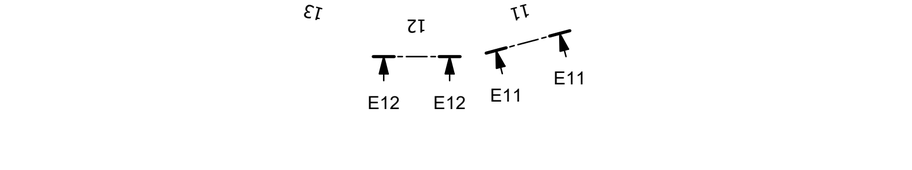

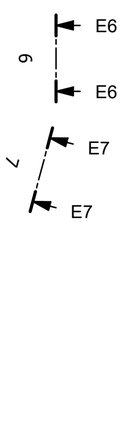

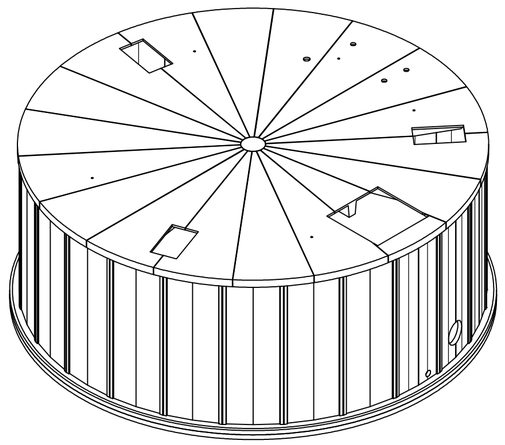

Note: All holes under Ø100 must be drilled on site

Rev	Date	Rev By	Description	Approved
B	19-09-2024	JCH	Added and changed hole sizes in concrete elements	JCH
A	09-09-2024	jsc	Added measure of holes	JLH
-	06-09-2024	jsc	First release	JLH

Revision History

Denne tegning må ikke overlades til, kopieres eller udnyttes af uvedkommende uden vor tilladelse.

This drawing remains our property. Its use without due authority is forbidden, and will lead to legal action.

Diese Zeichnung ist unser Eigentum. Unbefugte Benutzung ist verboten und wird gerichtlich verfolgt.

Ce dessin est notre propriété. Toute utilisation indue est interdité sous peine de poursuites légales.

Bigadan

Bigadan A/S
Vroldvej 168
DK - 8660 Skanderborg
Tel. : +45 86 57 90 90
www.bigadan.com

Drawing State: Released

4003 - Nurmo Bioenergia

Area 02 - Mixing Area

Mixing Tank 1

Scale: 1 : 100

Size: A2 (420x594 mm)

Dwg No: 4003-613-D01

Rev: A

Date : 31-08-2023

Sheet : 1 of 1