

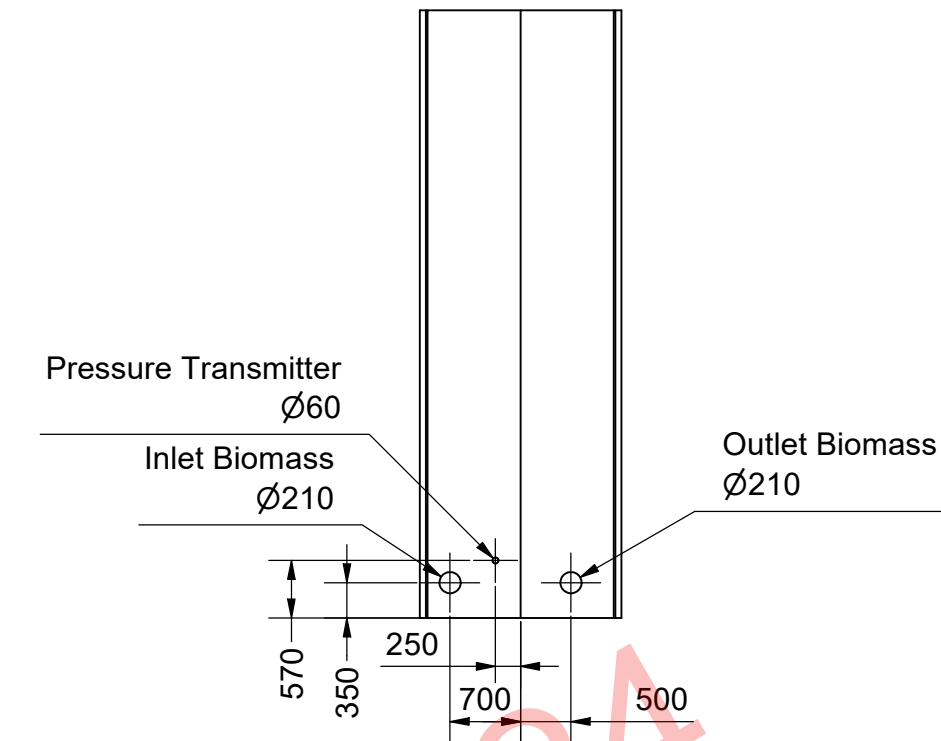


E13-E13 (1 : 75)




E18 (1 : 75)

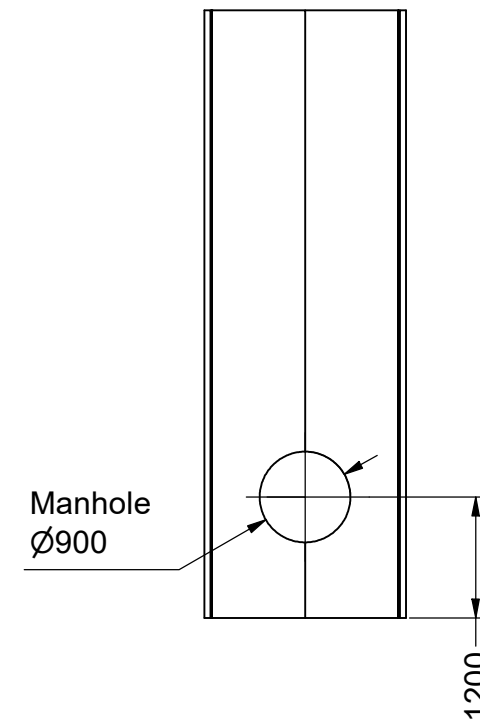

C-C (1 : 100)

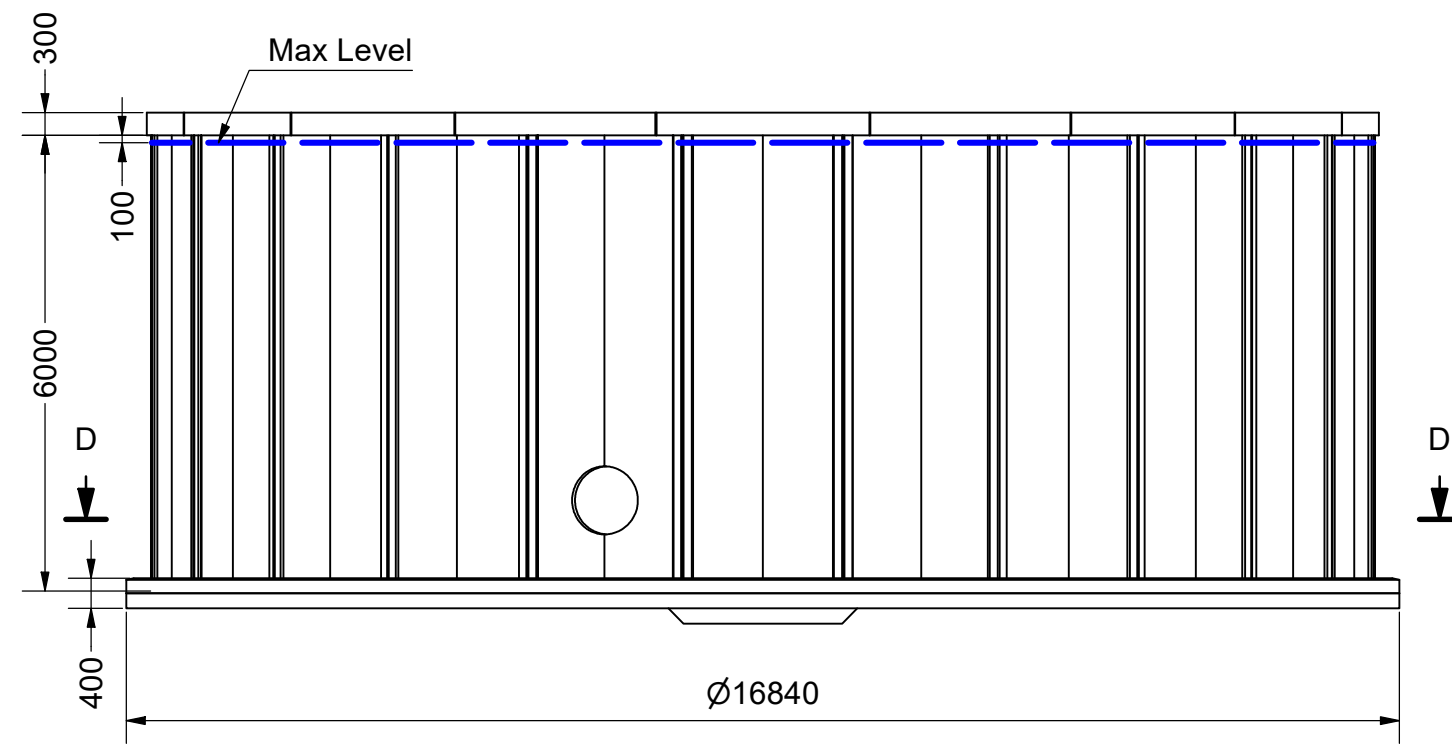

D-D (1 : 150)

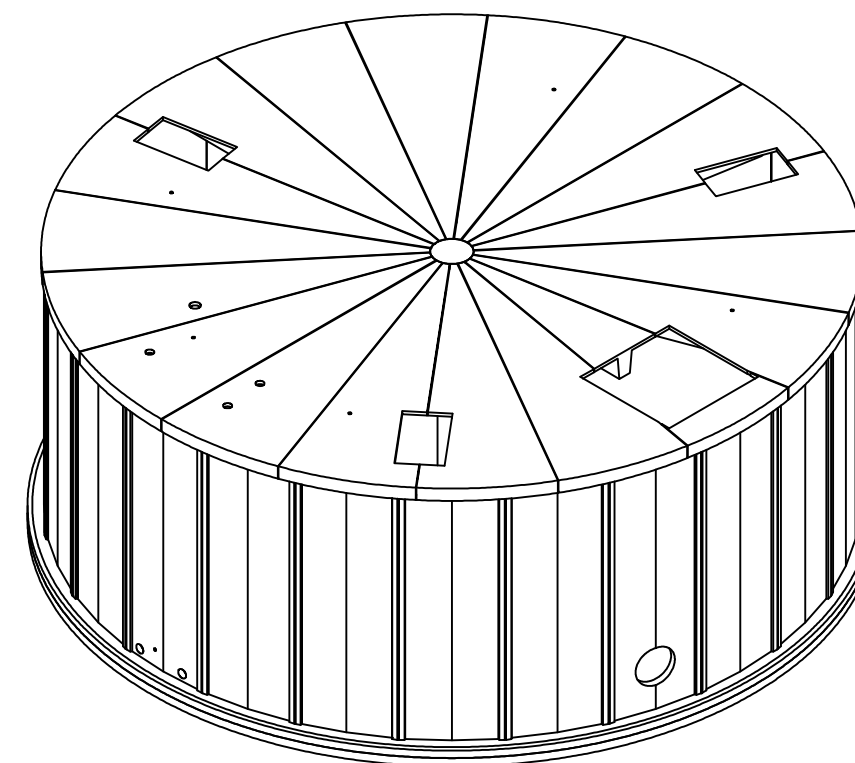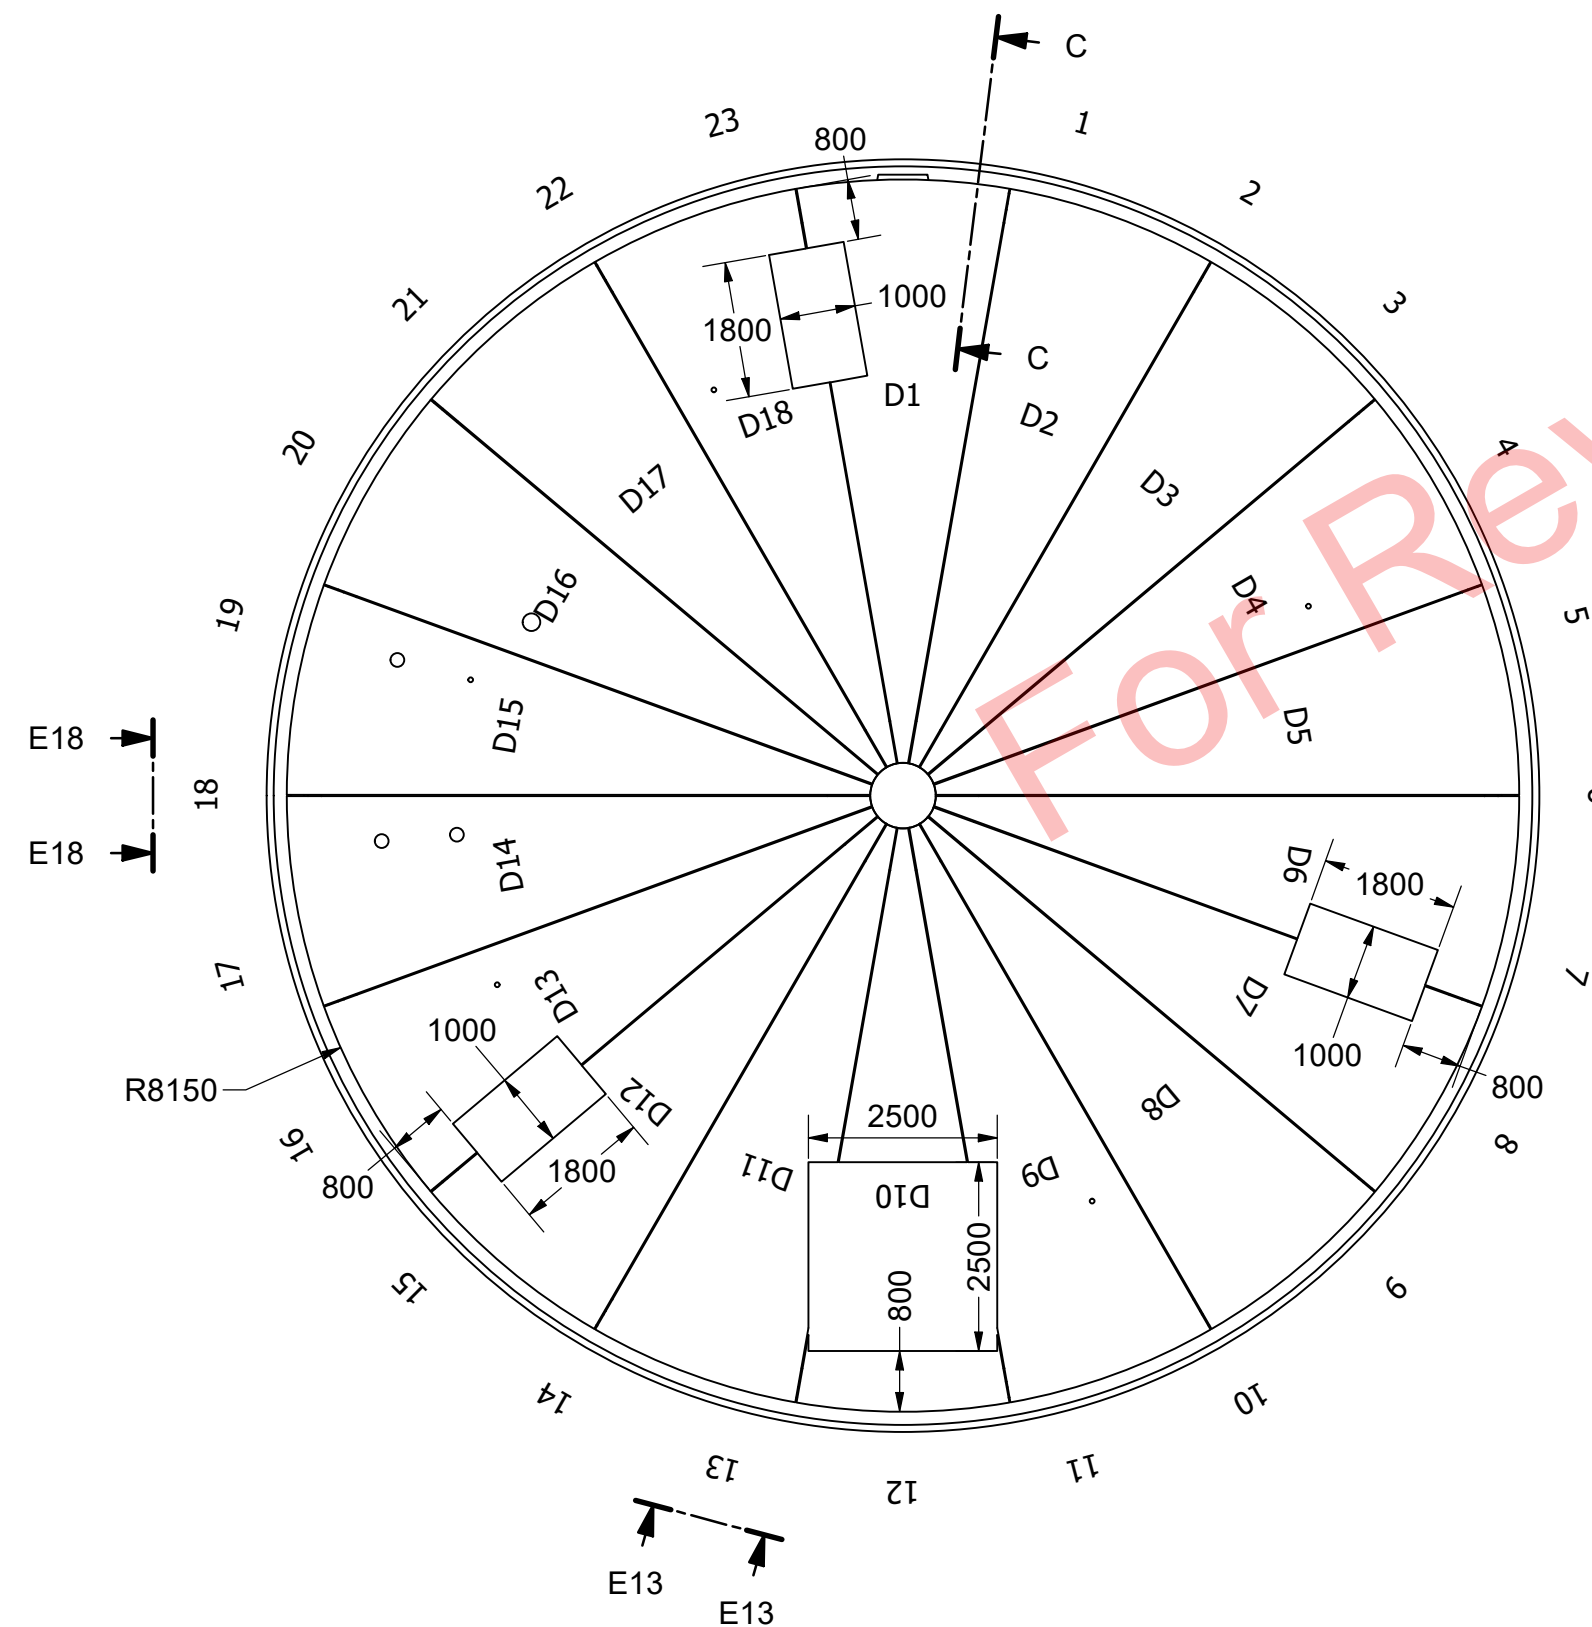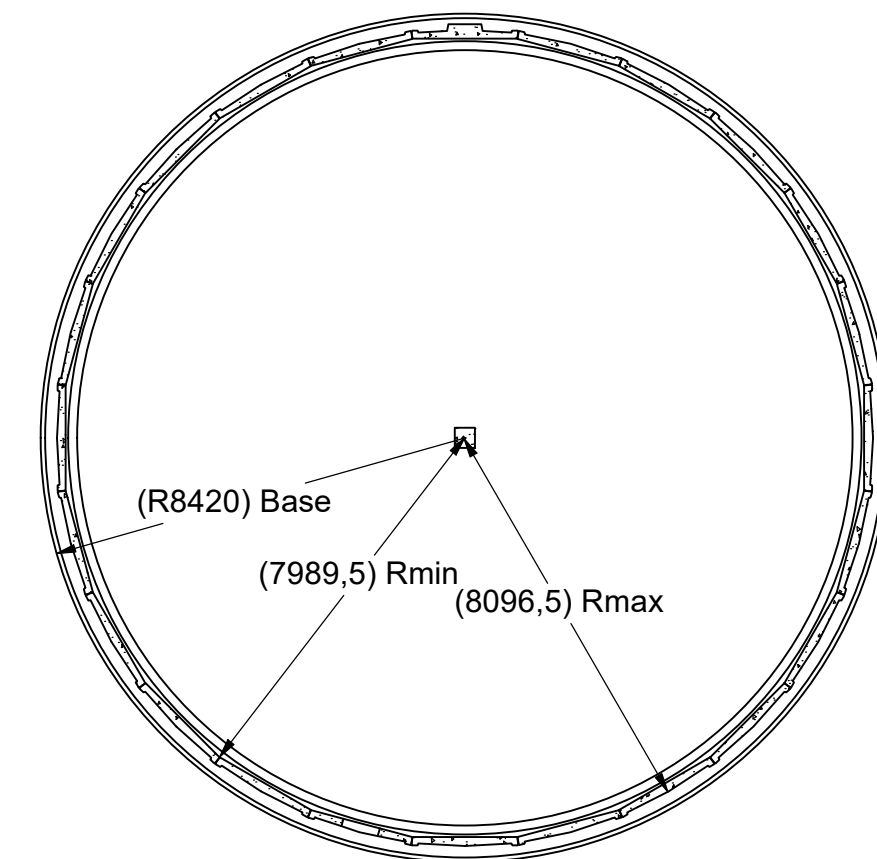

Note: All holes under Ø100 must be drilled on site

Denne tegning må ikke overlades til, kopieres eller udnyttes af uvedkommende uden vor tilladelse.		This drawing remains our property. Its use without due authority is forbidden, and will lead to legal action.		Diese Zeichnung ist unser Eigentum. Unbefugte Benutzung ist verboten und wird gerichtlich verfolgt.		Ce dessin est notre propriété. Toute utilisation induite est interdite sous peine de poursuites légales.			
 Bigadan Bigadan A/S Vroldvej 168 DK - 8660 Skanderborg Tel. : +45 86 57 90 90 www.bigadan.com				Drawing State					
				For Review					
				Scale		1 : 100			
				Size		A2 (420x594 mm)			
4003 - Nurmo Bioenergia				Dwg No		Rev			
Area 02 - Mixing Area				4003-613-D02		-			
Mixing Tank 2				Date : 31-08-2023		Sheet : 1 of 1			