


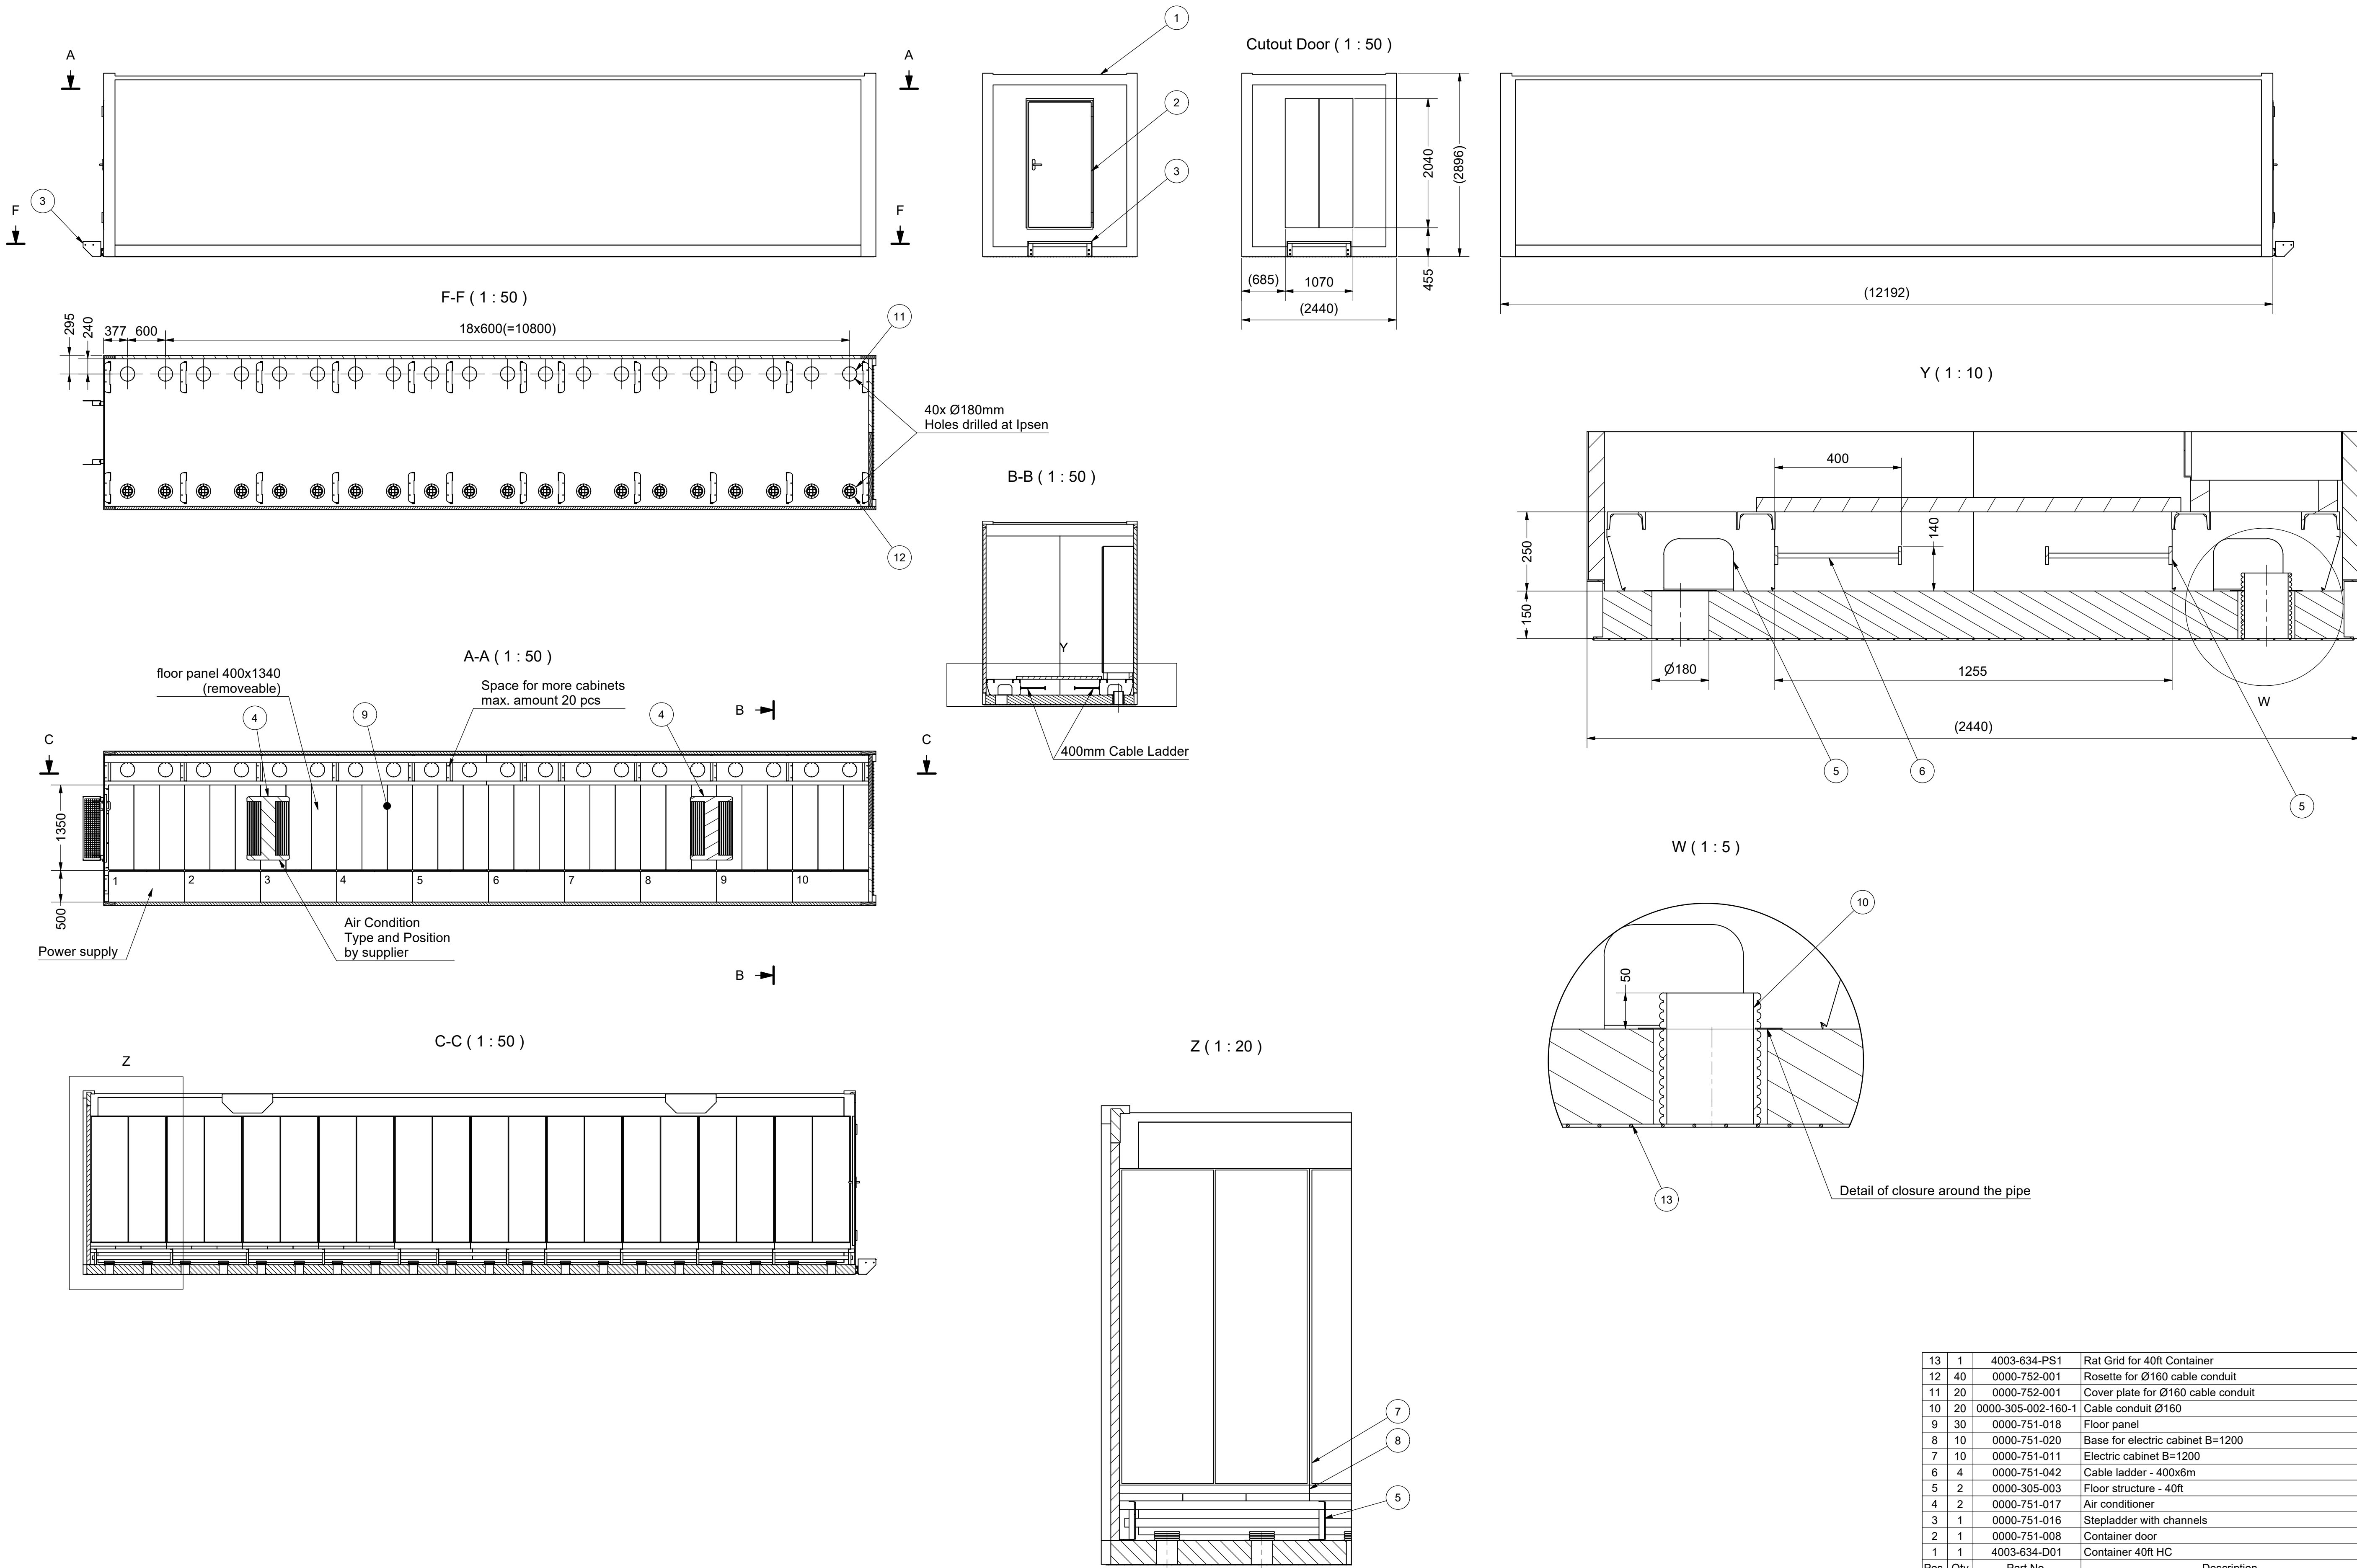

Field 1: Input
Field 2:
Field 3:
Field 4:
Field 5:
Field 6:
Field 7:
Field 8:
Field 9:
Field 10:

13	1	4003-634-PS1	Rat Grid for 40ft Container	Steel, Galv.
12	40	0000-752-001	Rosette for Ø160 cable conduit	SS 1.4301 - AISI 304
11	20	0000-752-001	Cover plate for Ø160 cable conduit	SS 1.4301 - AISI 304
10	20	0000-305-002-160-1	Cable conduit Ø160	PE
9	30	0000-751-018	Floor panel	Aluminum
8	10	0000-751-020	Base for electric cabinet B=1200	Steel, Galvanized
7	10	0000-751-011	Electric cabinet B=1200	-
6	4	0000-751-042	Cable ladder - 400x8m	Steel, Galvanized
5	2	0000-305-003	Floor structure - 40ft	Steel
4	2	0000-751-017	Air conditioner	-
3	1	0000-751-016	Stepladder with channels	Aluminum
2	1	0000-751-008	Container door	-
1	1	4003-634-D01	Container 40ft HC	-
Pos.	Qty	Part No.	Description	Material
Parts List				
Denne tegning må ikke overføres til, kopieres eller udrykkes af uvedkom-mende uden vor tilladelse.				
This drawing remains our property. Its use without due authority is for-bidden, and will lead to legal action.				
Diese Zeichnung ist unser Eigentum. Unbefugte Benutzung ist verboten und wird gerichtlich verfolgt.				
Ce dessin est notre propriété. Toute utilisation indue est interdite sous peine de poursuites légales.				
Bigadan A/S Vroldvej 168 DK - 8660 Skanderborg Tel. : +45 86 57 90 90 www.bigadan.com				
Tag no.				
Engineer / Assistant				
Scale				
Size				
Dwg No				
Rev				
Basic Design				
Electric Container 40ft HC				
4003-634-A01				
Date : 15-03-2021				
Sheet : 1 of 1				