

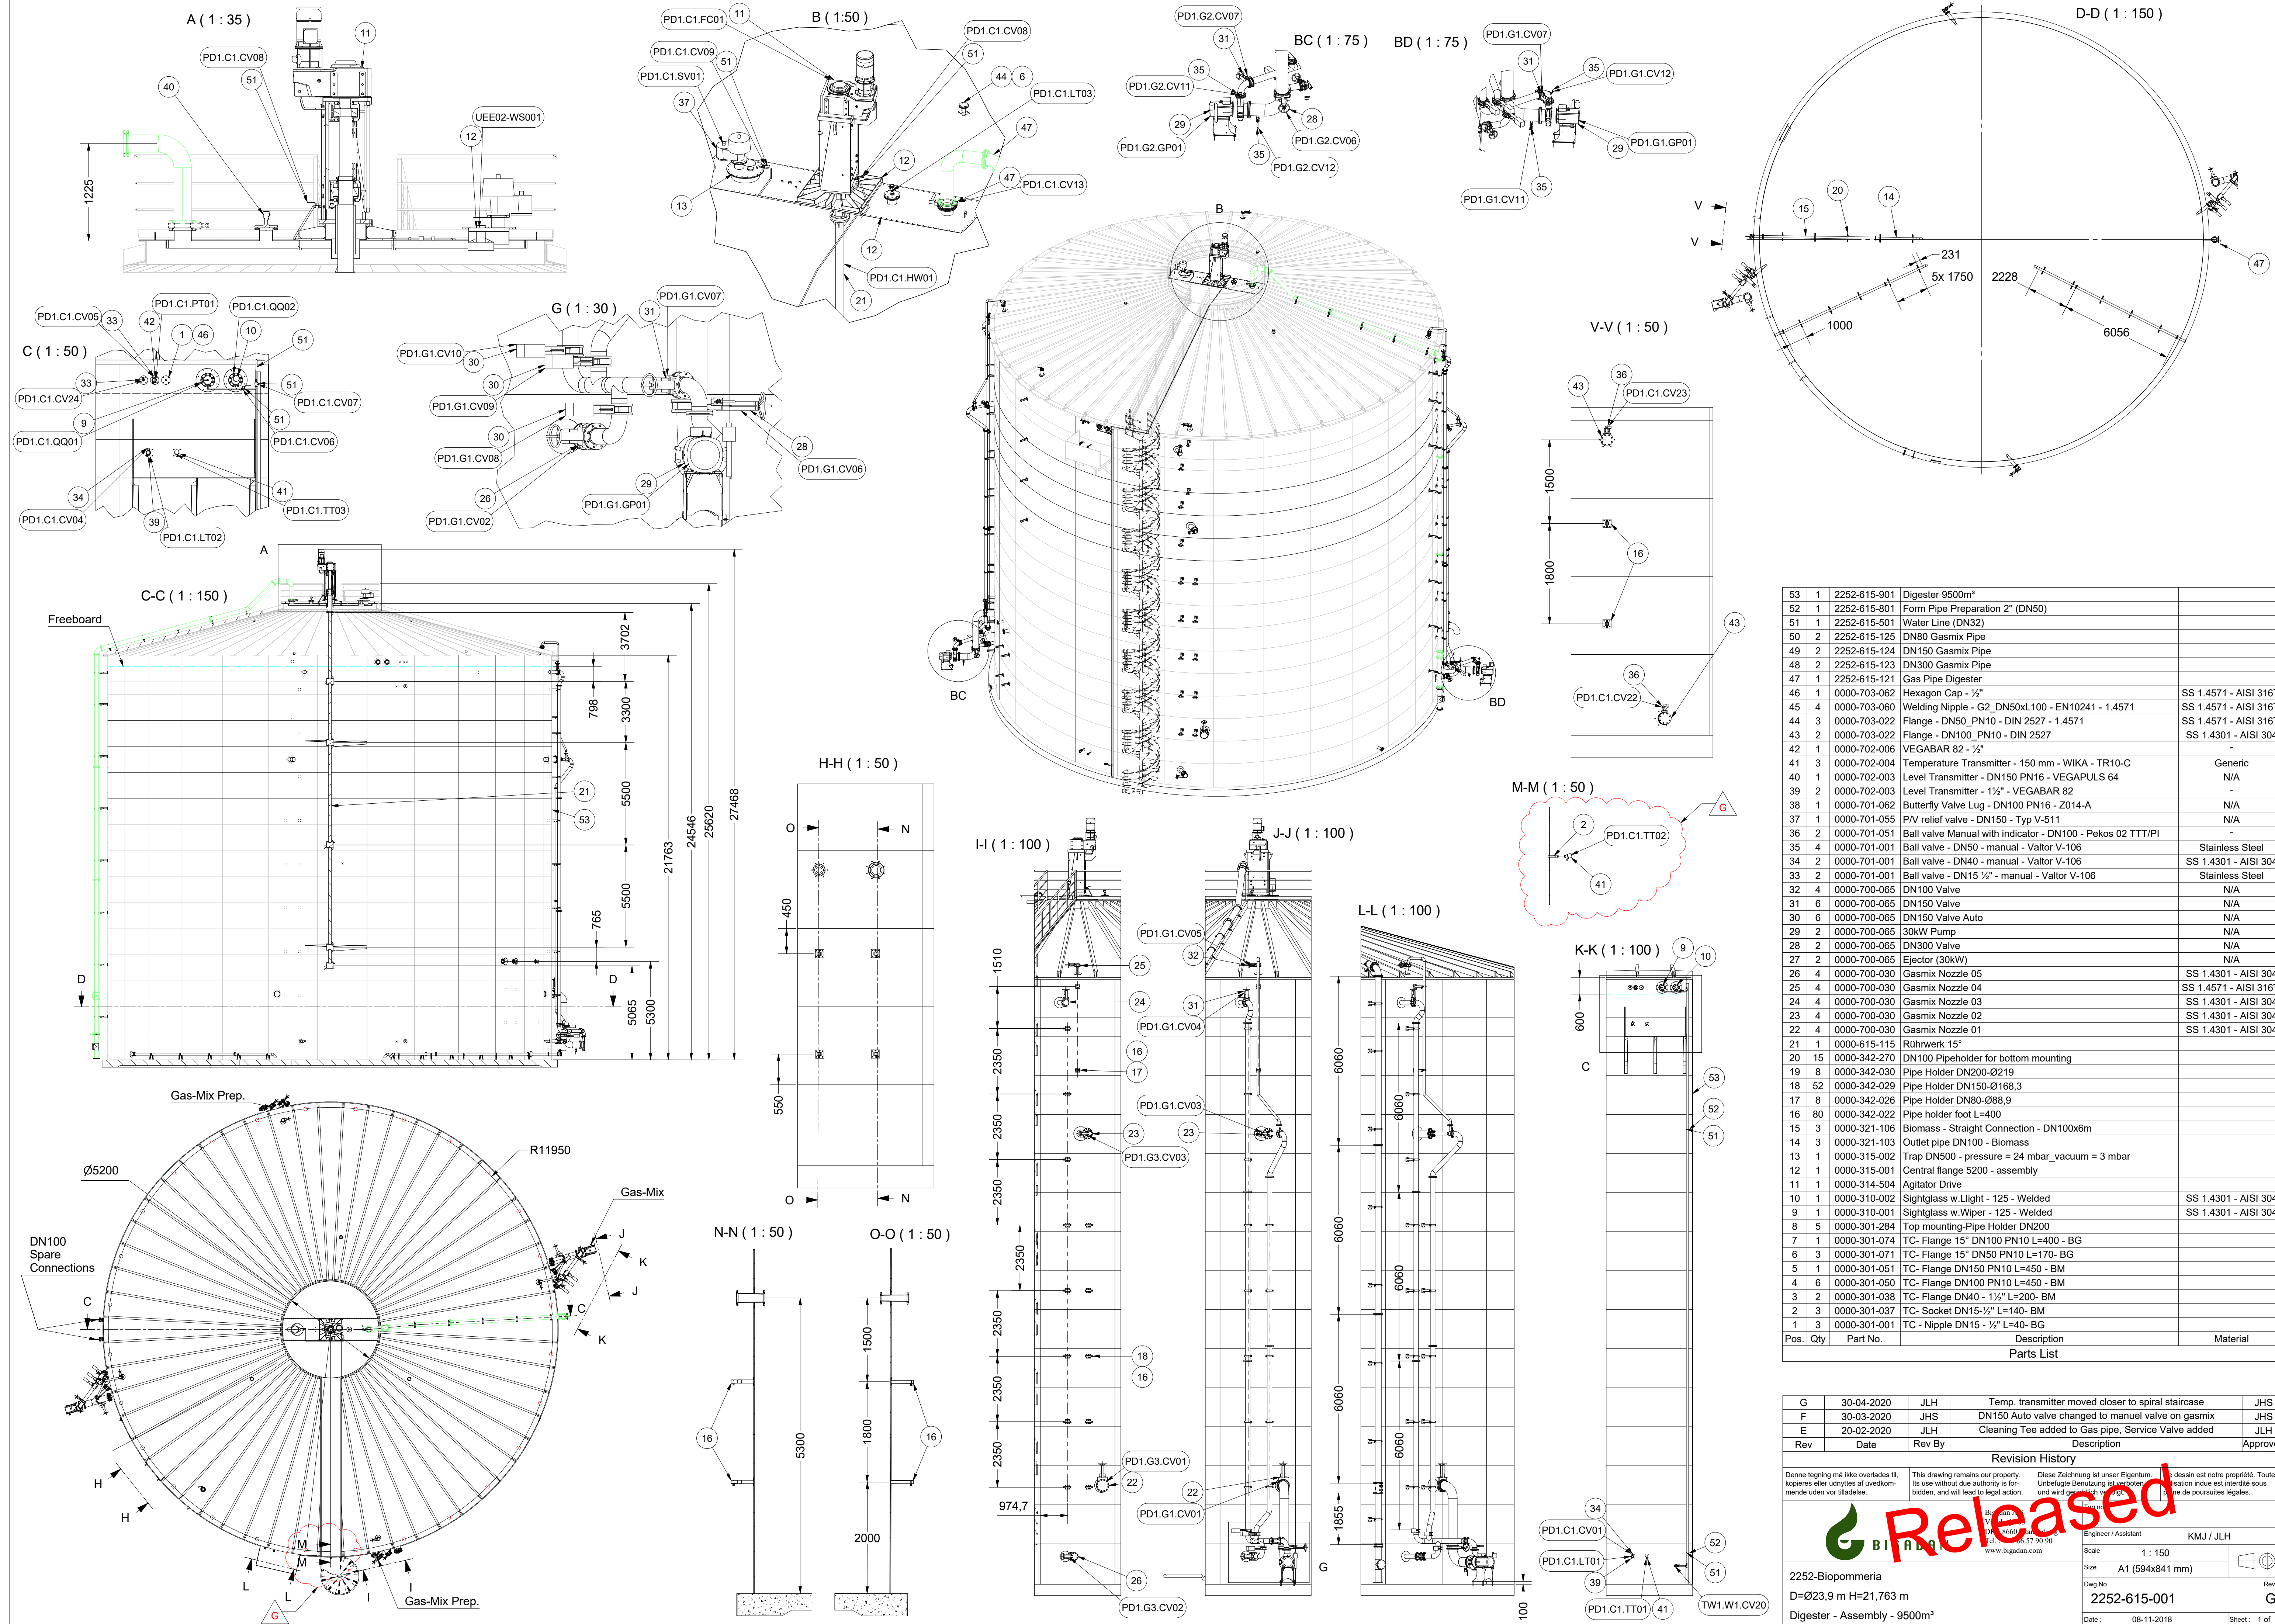


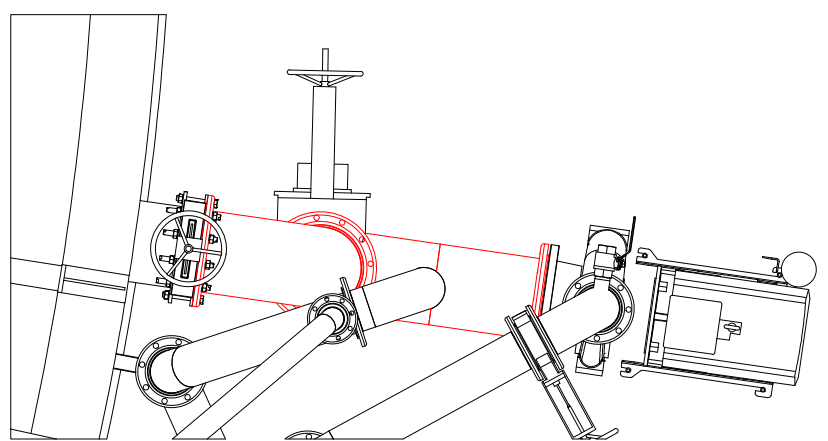



53	1	2252-615-901	Digester 9500m³		
52	1	2252-615-901	Form Pipe Preparation 2" (DN50)		
51	1	2252-615-501	Water Line (DN32)		
50	2	2252-615-125	DN80 Gasmix Pipe		
49	2	2252-615-124	DN150 Gasmix Pipe		
48	2	2252-615-123	DN300 Gasmix Pipe		
47	1	2252-615-121	Gas Pipe Digester		
46	1	0000-703-062	Hexagon Cap - 1/2"		SS 1.4571 - AISI 316Ti
45	4	0000-703-060	Welding Nipple - G2 DN50xL100 - EN10241 - 1.4571		SS 1.4571 - AISI 316Ti
44	3	0000-703-022	Flange - DN50 PN10 - DIN 2527 - 1.4571		SS 1.4571 - AISI 316Ti
43	2	0000-703-022	Flange - DN100 PN10 - DIN 2527		SS 1.4301 - AISI 304
42	1	0000-702-006	VEGABAR 82 - 1/2"		-
41	3	0000-702-004	Temperature Transmitter - 150 mm - WIKA - TR10-C		Generic
40	1	0000-702-003	Level Transmitter - DN150 PN16 - VEGAPULS 64		N/A
39	2	0000-702-003	Level Transmitter - 1 1/2" - VEGABAR 82		-
38	1	0000-701-062	Butterfly Valve Lug - DN100 PN16 - Z014-A		N/A
37	1	0000-701-055	P/V relief valve - DN150 - Typ V-511		N/A
36	2	0000-701-051	Ball valve Manual with indicator - DN100 - Pekos 02 TTT/PI		-
35	4	0000-701-001	Ball valve - DN50 - manual - Valtor V-106		Stainless Steel
34	2	0000-701-001	Ball valve - DN40 - manual - Valtor V-106		SS 1.4301 - AISI 304
33	2	0000-701-001	Ball valve - DN15 1/2" - manual - Valtor V-106		Stainless Steel
32	4	0000-700-065	DN100 Valve		N/A
31	6	0000-700-065	DN150 Valve		N/A
30	6	0000-700-065	DN150 Valve Auto		N/A
29	2	0000-700-065	30kW Pump		N/A
28	2	0000-700-065	DN300 Valve		N/A
27	2	0000-700-065	Ejector (30kW)		N/A
26	4	0000-700-030	Gasmix Nozzle 05		SS 1.4301 - AISI 304
25	4	0000-700-030	Gasmix Nozzle 04		SS 1.4571 - AISI 316Ti
24	4	0000-700-030	Gasmix Nozzle 03		SS 1.4301 - AISI 304
23	4	0000-700-030	Gasmix Nozzle 02		SS 1.4301 - AISI 304
22	4	0000-700-030	Gasmix Nozzle 01		SS 1.4301 - AISI 304
21	1	0000-615-115	Rührwerk 15°		
20	15	0000-342-270	DN100 Pipeholder for bottom mounting		
19	8	0000-342-030	Pipe Holder DN200-Ø219		
18	52	0000-342-029	Pipe Holder DN150-Ø168.3		
17	8	0000-342-026	Pipe Holder DN80-Ø88.9		
16	80	0000-342-022	Pipe holder foot L=400		
15	3	0000-321-106	Biomass - Straight Connection - DN100x6m		
14	3	0000-321-103	Outlet pipe DN100 - Biomass		
13	1	0000-315-002	Trap DN500 - pressure = 24 mbar_vacuum = 3 mbar		
12	1	0000-315-001	Central flange 5200 - assembly		
11	1	0000-314-504	Agitator Drive		
10	1	0000-310-002	Sightglass w.Light - 125 - Welded		SS 1.4301 - AISI 304
9	1	0000-310-001	Sightglass w.Wiper - 125 - Welded		SS 1.4301 - AISI 304
8	5	0000-301-284	Top mounting-Pipe Holder DN200		
7	1	0000-301-074	TC- Flange 15" DN100 PN10 L=400 - BG		
6	3	0000-301-071	TC- Flange 15" DN50 PN10 L=170- BG		
5	1	0000-301-051	TC- Flange DN150 PN10 L=450 - BM		
4	6	0000-301-050	TC- Flange DN100 PN10 L=450 - BM		
3	2	0000-301-038	TC- Flange DN40 - 1 1/2" L=200- BM		
2	3	0000-301-037	TC- Socket DN15-1/2" L=140- BM		
1	3	0000-301-001	TC - Nipple DN15 - 1/2" L=40- BG		
Pos.	Qty	Part No.	Description	Material	

G	30-04-2020	JLH	Temp. transmitter moved closer to spiral staircase	JHS
F	30-03-2020	JHS	DN150 Auto valve changed to manual valve on gasmix	JHS
E	20-02-2020	JLH	Cleaning Tee added to Gas pipe, Service Valve added	JLH
Rev	Date	Rev By	Description	Approved
Revision History				
Denne tegning må ikke overføres til kopieres eller udrykkes af uvedkommende uden vor tilladelse.				
This drawing remains our property. Its use without due authority is forbidden, and will lead to legal action.				
Diese Zeichnung ist unser Eigentum. Ihre unbefugte Benutzung ist verboten und wird gesetzlich verfolgt.				
Ces dessin est notre propriété. Toute utilisation induite est interdite sous peine de poursuites légales.				
Biomass Vejle 8660 57 90 90 www.biogdan.com				
Engineer / Assistant			KMJ / JLH	
Scale			1 : 150	
Size			A1 (594x841 mm)	
Dwg No			2252-615-001	
2252-Biopommeria			Rev	
D=Ø23.9 m H=21,763 m			G	
Digester - Assembly - 9500m³			Date : 08-11-2018	
			Sheet : 1 of 2	



A technical drawing of a vertical pipe assembly. The drawing shows a vertical pipe with various fittings, valves, and a horizontal branch. A red line highlights a specific section of the pipe, starting from a horizontal branch at the bottom, going up, and then curving to the right to connect to a horizontal pipe. The drawing is a line drawing with no shading.

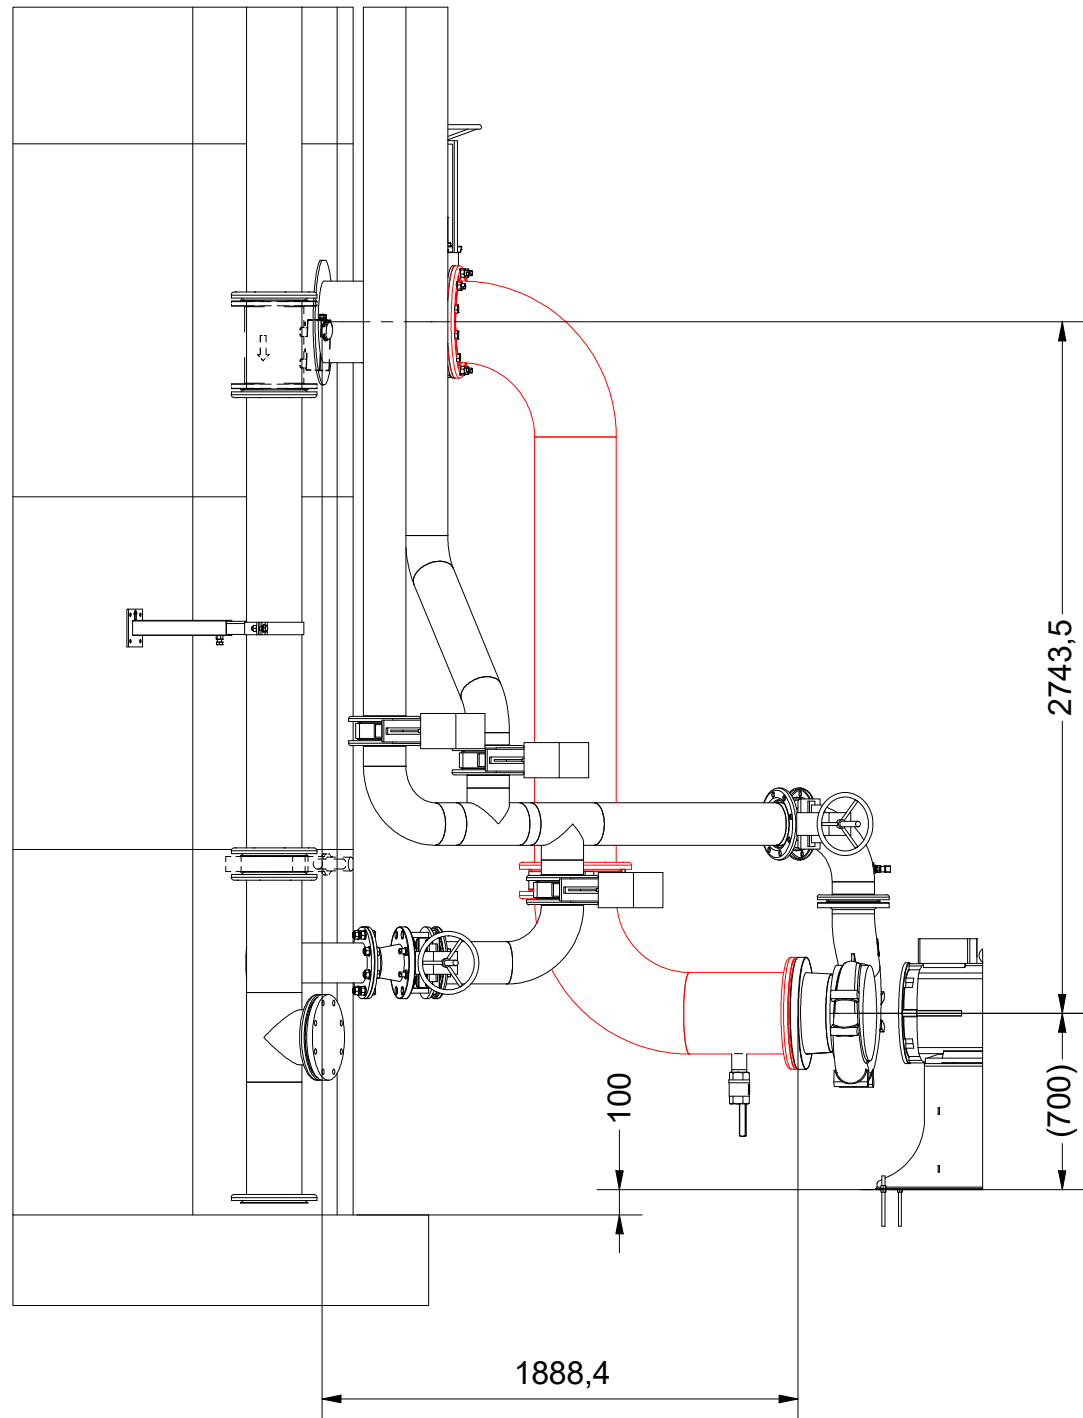

1	1	0000-703-001	Pipe - DN300-Ø323,9x3,0 L=2140 - EN10217-7	SS 1.4301 - AISI 304
4	2	0000-703-030	Elbow 90° DN300 Ø323,9x6,3 - Type 3 R=450 DN12605 - 1.4301	SS 1.4301 - AISI 304
3	4	0000-703-020	Pressed Flange - DN300 PN10 - EN 1092-1 Typ 02	SS 1.4301 - AISI 304
2	4	0000-703-010	Collar DN300 - PN10 EN 1092-1 Typ 37 - 1.4301	SS 1.4301 - AISI 304
Pos.	Qty	Part No.	Description	Material
Parts List For 1x - 2252-615-123				

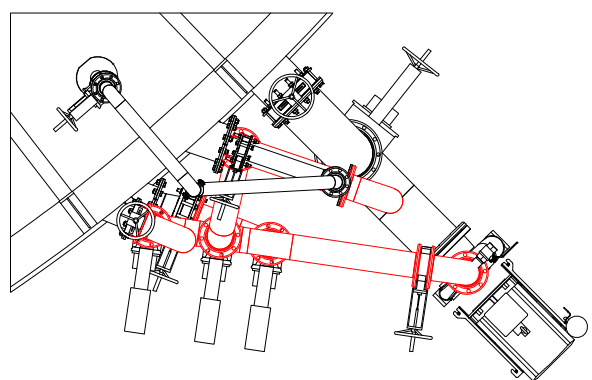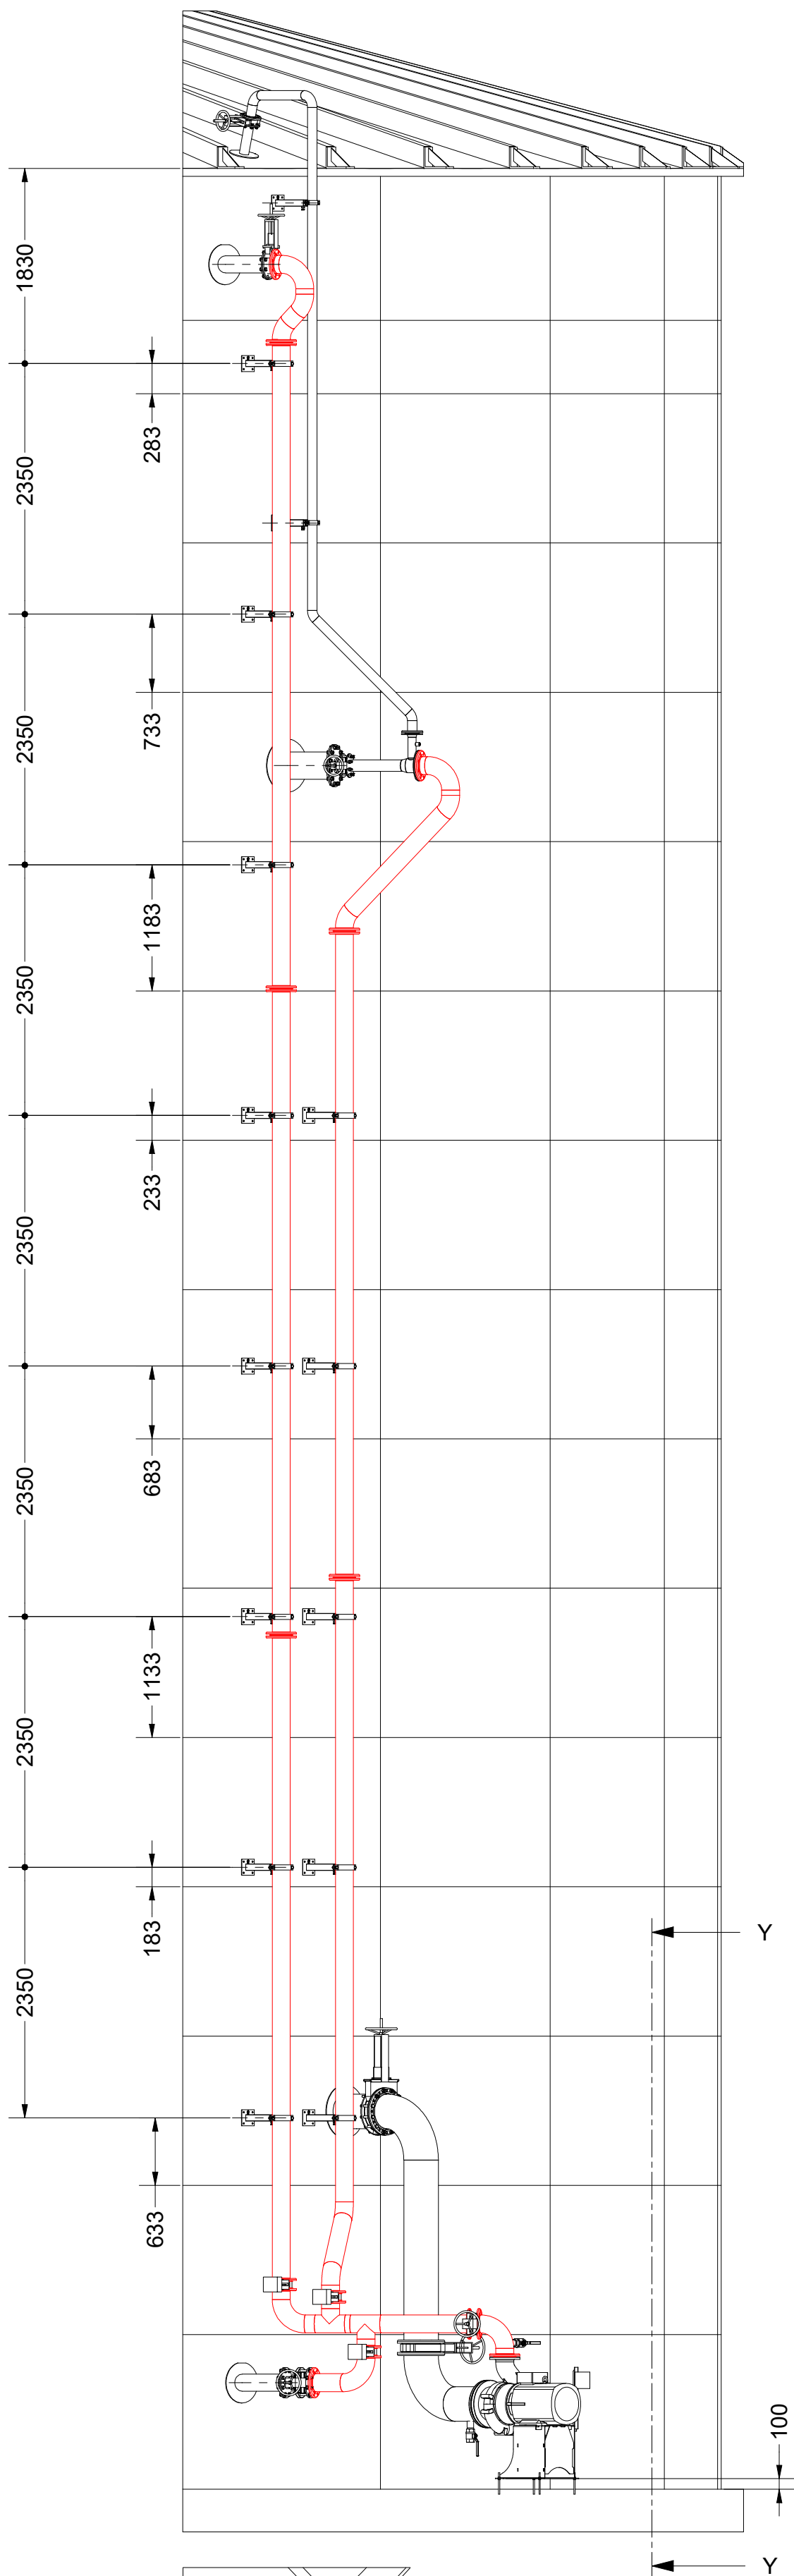

6	1	0000-703-001	Pipe - DN150-Ø168,3x2,6 - L=35268 - EN10217-7	SS 1.4301 - AISI 304
5	2	0000-703-040	Tee Equal - DN150 Ø168,3x2,6 - EN10523-4	SS 1.4301 - AISI 304
4	6	0000-703-030	Elbow 45° DN150-Ø168,3x2,6 - Type 2 =R229 - DIN2605	SS 1.4301 - AISI 304
3	5	0000-703-030	Elbow 90° DN150 Ø168,3x2,6 - Type 3 =r229 - DIN2605	SS 1.4301 - AISI 304
2	22	0000-703-020	Pressed Flange - DN150 PN10 - EN 10921 Typ 02	SS 1.4301 - AISI 304
1	22	0000-703-010	Collar - DN150 PN10 - EN 1092-1 Typ 137	SS 1.4301 - AISI 304
Pos.	Qty	Part No.	Description	Material
Parts List For 1x 2252-615-124				

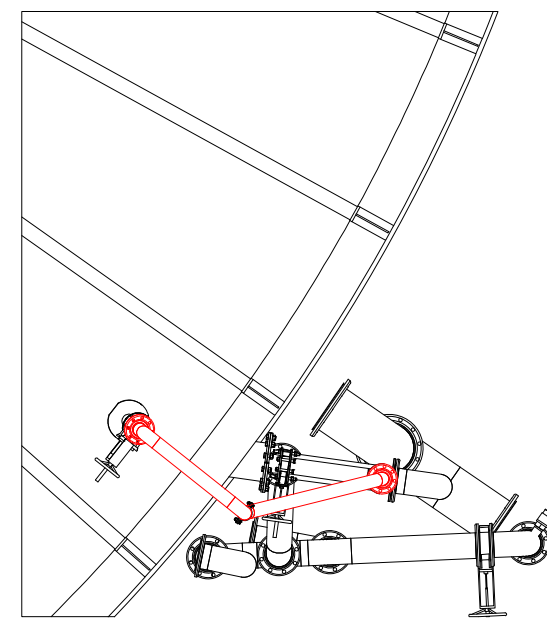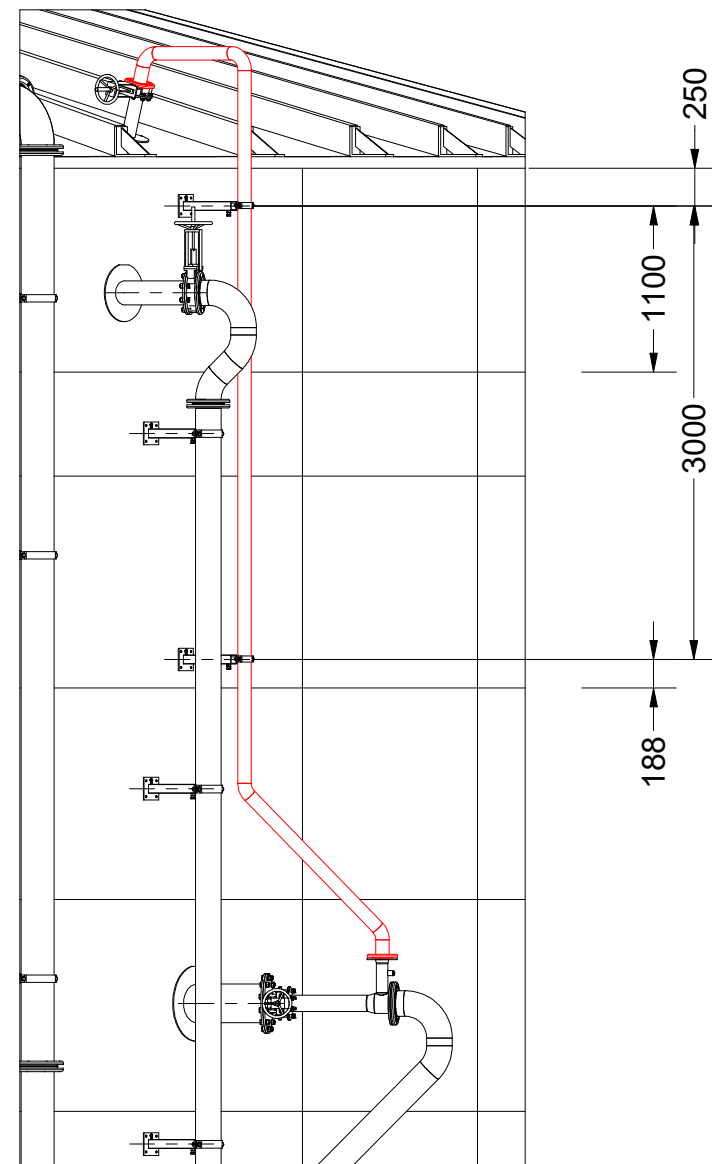

1	2	0000-703-001	Pipe - DN80-Ø88,9x2,6 L=7114 - EN10217-2	SS 1.4301 - AISI 304
1	2	0000-703-030	Elbow 45° DN80 Ø88,9x2,6 - Type 3 R=114 - DIN2605	SS 1.4301 - AISI 304
4	2	0000-703-030	Elbow 90° DN80 Ø88,9x2 - Type 3 R=114 - DIN2605 - 1.4301	SS 1.4301 - AISI 304
3	2	0000-703-020	Pressed Flange - DN80 PN10 / EN 1092-1 Typ 02	SS 1.4301 - AISI 304
2	2	0000-703-010	Collar - DN80 PN10 - EN 1096-1 Typ 37	SS 1.4571 - AISI 316Ti
Pos.	Qty	Part No.	Description	Material

Parts List For 1x 2252-615-125

G	30-04-2020	JLH	Temp. transmitter moved closer to spiral staircase	JHS
F	30-03-2020	JHS	DN150 Auto valve changed to manuel valve on gasmix	JHS
E	20-02-2020	JLH	Cleaning Tee added to Gas pipe, Service Valve added	JLH
Rev	Date	Rev By	Description	Approved

Revision History				
Denne tegning må ikke overlades til, kopieres eller udnyttes af uvedkommende uden tilladelse.	This drawing remains our property. Its use without draws authority is forbidden, and will lead to legal action.	Diese Zeichnung ist unser Eigentum. Unbefugte Benutzung ist verboten und wird gesetzlich verfolgt.	Toute ébauche est notre propriété. Toute utilisation induite est interdite sous peine de poursuites légales.	



Bigan
 Industriepark
 D-86604 Gaißing
 Tel.: +49 89 57 90 90
www.bigan.com

2252-Biopommerria D=Ø23,9 m H=21,763 m Digester - Assembly - 9500m³	Engineer / Assistant	KMJ / JLH
	Scale	1 : 30
	Size	A1 (594x841 mm)
	Dwg No	2252-615-001
	Date	08-11-2018



G

Sheet : 2 of 2