


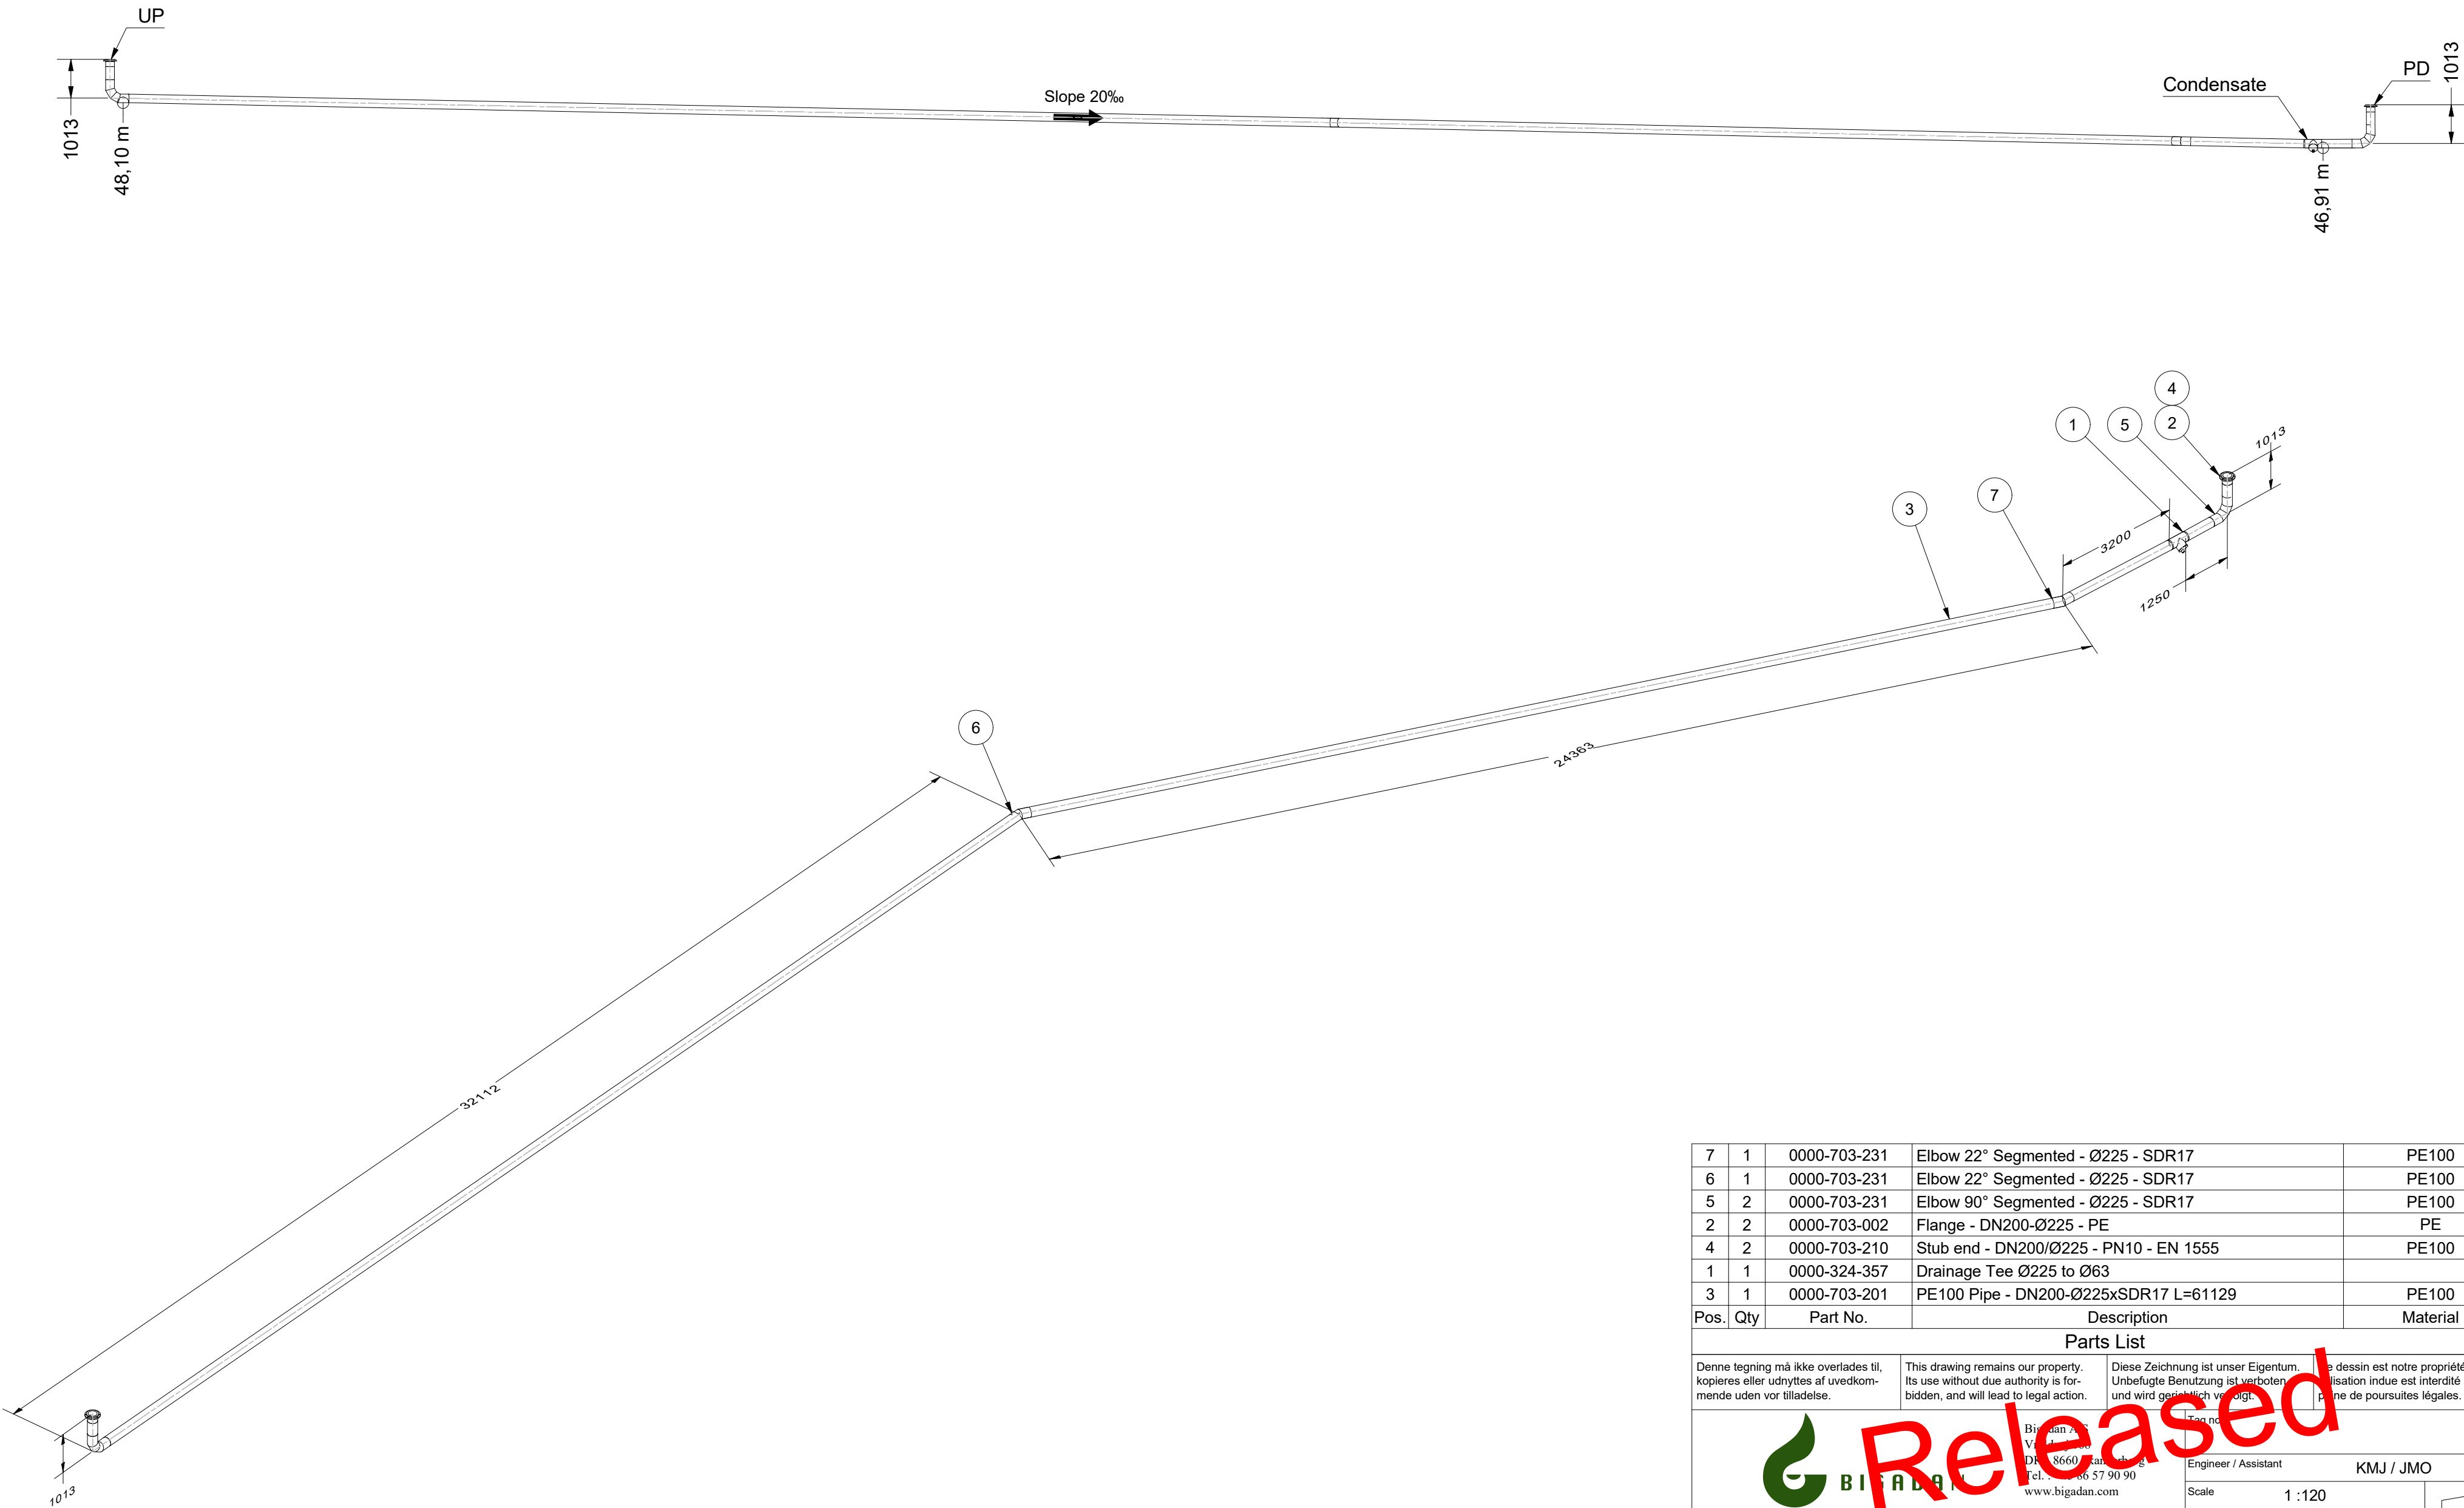

7	1	0000-703-231	Elbow 22° Segmented - Ø225 - SDR17	PE100
6	1	0000-703-231	Elbow 22° Segmented - Ø225 - SDR17	PE100
5	2	0000-703-231	Elbow 90° Segmented - Ø225 - SDR17	PE100
2	2	0000-703-002	Flange - DN200-Ø225 - PE	PE
4	2	0000-703-210	Stub end - DN200/Ø225 - PN10 - EN 1555	PE100
1	1	0000-324-357	Drainage Tee Ø225 to Ø63	
3	1	0000-703-201	PE100 Pipe - DN200-Ø225xSDR17 L=61129	PE100
Pos.	Qty	Part No.	Description	Material

Parts List

Denne tegning må ikke overlades til, kopieres eller udnyttes af uvedkommende uden vor tilladelse.

This drawing remains our property. Its use without due authority is forbidden, and will lead to legal action.

Diese Zeichnung ist unser Eigentum. Unbefugte Benutzung ist verboten und wird gesetzlich verfolgt.

Ce dessin est notre propriété. Toute utilisation induue est interdite sous peine de poursuites légales.



2252 - BioPommeria
Pipe In Ground
From PD To UP

Engineer / Assistant
Scale 1 : 120
Size A2 (420x594 mm)
Dwg No 2252-BG033-02
Date : 06-02-2020

KMJ / JMO
Rev -
Sheet : 1 of 1