


B

A-A ( 1 : 100 )

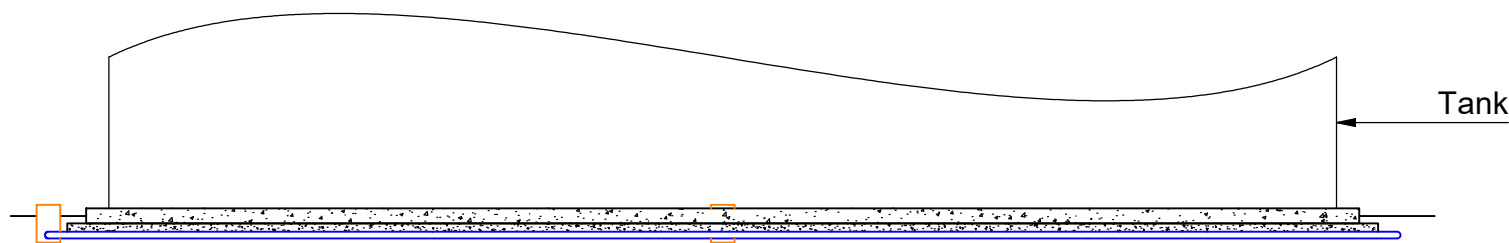

Tank



B ( 1 : 10 )

Tank Wall




Tank Wall

C ( 1 : 10 )

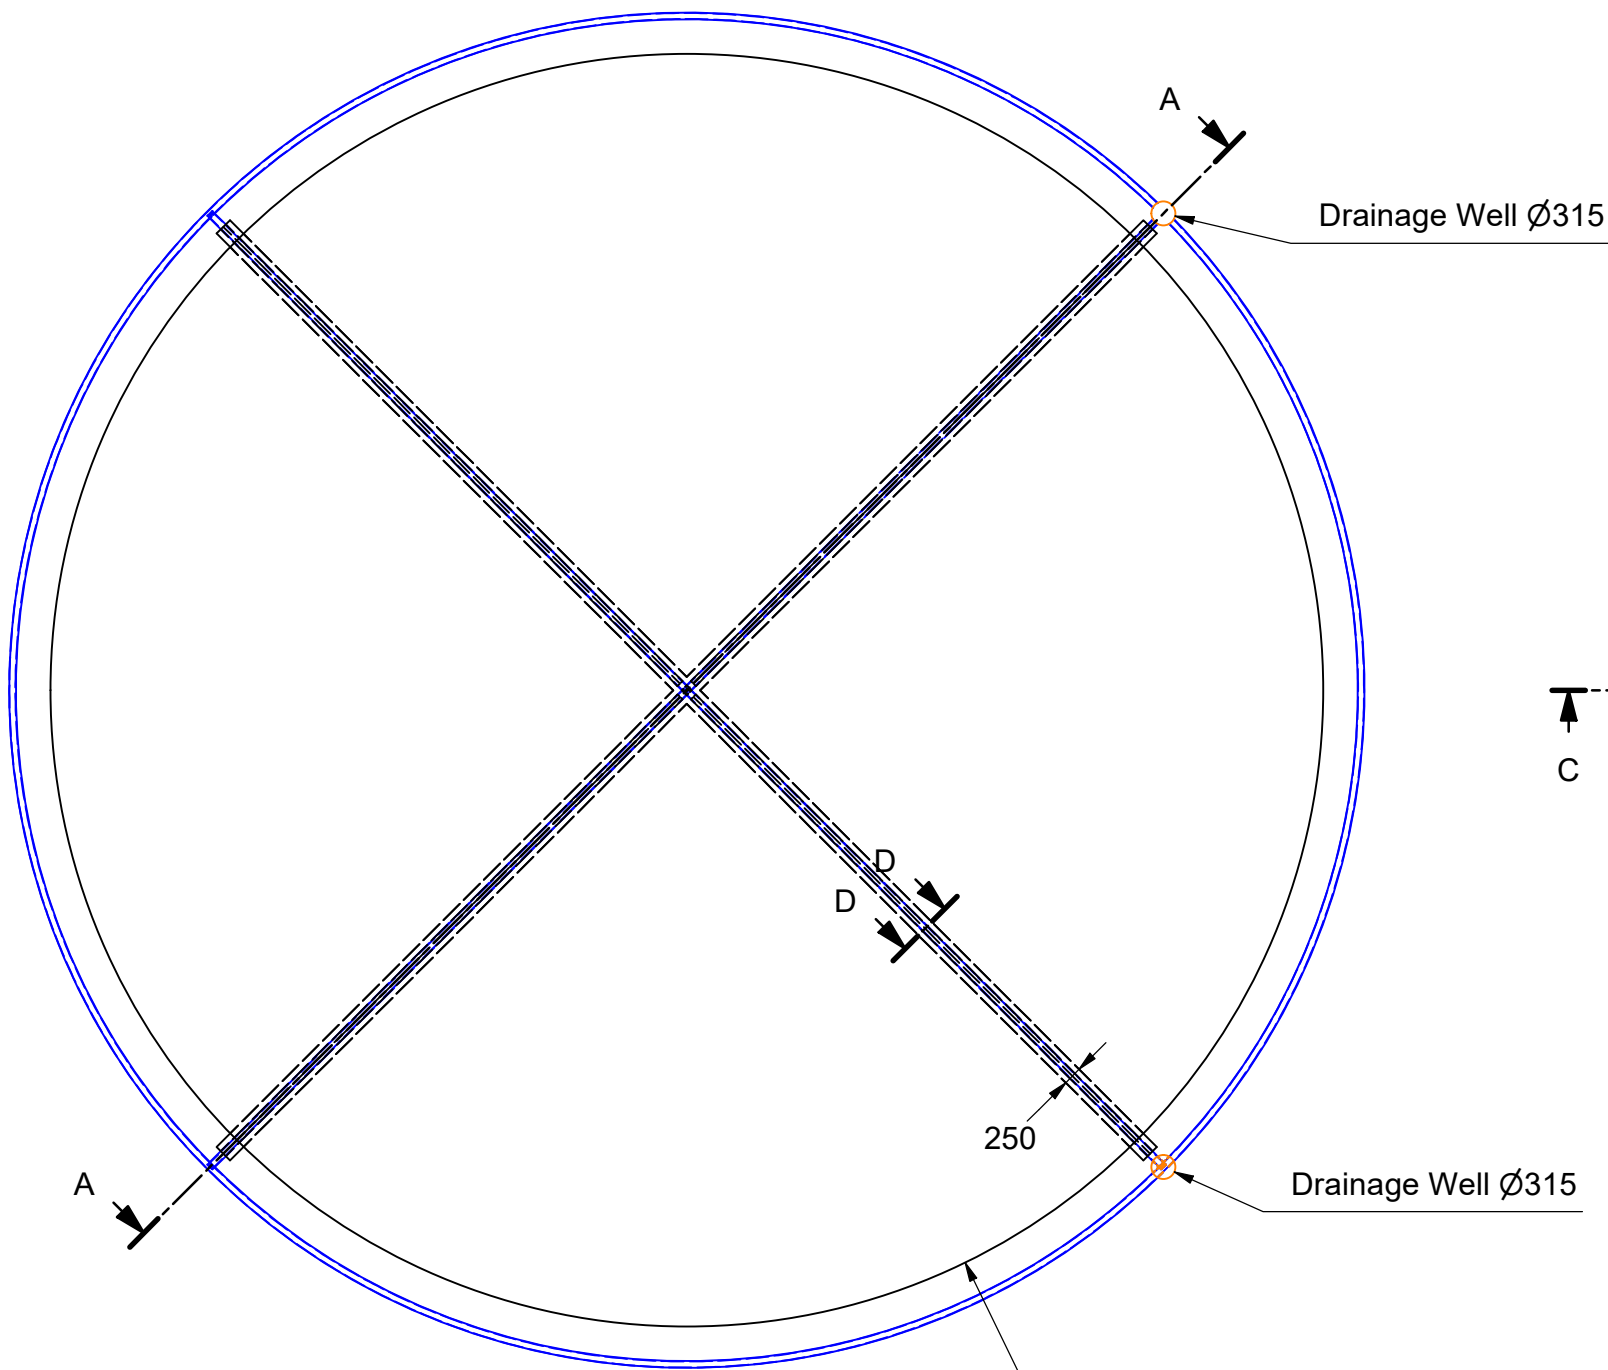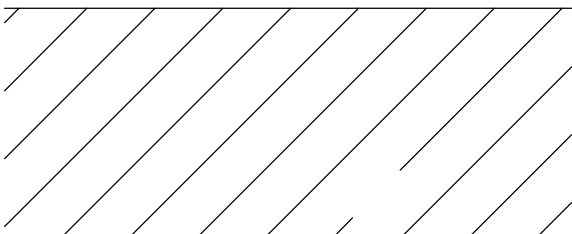


Drainage Well Ø315

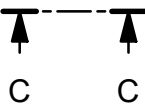

Drainage Well Ø315

Ø16840

D-D ( 1 : 10 )

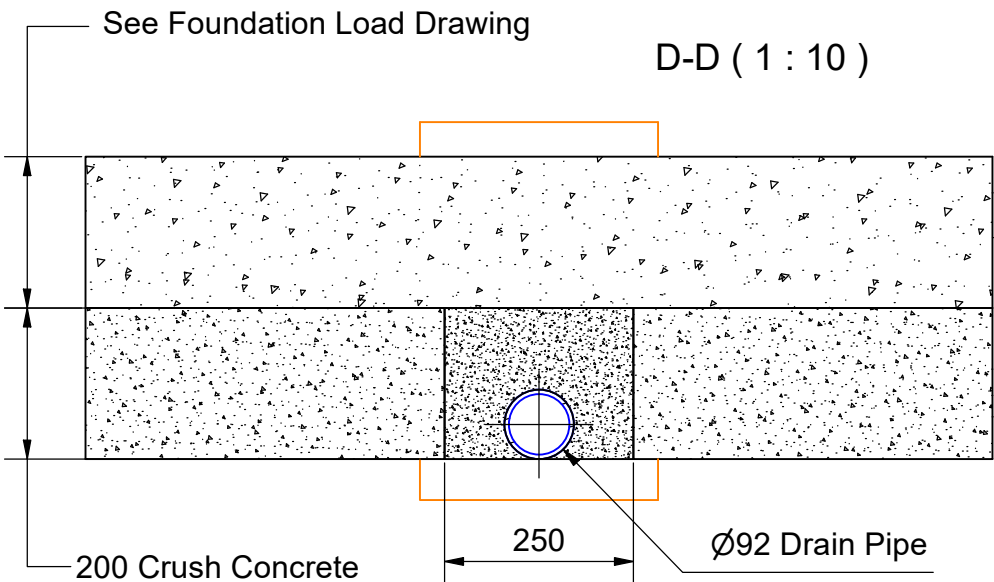

See Foundation Load Drawing

200 Crush Concrete

250

Ø92 Drain Pipe

|                                                                                                   |   |   |   |
|---------------------------------------------------------------------------------------------------|---|---|---|
| Denne tegning må ikke overlades til, kopieres eller udnyttes af uvedkommende uden vor tilladelse. | This drawing remains our property. Its use without due authority is forbidden, and will lead to legal action. | Diese Zeichnung ist unser Eigentum. Unbefugte Benutzung ist verboten und wird gerichtlich verfolgt. | Le dessin est notre propriété. Toute utilisation induue est interdité sous peine de poursuites légales. |
| BIGADAN                                                                                           |   |   |   |
| 4003 - Nurmo Bioenergia                                                                           |   |   |   |
| Mixing Area 02                                                                                    |   |   |   |
| Mixing Tank 2 Foundation                                                                          |   |   |   |
| Engineer / Assistant                                                                              |   | KMJ / JLH                                                                                           |   |
| Scale                                                                                             |   | 1 : 100                                                                                             |   |
| Size                                                                                              |   | A2 (420x594 mm)                                                                                     |   |
| Dwg No                                                                                            |   | 4003-613-F02                                                                                        |   |
| Date :                                                                                            |   | 15-07-2020                                                                                          |   |
|                                                                                                   |   | Sheet : 1 of 1                                                                                      |   |